ZONA DV	Nº TAL.	DATA PL.	ÁREA (ha)	VARIEDADE
999 6.21 %	1	04/2022	17.75	RB 975201
	2	06/2023	7.00	
	3		26.59	
	4		10.88	
TOTAL PLANTIO			62.22	--------


ÁREAS	(ha)	(%)
PLANTIO	62.22	95.68
CARREADORES	2.81	4.32
OUTROS	0.00	0.00
SUB TOTAL AGRICULTÁVEL	65.03	100.00
AP.P.	0.00	0.00
ÁRVORES	0.00	0.00
OUTROS	0.00	0.00
SUB TOTAL NÃO AGRICULT.	0.00	0.00
ÁREA TOTAL	65.03	100.00

C. NÍVEL: 3546.69 m/l 0.82 ha 1.25 %


LEGENDA

- FAZENDA
- TALHÃO
- CURVA DE NÍVEL
- CARREADOR
- CONFRONTANTE
- REDE ELÉTRICA
- TRAJETO VAZIO
- TRAJETO CARREGADO

PLANTIO MANUAL - ESPAÇAMENTO: 1.50 X 1.50
TIRO MÉDIO ESTIMADO: 237.84 m

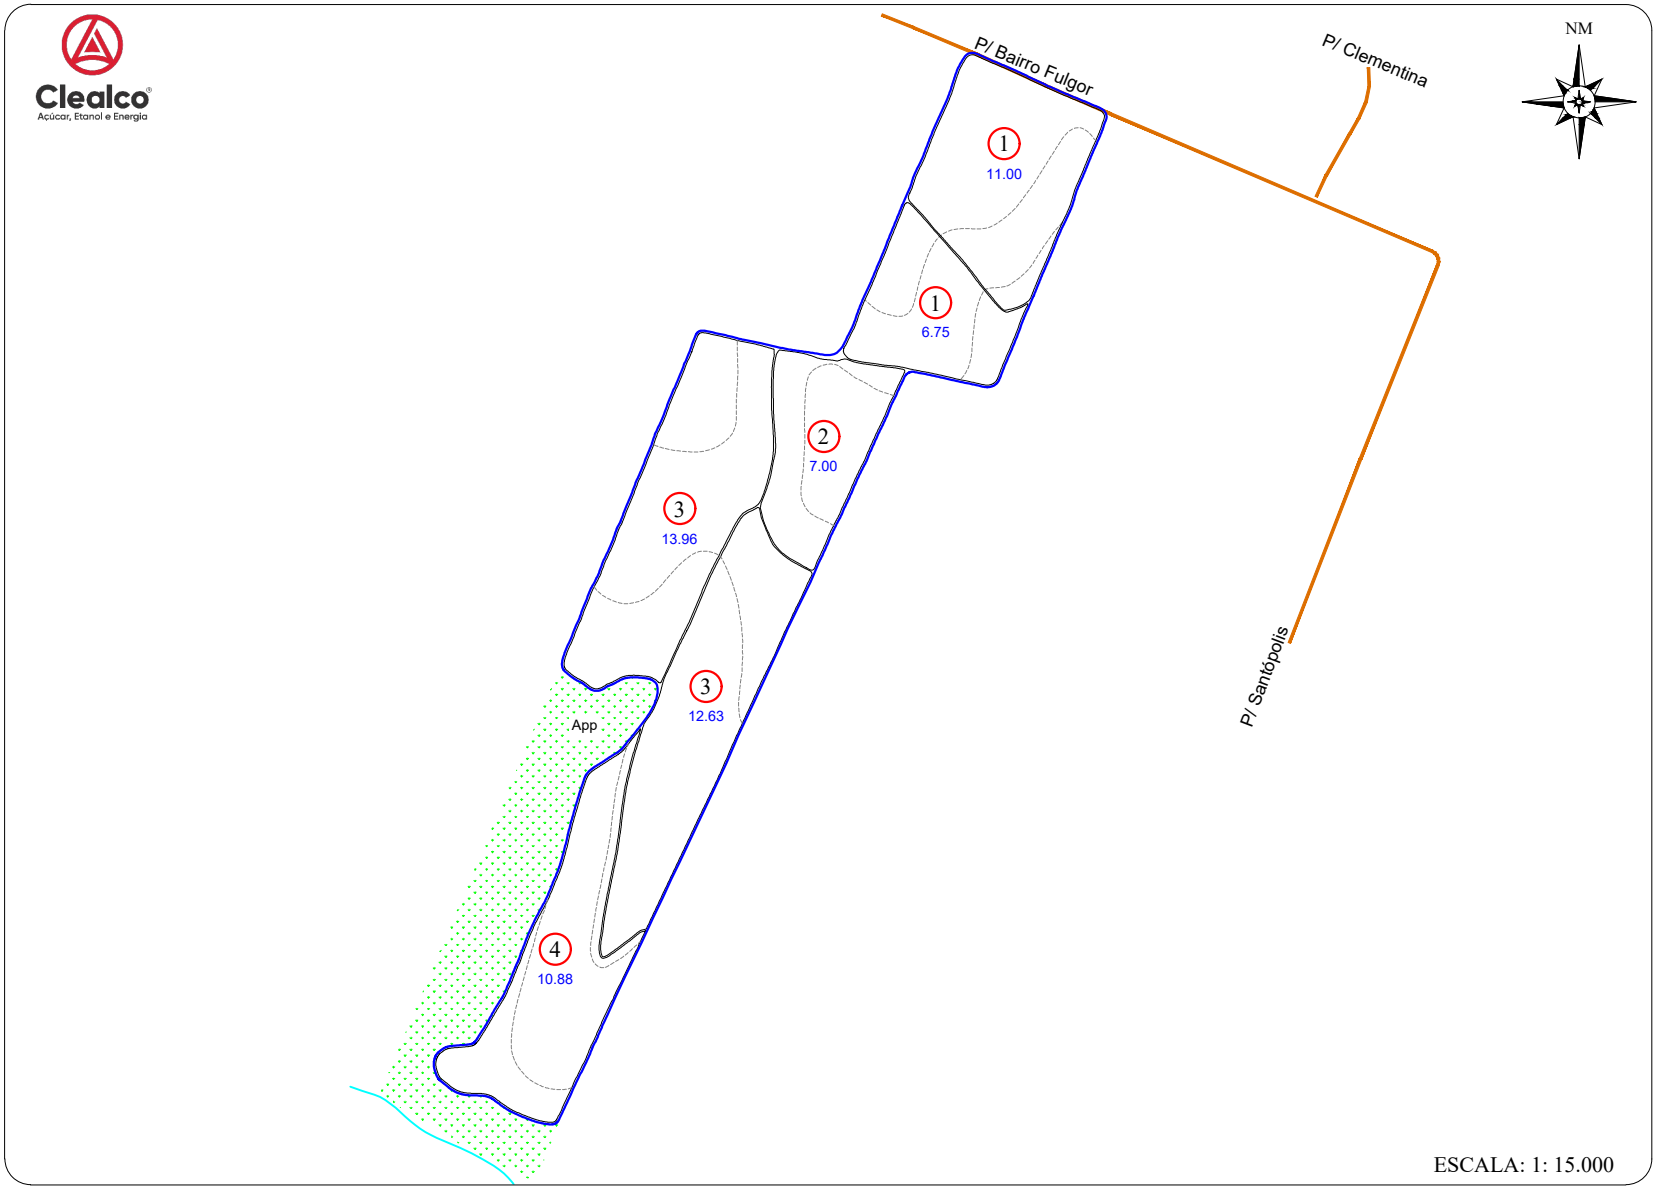

CROQUI DE ACESSO

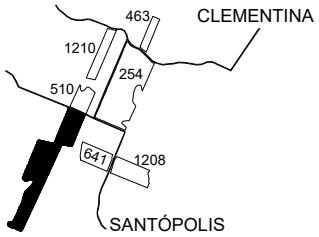

SÍTIO FLOR DA SERRA

PROPRIETÁRIO: JOSÉ FRANCISCO MARTINS
ARRENDATÁRIO: CLEALCO S/A
MUNICÍPIO: CLEMENTINA

DISTÂNCIAS (km):
UNID. I - Asfalto: 11.60 Terra.: 7.10
UNID.I I - Asfalto: 51.00 Terra.: 7.10
UNID. III -Asfalto: 52.00 Terra.: 7.10

COORDENADAS: E(X): 549829.05 N(Y): 7610509.54
LAT: -21°36'27.9637" LONG: -50°31'6.8688"

CLEALCO - AÇÚCAR E ALCOOL S/A - DEPARTAMENTO DE TOPOGRAFIA

UNIDADE: I
PARTE: A/A
FUNDO AGRÍCOLA: 306966

M:\03-Projetos (Sistematização, Pré, Pós e outros)\Terceiro\2023\Edvaldo\306966 - Sitio Flor da Serra (Jose Francisco Martins) Pos plantio - 2023.dwg

Bruno Gamboa 17/10/23