
Clealco
Açúcar, Etanol e Energia

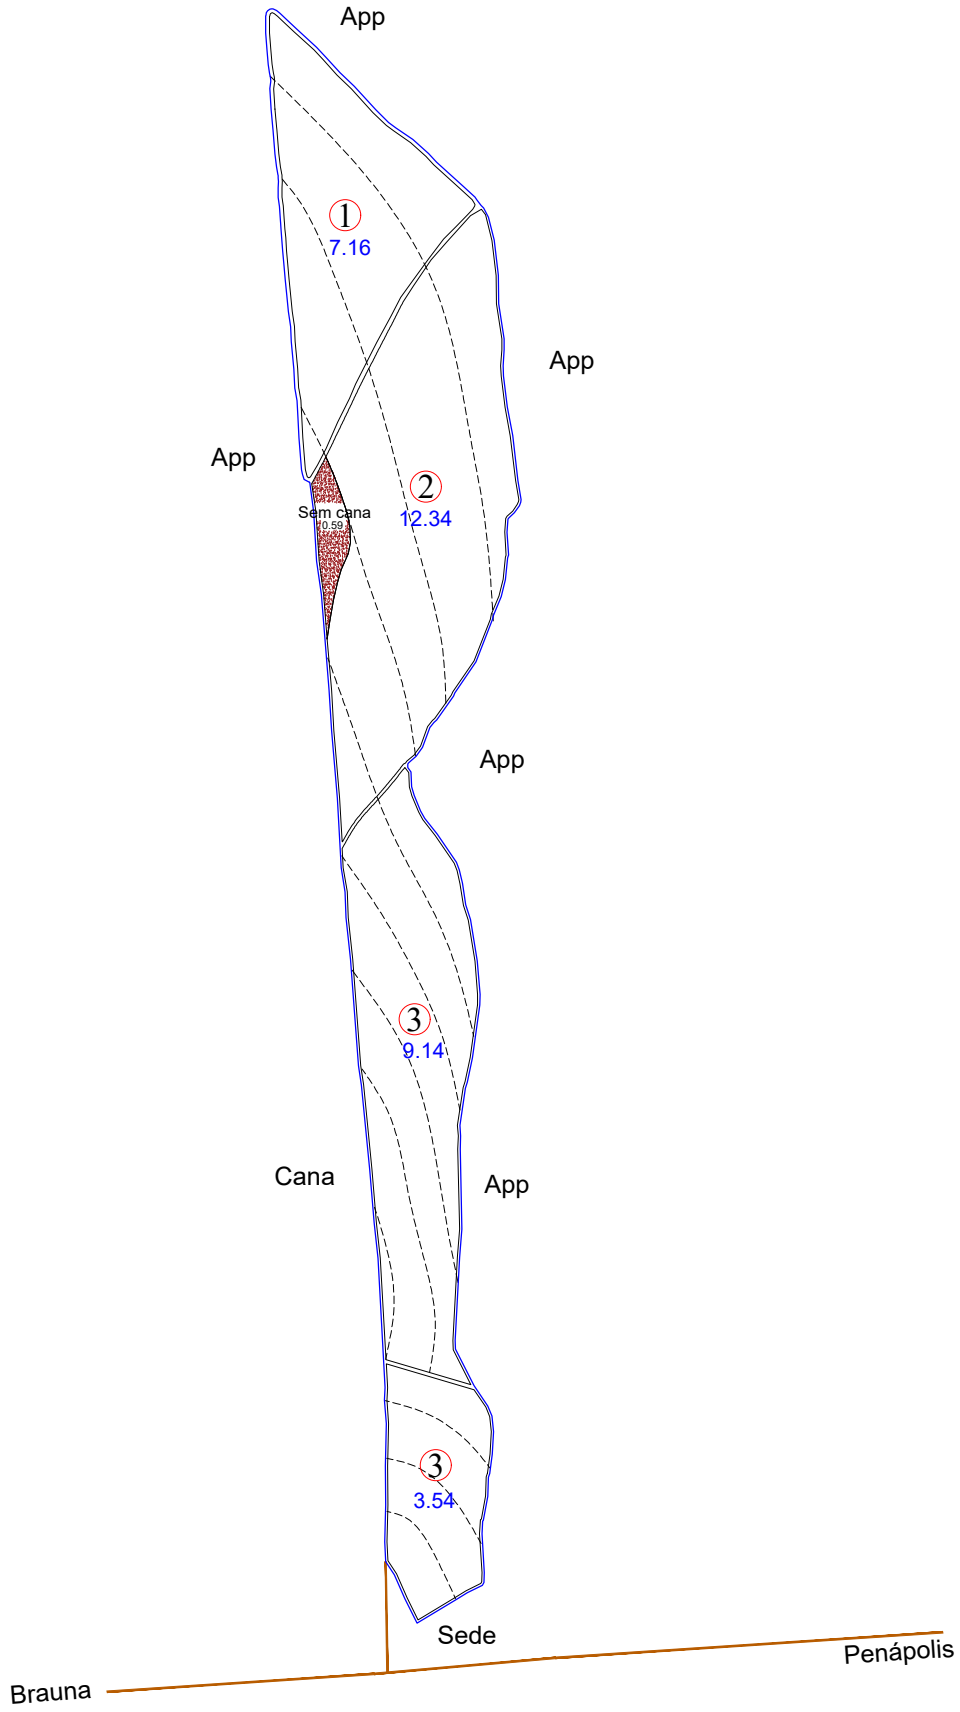

Nº TAL.	DATA PL.	ÁREA (ha)	VARIEDADE
1	04/2025	7.16	CTC4
2	2026	12.34	REFORMA
3		12.68	
TOTAL PLANTIO		32.18	

ÁREAS	(ha)	(%)
PLANTIO	32.18	92.94
CARREADORES	1.86	5.36
OUTROS	0.59	1.70
SUB TOTAL AGRICULTÁVEL	34.63	100.00
AP.P.	0.00	0.00
ÁRVORES	0.00	0.00
OUTROS	0.00	0.00
SUB TOTAL NÃO AGRICULT.	0.00	0.00
ÁREA TOTAL	34.63	100.00

C. NÍVEL: 4404.81 m/l 1.01 ha 2.93 %


LEGENDA

- FAZENDA
- TALHÃO
- REDE ELÉTRICA
- TERRAÇO BASE LARGA
- TERRAÇO EMBUTIDO
- (P.O.A) PATIO DE OPERAÇÃO

ESPAÇAMENTO: 1.50 x 1.50
TIRO MÉDIO ESTIMADO: 319.14 m
D.V: 7.00 %

ESCALA: 1: 10.000

CROQUI DE ACESSO

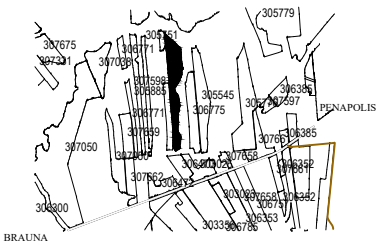

SÍTIO SÃO JOÃO

PROPRIETÁRIO: NILTON CEZÁRIO ANNELI
COMPRADOR: CLEALCO
MUNICÍPIO: PENÁPOLIS - SP

DISTÂNCIAS (km):
UNID. I - Asfalto: 31.00 Terra.: 2.20
UNID.I I - Asfalto: 70.00 Terra.: 2.20

COORDENADAS: E(X): 580231.10 N(Y): 7625175.67
LAT: -21°28'26.9802" LONG: -50°13'32.0297"

CLEALCO - AÇÚCAR E ALCOOL S/A - DEPARTAMENTO DE GEOTECNOLOGIA

LEVANTAMENTO VIA:
- SATÉLITE
- GPS / VANT
- GOOGLE

UNIDADE: I
PARTE: A/A
FUNDO AGRÍCOLA: 306969

M:\01-Mapa de safra\Mapas Atualizados\Terceiro\306969 - Sitio São João (Nilton Cezário Anneli)\306969 - Sitio São João (Nilton Cezário Anneli).dwg

Benati 23/02/2026