ZONA DV	CLA	Nº TAL.	DATA PL.	ÁREA (ha)	VAR.
999 4.56 %		1	04/2020	25.79	CTC 04
TOTAL PLANTIO				25.79	--------

ÁREAS	(ha)	(%)
PLANTIO	25.79	95.59
CARREADORES	1.19	4.41
OUTROS	0.00	0.00
SUB TOTAL AGRICULTÁVEL	26.98	100.00
VÁRZEA	0.00	0.00
MATA	0.00	0.00
OUTROS	0.00	0.00
SUB TOTAL NÃO AGRICULT.	0.00	0.00
ÁREA TOTAL	26.98	100.00


C. NÍVEL:

LEGENDA

- FAZENDA
- TALHÃO
- CURVA DE NÍVEL
- CARREADOR
- CONFRONTANTE
- REDE ELÉTRICA
- TRAJETO VAZIO
- TRAJETO CARREGADO


PLANTIO MANUAL - ESPAÇAMENTO: 1.50 X 1.50
TIRO MÉDIO ESTIMADO: 150.79 m

Clealco
Açúcar, Etanol e Energia

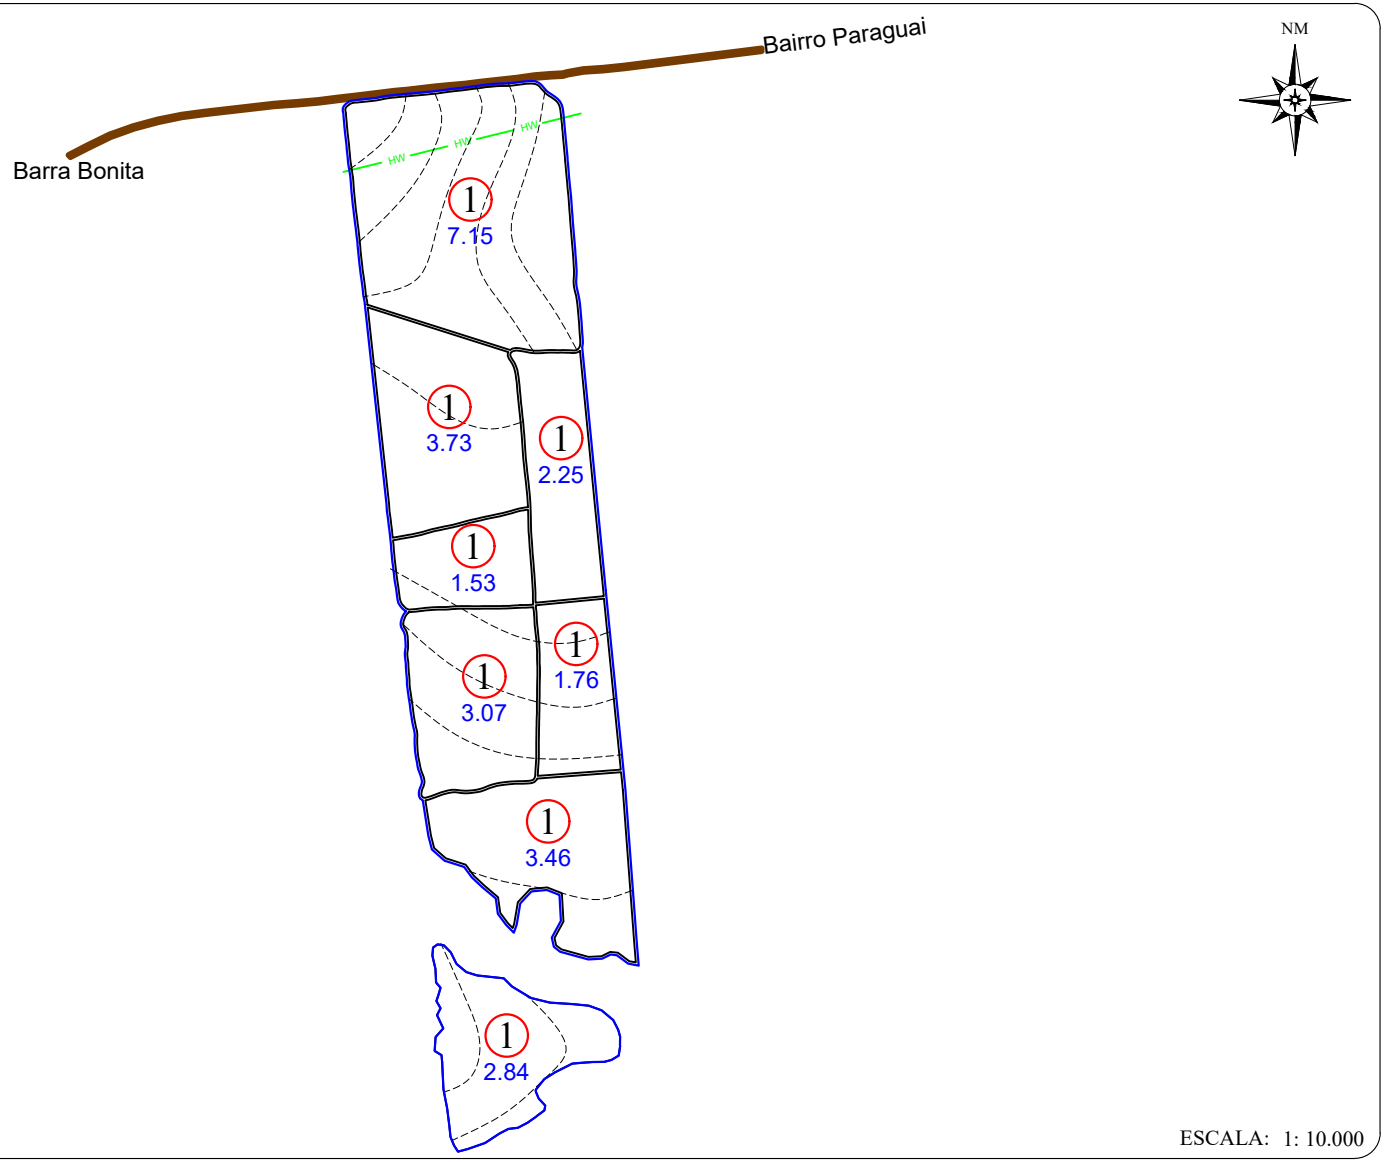

ESCALA: 1: 10.000

CROQUI DE ACESSO

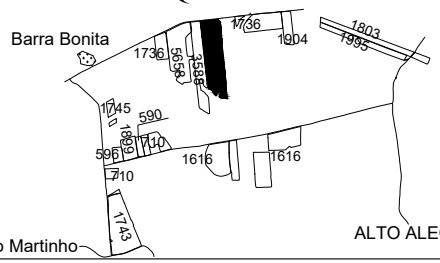

SÍTIO SÃO PEDRO

PROPRIETÁRIO: GENILSON A. DOS SANTOS
COMPRADOR: CLEALCO S/A
MUNICÍPIO: PENÁPOLIS

DISTÂNCIAS (km):
UNID. I - Asfalto: 33.00 Terra.: 7.50
UNID.I I - Asfalto: 71.00 Terra.: 00.00
UNID. III -Asfalto: 00.00 Terra.: 13.30

COORDENADAS: E(X): 581648 N(Y): 7619703
LAT: 21° 31' 24,73959" LONG: 50° 12' 41,83804"

CLEALCO - AÇÚCAR E ALCOOL S/A - DEPARTAMENTO DE TOPOGRAFIA

UNIDADE: I
PARTE: A/A
FUNDO AGRÍCOLA: 307034

M:\01-Mapa de safra\Mapas Atualizados\Terceiro\307034 - Sítio São Pedro (Genilson Antonio dos Santos)\307034 - Sítio São Pedro (Genilson Antonio dos Santos) - 2023.dwg