
Clealco
Açúcar, Etanol e Energia

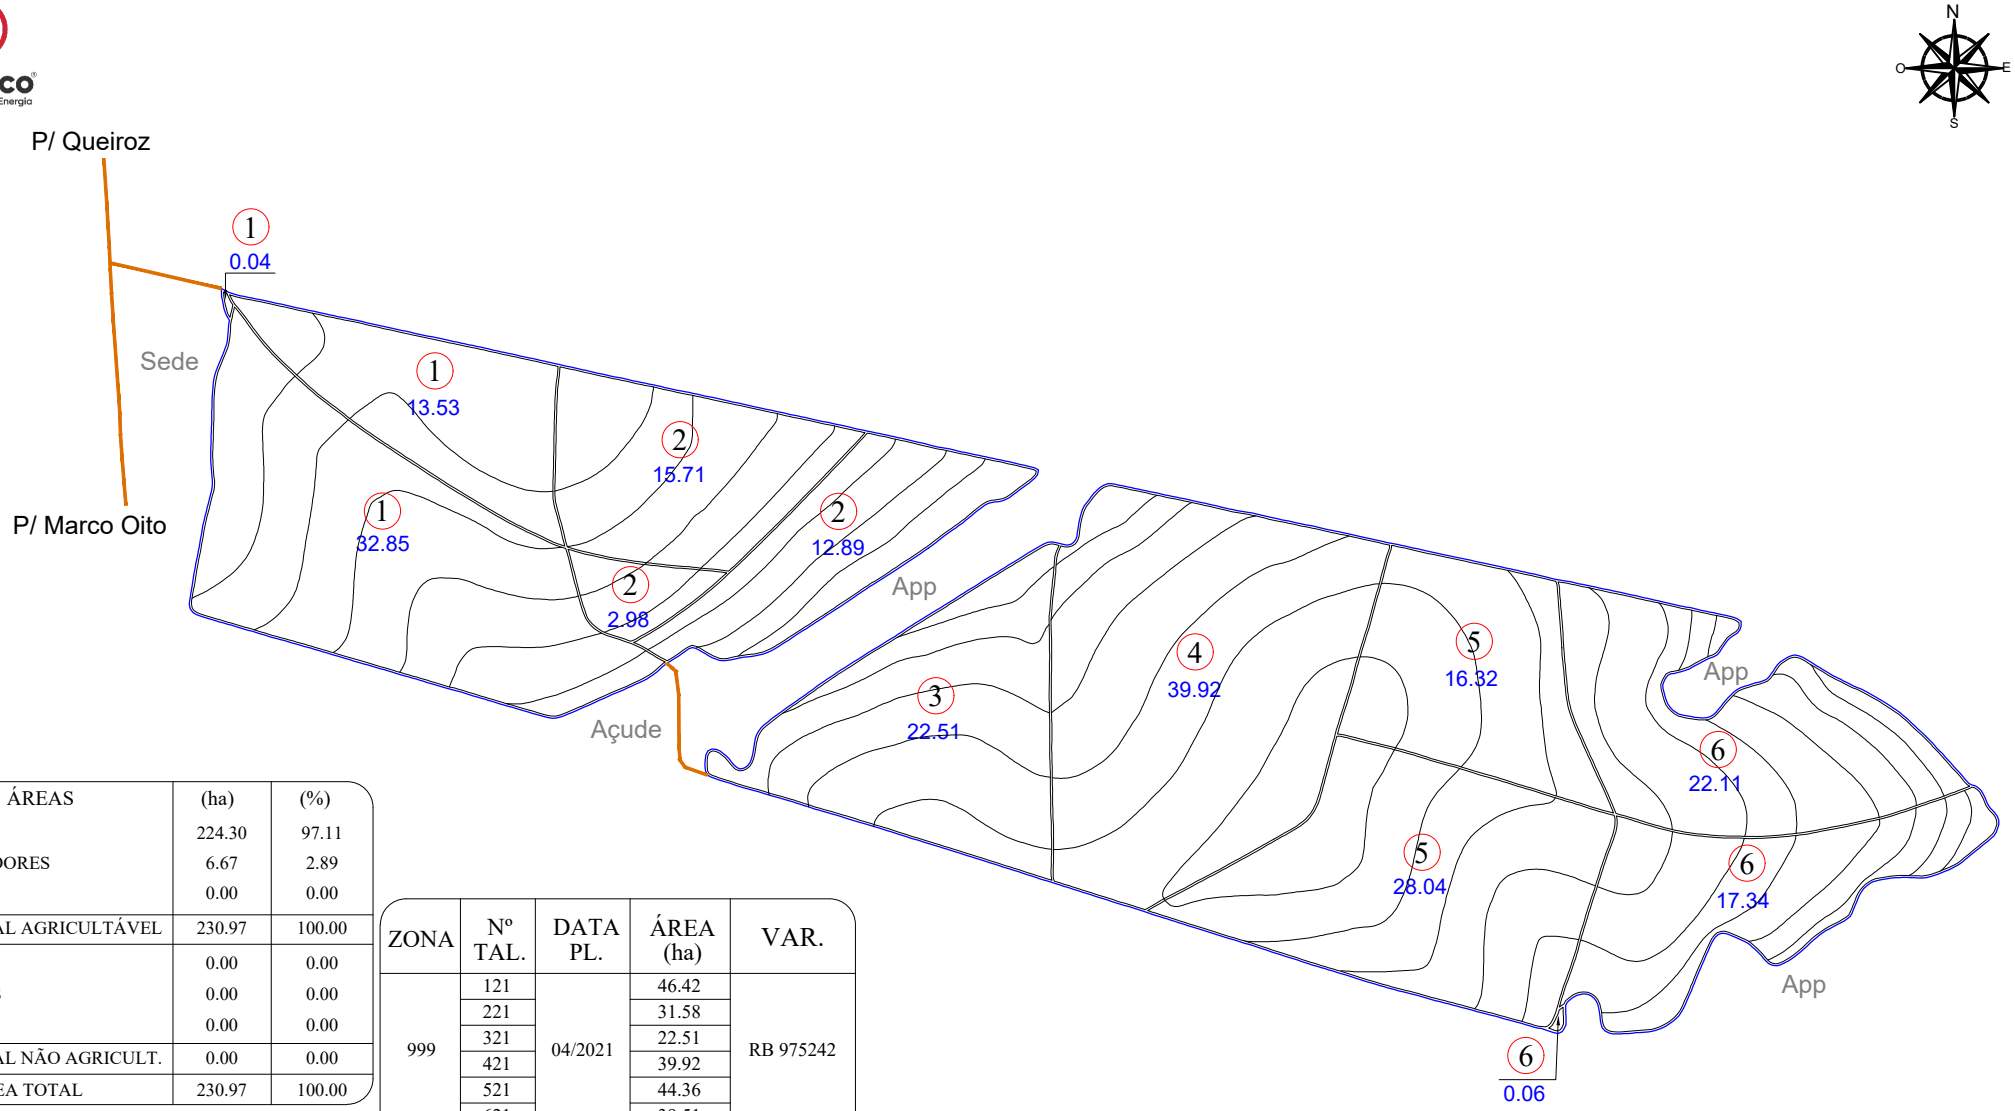

ÁREAS	(ha)	(%)
PLANTIO	224.30	97.11
CARREADORES	6.67	2.89
OUTROS	0.00	0.00
SUB TOTAL AGRICULTÁVEL	230.97	100.00
AP.P.	0.00	0.00
ÁRVORES	0.00	0.00
OUTROS	0.00	0.00
SUB TOTAL NÃO AGRICULT.	0.00	0.00
ÁREA TOTAL	230.97	100.00

C. NÍVEL: 21920.66 m/l 5.04 ha 2.18 %


ZONA	Nº TAL.	DATA PL.	ÁREA (ha)	VAR.
999	121	04/2021	46.42	RB 975242
	221		31.58	
	321		22.51	
	421		39.92	
	521		44.36	
	621		39.51	
TOTAL PLANTIO			224.30	

ESCALA: 1: 15.000

LEGENDA
- FAZENDA
- TALHÃO
- REDE ELÉTRICA
- TERRAÇO BASE LARGA
- TERRAÇO EMBUTIDO
- VAZIO
- CARREGADO

ESPAÇAMENTO: 1.50 x 1.50
TIRO MÉDIO ESTIMADO: 000.00 m
D.V: 0.00 %

CROQUI DE ACESSO

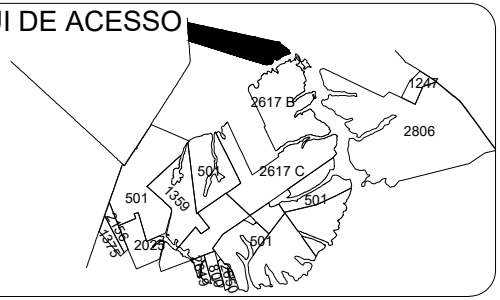

FAZENDA SÃO LUIZ

PROPRIETÁRIO: ALICE CISNEROS FERNANDES
COMPRADOR: CLEALCO
MUNICÍPIO: QUEIROZ - SP

DISTÂNCIAS (km):
UNID. I - Asfalto: 65.70 Terra.: 5.00
UNID.I I - Asfalto: 6.70 Terra.: 5.00

COORDENADAS: E(X): 579542.49 N(Y): 7580166.95
LAT: -21°52'50.8988" LONG: -50°13'48.1935"
CLEALCO - AÇÚCAR E ALCOOL S/A - DEPARTAMENTO DE GEOTECNOLOGIA

LEVANTAMENTO VIA:
SATÉLITE
GPS / VANT
GOOGLE

UNIDADE: II
PARTE: A/A
FUNDO AGRÍCOLA: 307037

M:\01-Mapa de safra\Mapas Atualizados\Terceiro\307037 - Fazenda Sao Luiz (Felipe de Figueiredo Ferraz)\307037 - Fazenda Sao Luiz (Felipe de Figueiredo Ferraz).dwg

Bruno Gamboa 25/05/26