ZONA D.V.	Nº TAL.	DATA PL.	ÁREA (ha)	VARIEDADE
999 4.82 %	1	05/2023	38.63	RB 975242
TOTAL PLANTIO			38.63	--------

ÁREAS	(ha)	(%)
PLANTIO	38.63	95.69
CARREADORES	1.42	3.52
OUTROS	0.00	0.00
SUB TOTAL AGRICULTÁVEL	40.05	99.21
AP.P.	0.09	0.22
ÁRVORES	0.23	0.57
OUTROS	0.00	0.00
SUB TOTAL NÃO AGRICULT.	0.32	0.79
ÁREA TOTAL	40.37	100.00

C. NÍVEL:	2975.81 m/l	0.68 ha	1.70 %

LEGENDA

🟦 FAZENDA	▬ CONFRONTANTE
▬ TALHÃO	- - REDE ELÉTRICA
▪▪▪▪ CURVA DE NÍVEL	⇨ TRAJETO VAZIO
— CARREADOR	→ TRAJETO CARREGADO

PLANTIO MANUAL - ESPAÇAMENTO: 1.50 X 1.50
TIRO MÉDIO ESTIMADO: 485.22 m

Clealco
Açúcar, Etanol e Energia

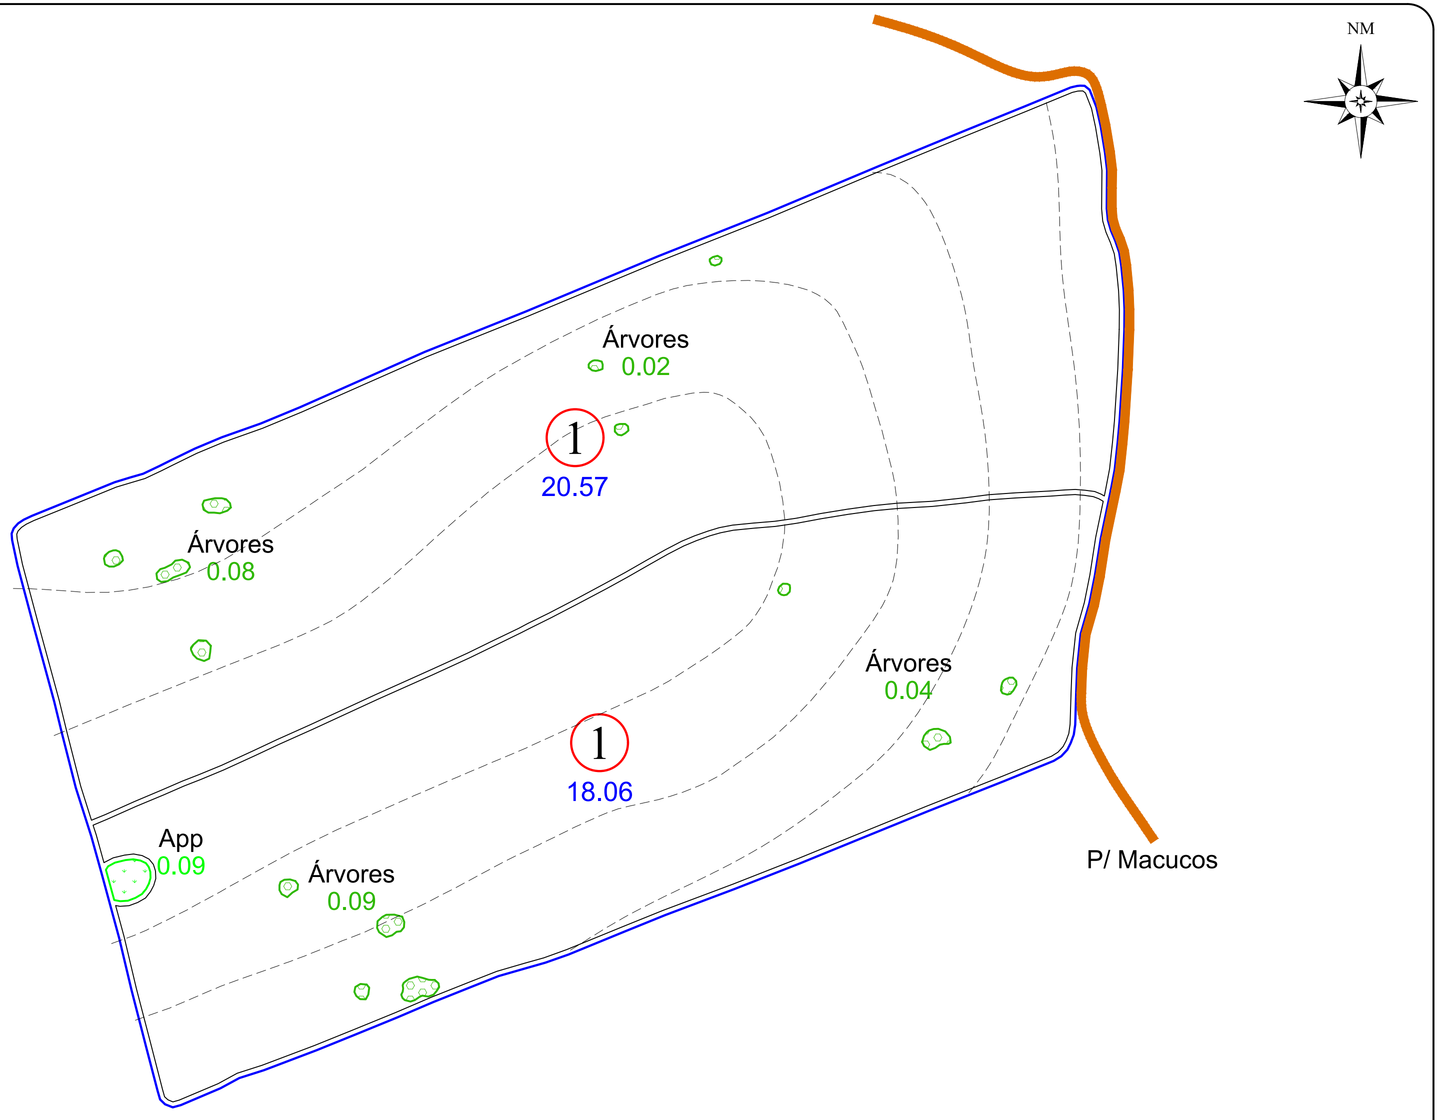

ESCALA: 1: 7.000

CROQUI DE ACESSO

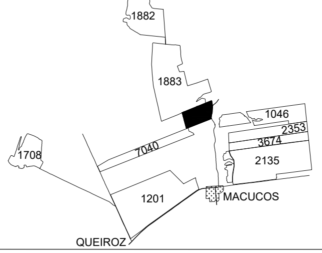

SITIO SÃO LUIZ

PROPRIETÁRIO: CARLOS CESAR DE S. FILHO
COMPRADOR: CLEALCO S/A
MUNICÍPIO: GETULINA

DISTÂNCIAS (km):

	Asfalto		Terra
UNID. I - Asfalto:	73.00	Terra.:	2.50
UNID.I I - Asfalto:	16.50	Terra.:	2.50
UNID. III -Asfalto:	59.00	Terra.:	2.50

COORDENADAS: E(X): 591818.92 N(Y): 7597308.69
LAT: -21°43'31.2734" LONG: -50°6'43.8724"

CLEALCO - AÇÚCAR E ALCOOL S/A - DEPARTAMENTO DE TOPOGRAFIA

UNIDADE:
II

PARTE:
A/A

FUNDO AGRÍCOLA:
307047

M:\01-Mapa de safra\Mapas Atualizados\Terceiro\307047 - Sítio São Luiz (Carlos Cesar Filho)\307047 - Sítio São Luiz (Carlos Cesar Filho).dwg

Fernanda Bezerra 25/01/24