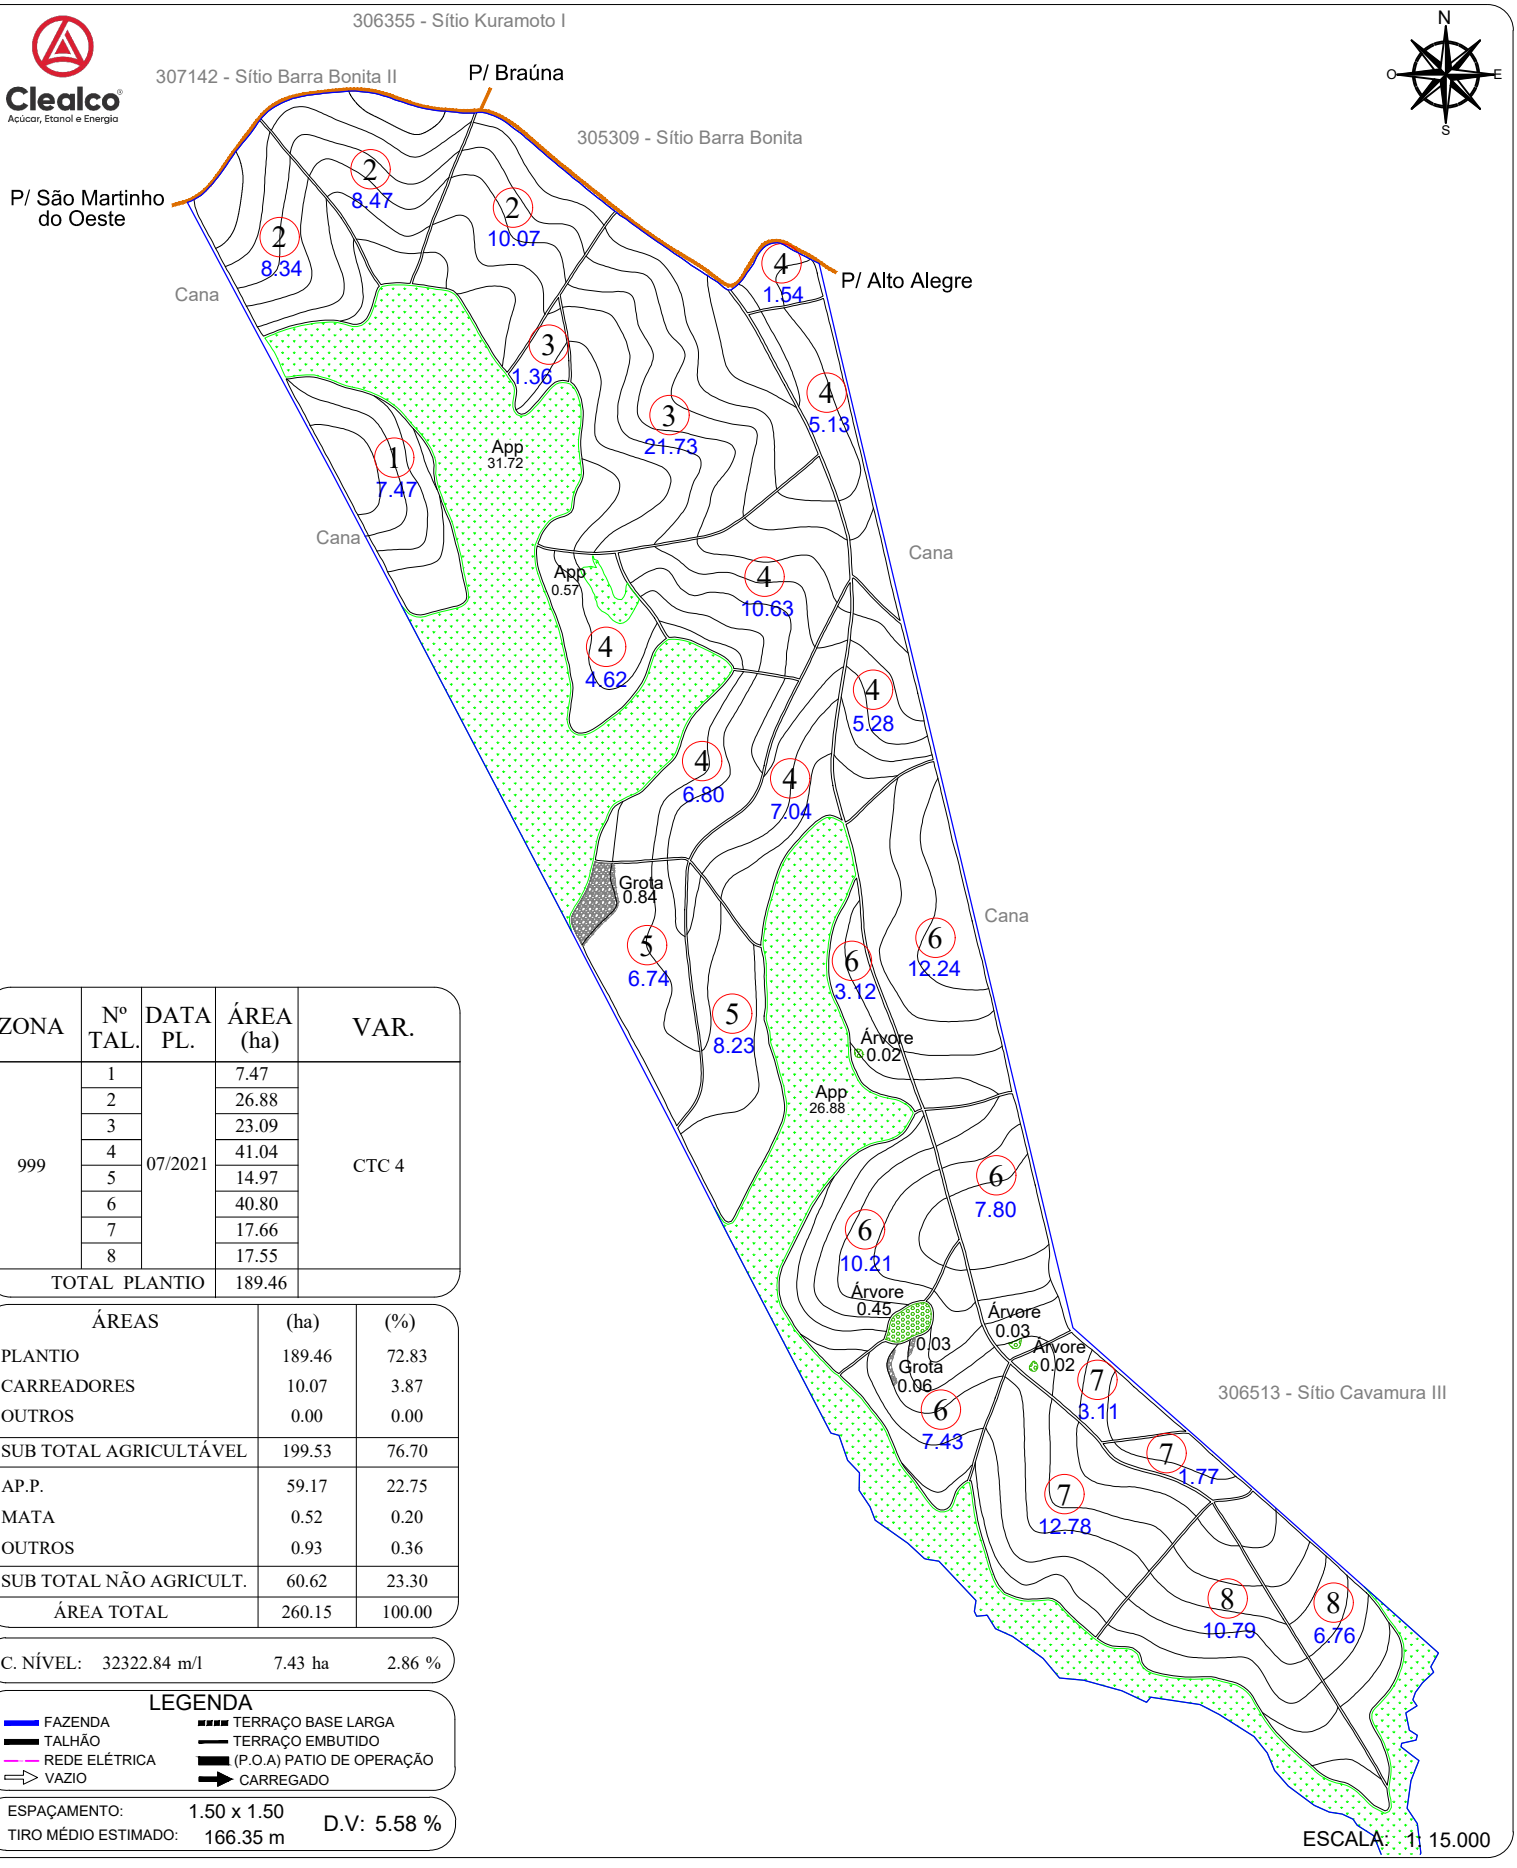


ZONA	Nº TAL.	DATA PL.	ÁREA (ha)	VAR.
999	1	07/2021	7.47	CTC 4
	2		26.88	
	3		23.09	
	4		41.04	
	5		14.97	
	6		40.80	
	7		17.66	
	8		17.55	
TOTAL PLANTIO			189.46	

ÁREAS	(ha)	(%)
PLANTIO	189.46	72.83
CARREADORES	10.07	3.87
OUTROS	0.00	0.00
SUB TOTAL AGRICULTÁVEL	199.53	76.70
AP.P.	59.17	22.75
MATA	0.52	0.20
OUTROS	0.93	0.36
SUB TOTAL NÃO AGRICULT.	60.62	23.30
ÁREA TOTAL	260.15	100.00

C. NÍVEL: 32322.84 m/l 7.43 ha 2.86 %


LEGENDA

- FAZENDA
- TALHÃO
- REDE ELÉTRICA
- VAZIO
- TERRAÇO BASE LARGA
- TERRAÇO EMBUTIDO
- (P.O.A) PATIO DE OPERAÇÃO
- CARREGADO

ESPAÇAMENTO: 1.50 x 1.50
TIRO MÉDIO ESTIMADO: 166.35 m
D.V: 5.58 %

ESCALA: 1: 15.000

CROQUI DE ACESSO

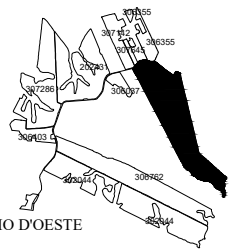

SAO MARTINHO D'OESTE

FAZENDA RIO FEIO

PROPRIETÁRIO: JULIO CESAR DAS NEVES E OUTROS
COMPRADOR: CLEALCO
MUNICÍPIO: ALTO ALEGRE

DISTÂNCIAS (km):
UNID. I - Asfalto: 25.00 Terra.: 7.50
UNID.I I - Asfalto: 72.50 Terra.: 15.00

COORDENADAS: E(X): 578887.10 N(Y): 7615862.39
LAT: -21°33'30.0947" LONG: -50°14'17.1510"

CLEALCO - AÇÚCAR E ALCOOL S/A - DEPARTAMENTO DE GEOTECNOLOGIA

LEVANTAMENTO VIA:
- SATÉLITE
- GPS / VANT
- GOOGLE

UNIDADE: I
PARTE: A/A
FUNDO AGRÍCOLA: 307070

M:\01-Mapa de safra\Mapas Atualizados\Terceiro\307070 - Fazenda Rio Feio (Julio Cesar das Neves)\307070 - Fazenda Rio Feio (Julio Cesar das Neves).dwg

Bruno Gamboa 10/07/26