ZONA	Nº TAL.	DATA PL.	ÁREA (ha)	VAR.
999	1	06/2021	35.51	CTC 04
	2		23.09	
	3		17.37	
	4		2.51	
TOTAL PLANTIO			78.48	--------

ÁREAS	(ha)	(%)
PLANTIO	78.48	92.54
CARREADORES	3.94	4.65
OUTROS	0.32	0.38
SUB TOTAL AGRICULTÁVEL	82.74	97.57
AP.P.	0.19	0.22
ÁRVORES	0.00	0.00
OUTROS	1.87	2.21
SUB TOTAL NÃO AGRICULT.	2.06	2.43
ÁREA TOTAL	84.80	100.00


C. NÍVEL: 14740.68 m/l 3.39 ha 4.00 %

LEGENDA

- FAZENDA
- TALHÃO
- CURVA DE NÍVEL
- CARREADOR
- CONFRONTANTE
- REDE ELÉTRICA
- TRAJETO VAZIO
- TRAJETO CARREGADO


PLANTIO MANUAL - ESPAÇAMENTO: 1.50 X 1.50

Clealco
Açúcar, Etanol e Energia

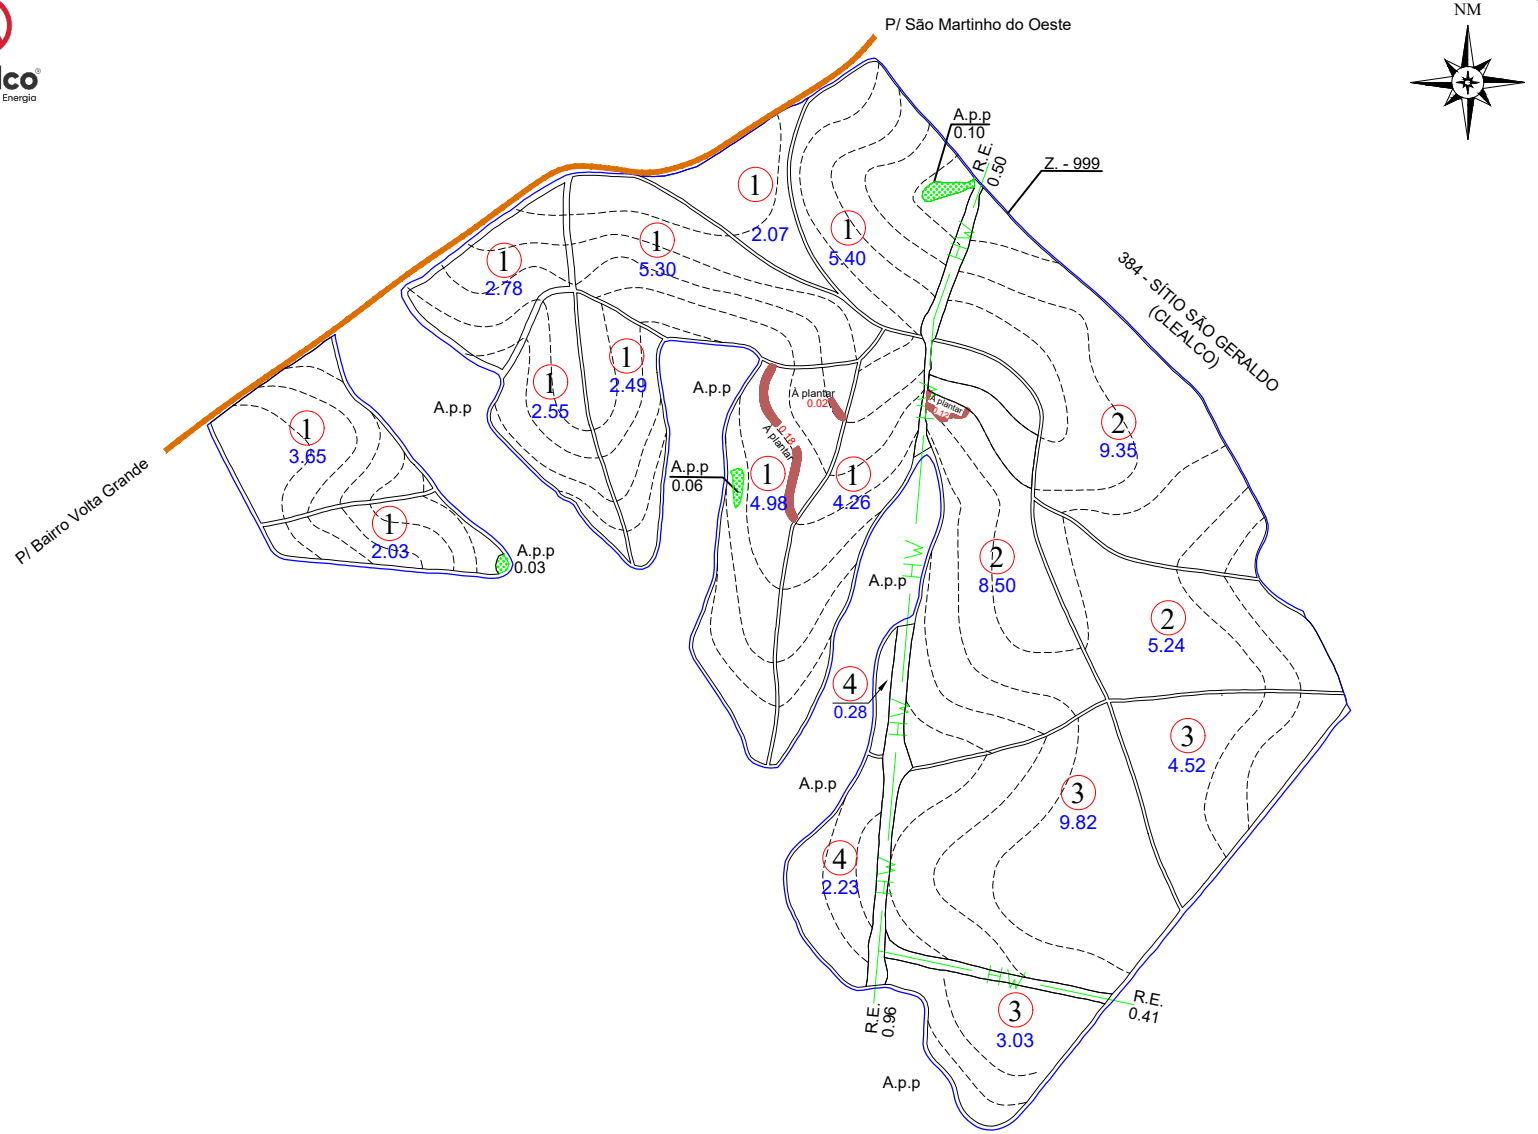

ESCALA: 1: 10.000

CROQUI DE ACESSO

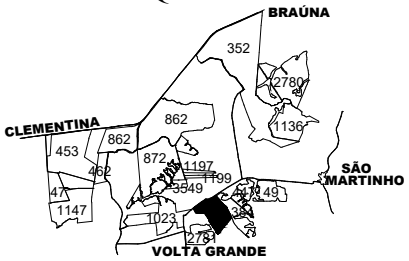

SÍTIO BEIJA FLOR

PROPRIETÁRIO: CLEALCO S/A
FORNECEDOR: ADALTO LUIZ GAVIOLI E OUTRO
MUNICÍPIO: BRAÚNA - SP

DISTÂNCIAS (km):
UNID. I - Asfalto: 13.50 Terra.: 8.50
UNID.I I - Asfalto: 23.00 Terra.: 10.50
UNID. III -Asfalto: 32.00 Terra.: 10.50

COORDENADAS: E(X): 571.091.00 N(Y): 7.612.665.00
LAT: 21º 35' 15,26377" LONG: 50º 18' 47,71052"

CLEALCO - AÇÚCAR E ALCOOL S/A - DEPARTAMENTO DE TOPOGRAFIA

UNIDADE: I
PARTE: A/A
FUNDO AGRÍCOLA: 307073

M:\01-Mapa de safra\Mapas Atualizados\Terceiro\307073 - Sítio Beija Flor (Adauto Luiz Gavioli)\307073 - Sítio Beija Flor (Adauto Luiz Gavioli).dwg

Bruno Gamboa 22/01/26