ZONA	Nº TAL.	DATA PL.	ÁREA (ha)	VAR.
999	121	05/2021	46.63	RB 97 5201
	221		40.29	
	321		20.08	
	421		37.29	
TOTAL PLANTIO			144.29	--------

ÁREAS	(ha)	(%)
PLANTIO	144.29	95.18
CARREADORES	6.86	4.53
OUTROS	0.44	0.29
SUB TOTAL AGRICULTÁVEL	151.59	100.00
AP.P.	0.00	0.00
MATA	0.00	0.00
OUTROS	0.00	0.00
SUB TOTAL NÃO AGRICULT.	0.00	0.00
ÁREA TOTAL	151.59	100.00

C. NÍVEL: 23547.11 m/l 5.42 ha 3.57 %


LEGENDA

- FAZENDA
- TALHÃO
- CURVA DE NÍVEL
- CARREADOR
- CONFRONTANTE
- REDE ELÉTRICA
- TRAJETO VAZIO
- TRAJETO CARREGADO

PLANTIO MANUAL - ESPAÇAMENTO: 1.50 X 1.50


Clealco
Açúcar, Etanol e Energia

NM

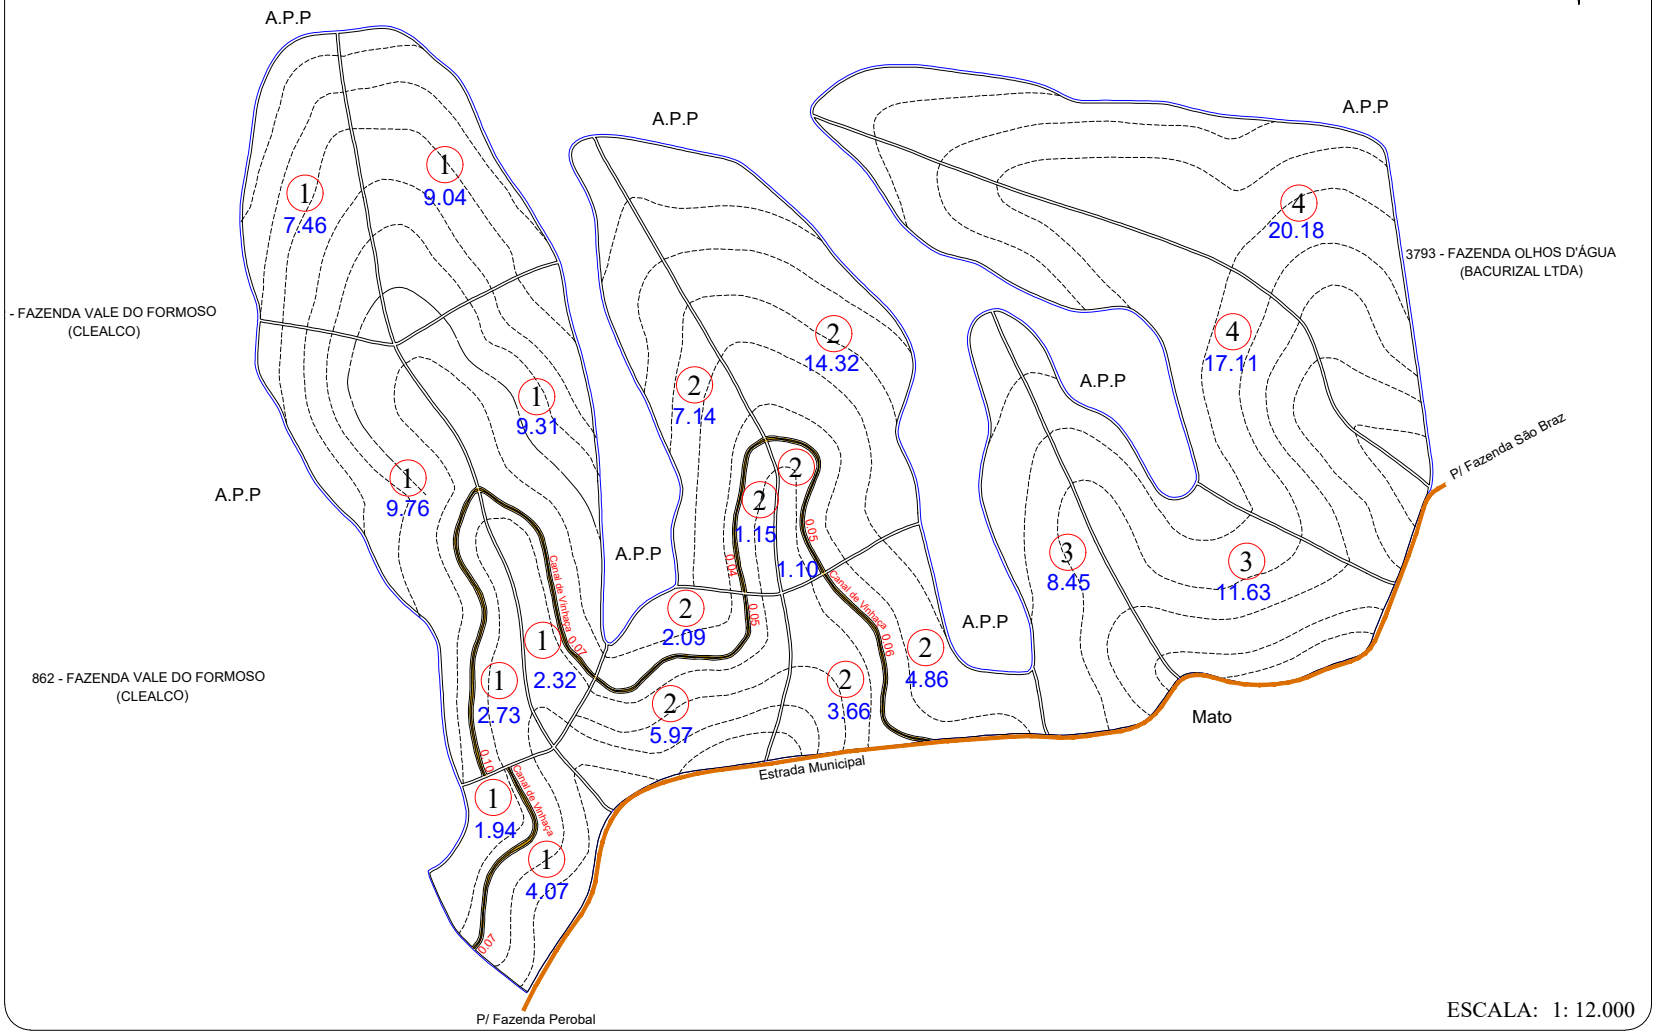

ESCALA: 1: 12.000

CROQUI DE ACESSO

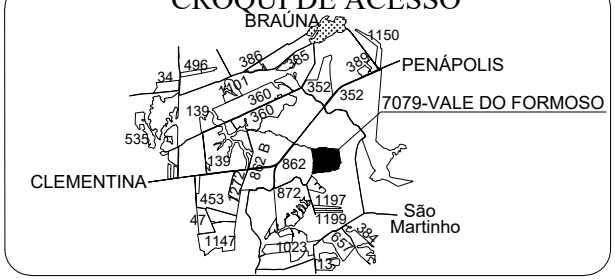

FAZENDA VALE FORMOSO

PROPRIETÁRIO: JORGE LUIZ ZAGO
ARRENDATÁRIO: CLEALCO S/A
MUNICÍPIO: BRAÚNA

DISTÂNCIAS (km):
UNID. I - Asfalto: 11.50 Terra.: 1.50
UNID.I I - Asfalto: 68.00 Terra.: 1.50
UNID. III -Asfalto: 34.00 Terra.: 1.50

COORDENADAS: E(X): 570.009,68 N(Y): 7.616.198,85
LAT: 21°33'20.4831" LONG: 50°19'25.8459"

CLEALCO - AÇÚCAR E ALCOOL S/A - DEPARTAMENTO DE TOPOGRAFIA

UNIDADE: I
PARTE: A/A
FUNDO AGRÍCOLA: 307079

M:\01-Mapa de safra\Mapas Atualizados\Terceiro\307079 - Fazenda Vale Formoso (Jorge Luiz Zago)\307079 - Fazenda Vale Formoso (Jorge Luiz Zago).dwg

Pedro Becker 30/08/21