
Clealco
Açúcar, Etanol e Energia

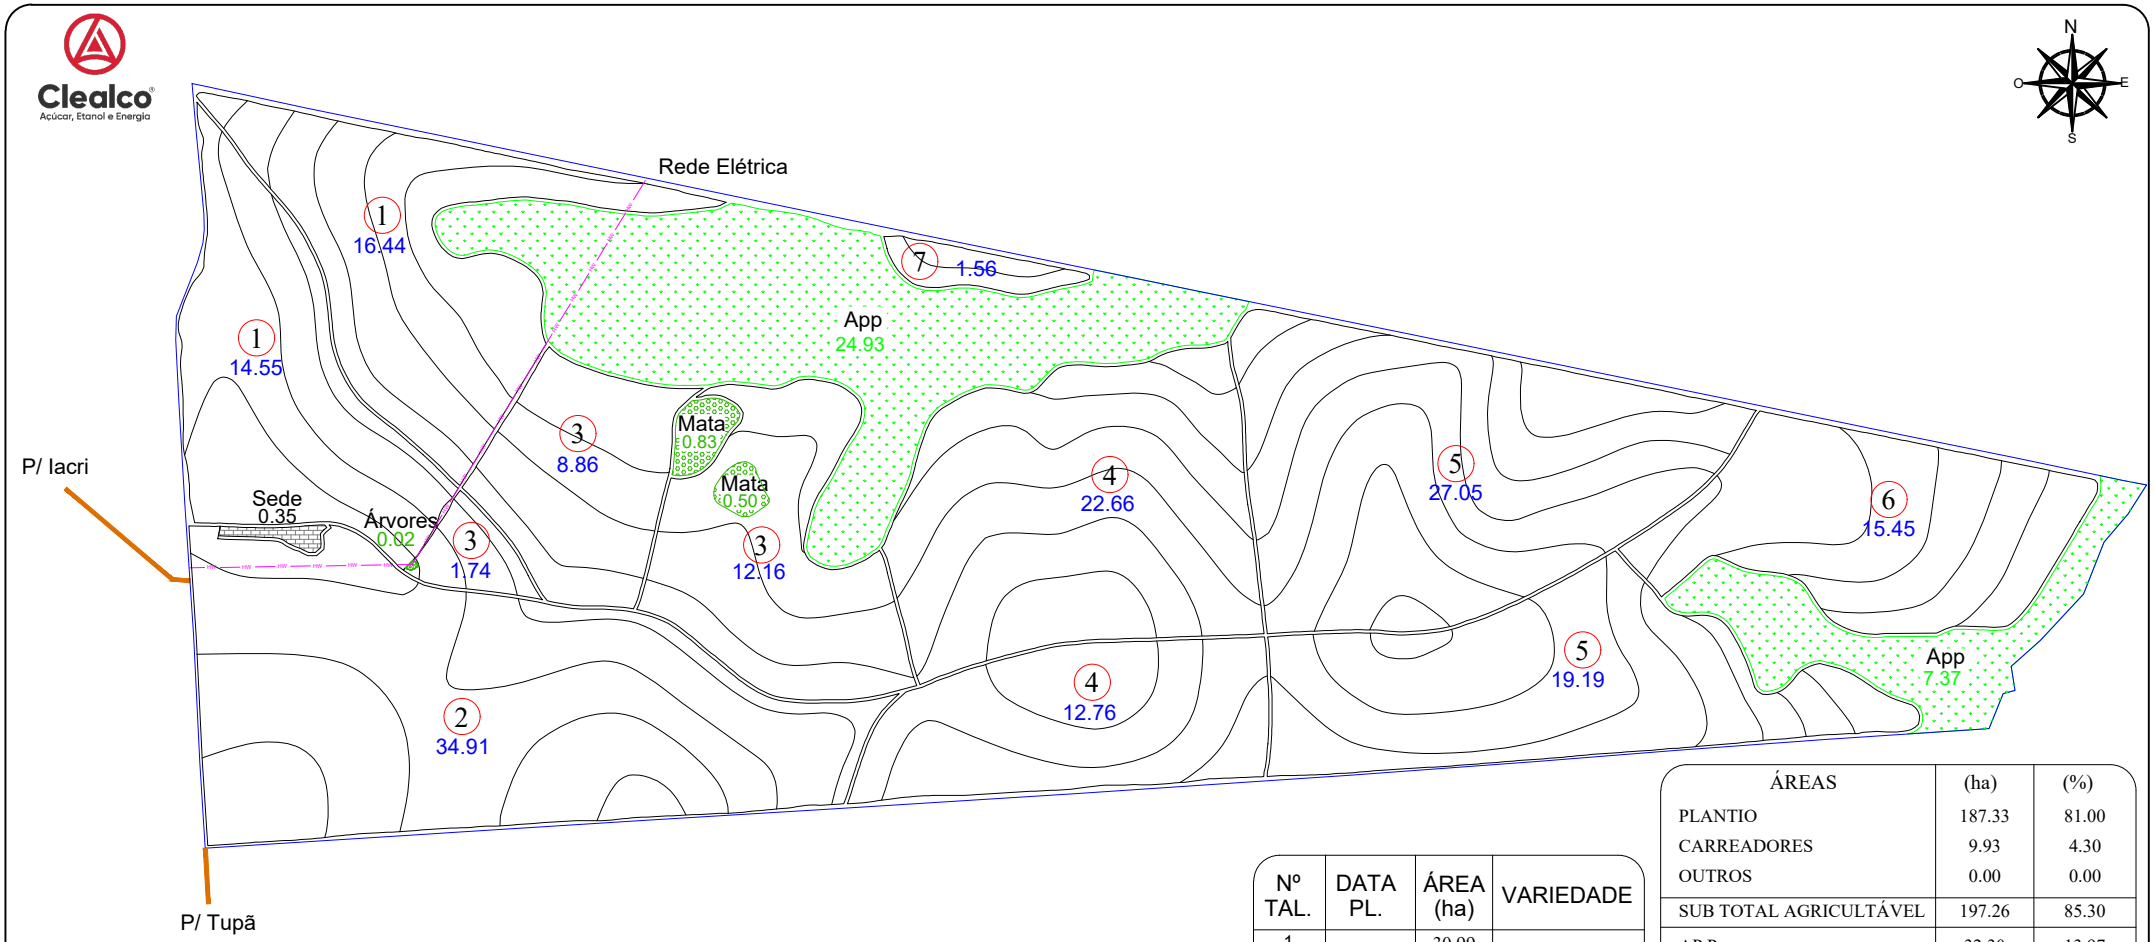

Nº TAL.	DATA PL.	ÁREA (ha)	VARIEDADE
1	04/2026	30.99	PLANTIO 2026
2		34.91	
3		22.76	
4		35.42	
5		46.24	
6		15.45	
7		1.56	
TOTAL PLANTIO		187.33	

ÁREAS	(ha)	(%)
PLANTIO	187.33	81.00
CARREADORES	9.93	4.30
OUTROS	0.00	0.00
SUB TOTAL AGRICULTÁVEL	197.26	85.30
AP.P.	32.30	13.97
MATA	1.35	0.58
OUTROS	0.35	0.15
SUB TOTAL NÃO AGRICULT.	34.00	14.70
ÁREA TOTAL	231.26	100.00


C. NÍVEL: 22883.71 m/l 5.26 ha 2.28 %

ESCALA: 1: 12.000

LEGENDA
- FAZENDA
- TALHÃO
- REDE ELÉTRICA
- TERRAÇO BASE LARGA
- TERRAÇO EMBUTIDO

ESPAÇAMENTO: 1.50 x 1.50
TIRO MÉDIO ESTIMADO: 217.62 m
D.V: 4.97 %

CROQUI DE ACESSO

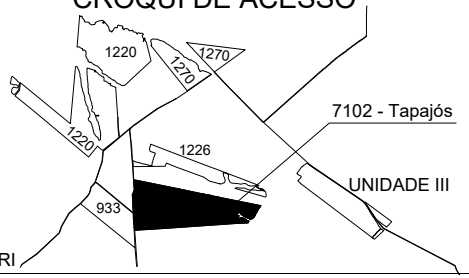

FAZENDA TAPAJÓS

PROPRIETÁRIO: CLAUDEMIR STEFANELI
COMPRADOR: CLEALCO
MUNICÍPIO: IACRI - SP

DISTÂNCIAS (km):
UNID. I - Asfalto: 36.50 Terra.: 8.00
UNID.I I - Asfalto: 71.00 Terra.: 8.00

COORDENADAS: E(X): 541590.56 N(Y): 7584170.35
LAT: -21°50'45.3988" LONG: -50°35'51.0278"
CLEALCO - AÇÚCAR E ALCOOL S/A - DEPARTAMENTO DE GEOTECNOLOGIA

LEVANTAMENTO VIA:
SATÉLITE
GPS / VANT
GOOGLE

UNIDADE: II
PARTE: A/A
FUNDO AGRÍCOLA: 307102

M:\01-Mapa de safra\Mapas Atualizados\Terceiro\307102 - Fazenda Tapajós (Claudemir Stefaneli)\307102 - Fazenda Tapajós (Claudemir Stefanelli).dwg

Bruno Gamboa 27/02/26