ZONA DV	Nº TAL.	DATA PL.	ÁREA (ha)	VAR.
999	1	05/2021	9.29	RB975242
TOTAL PLANTIO			9.29	

ÁREAS	(ha)	(%)
PLANTIO	9.29	95.28
CARREADORES	0.45	4.62
OUTROS	-	-
SUB TOTAL AGRICULTÁVEL	9.74	--------
ÁRVORE	-	-
VÁRZEA	0.01	0.10
OUTROS	-	-
SUB TOTAL NÃO AGRICULT.	0.01	--------
ÁREA TOTAL	9.75	100.00

C. NÍVEL:	947.49 m/l	0.22 ha	2.35 %

LEGENDA

🟦	FAZENDA	▬	CONFRONTANTE
▬	TALHÃO	– HW –	REDE ELÉTRICA
▪▪▪	CURVA DE NÍVEL	⇒	TRAJETO VAZIO
—	CARREADOR	→	TRAJETO CARREGADO

PLANTIO MANUAL - ESPAÇAMENTO: 1.50 x 1.50

Clealco
Açúcar, Etanol e Energia

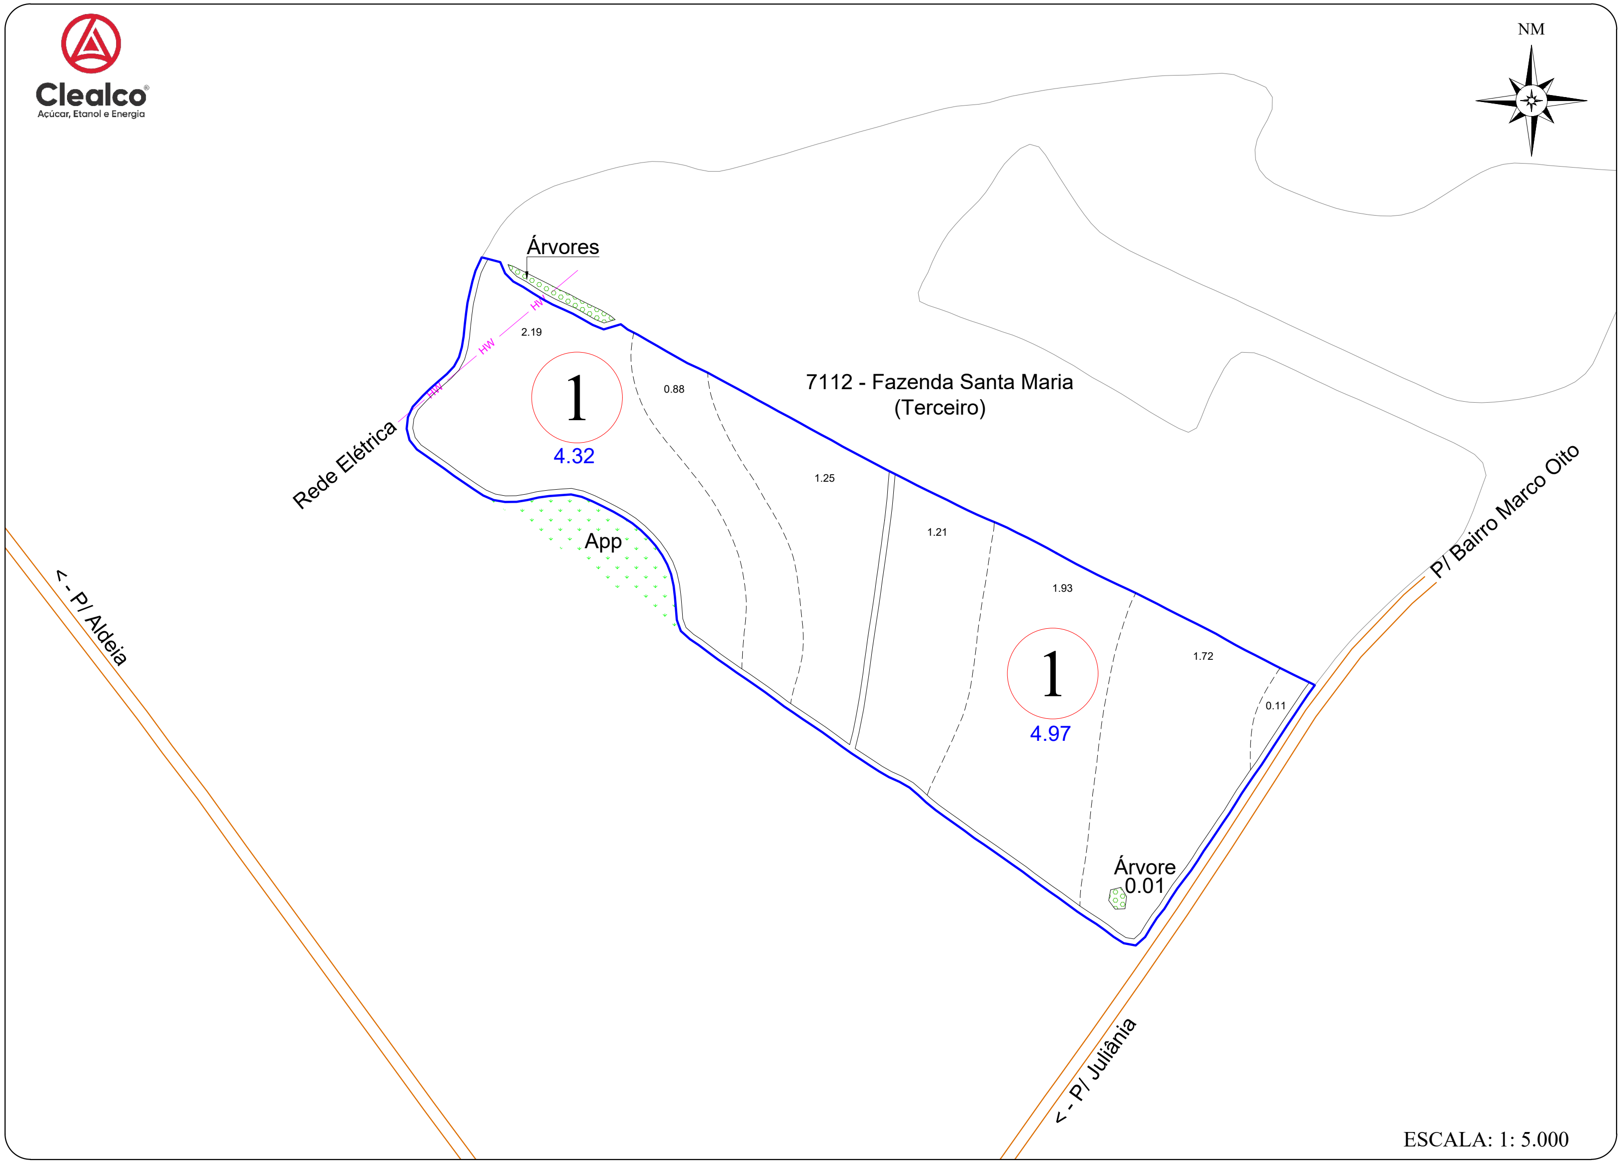

ESCALA: 1: 5.000

CROQUI DE ACESSO

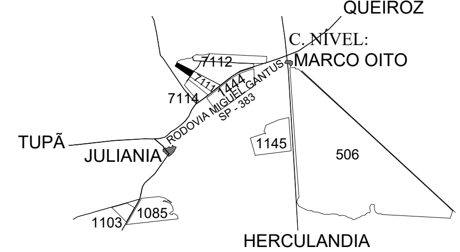

SÍTIO SÃO PAULO

		DISTÂNCIAS (km):			
PROPRIETÁRIO:	GERSON RIBEIRO	UNID. I - Asfalto:	32.50	Terra.:	24.50
COMPRADOR:	CLEALCO S/A	UNID.I I - Asfalto:	18.00	Terra.:	2.00
MUNICÍPIO:	HERCULANDIA	UNID. III -Asfalto:	88.00	Terra.:	2.00

COORDENADAS: E(X): 566051.3020 N(Y): 7580773.8842
LAT: 21° 52' 32,89901" LONG: 50° 21' 38,39189"

CLEALCO - AÇÚCAR E ALCOOL S/A - DEPARTAMENTO DE TOPOGRAFIA

UNIDADE:
II

PARTE:
A/A

FUNDO AGRÍCOLA:
307113

M:\01-Mapa de safra\Mapas Atualizados\Terceiro\307113 - Sítio São Paulo (Gerson Ribeiro)\307113 - Sítio São Paulo (Gerson Ribeiro).dwg

Fernanda Bezerra 21/06/21