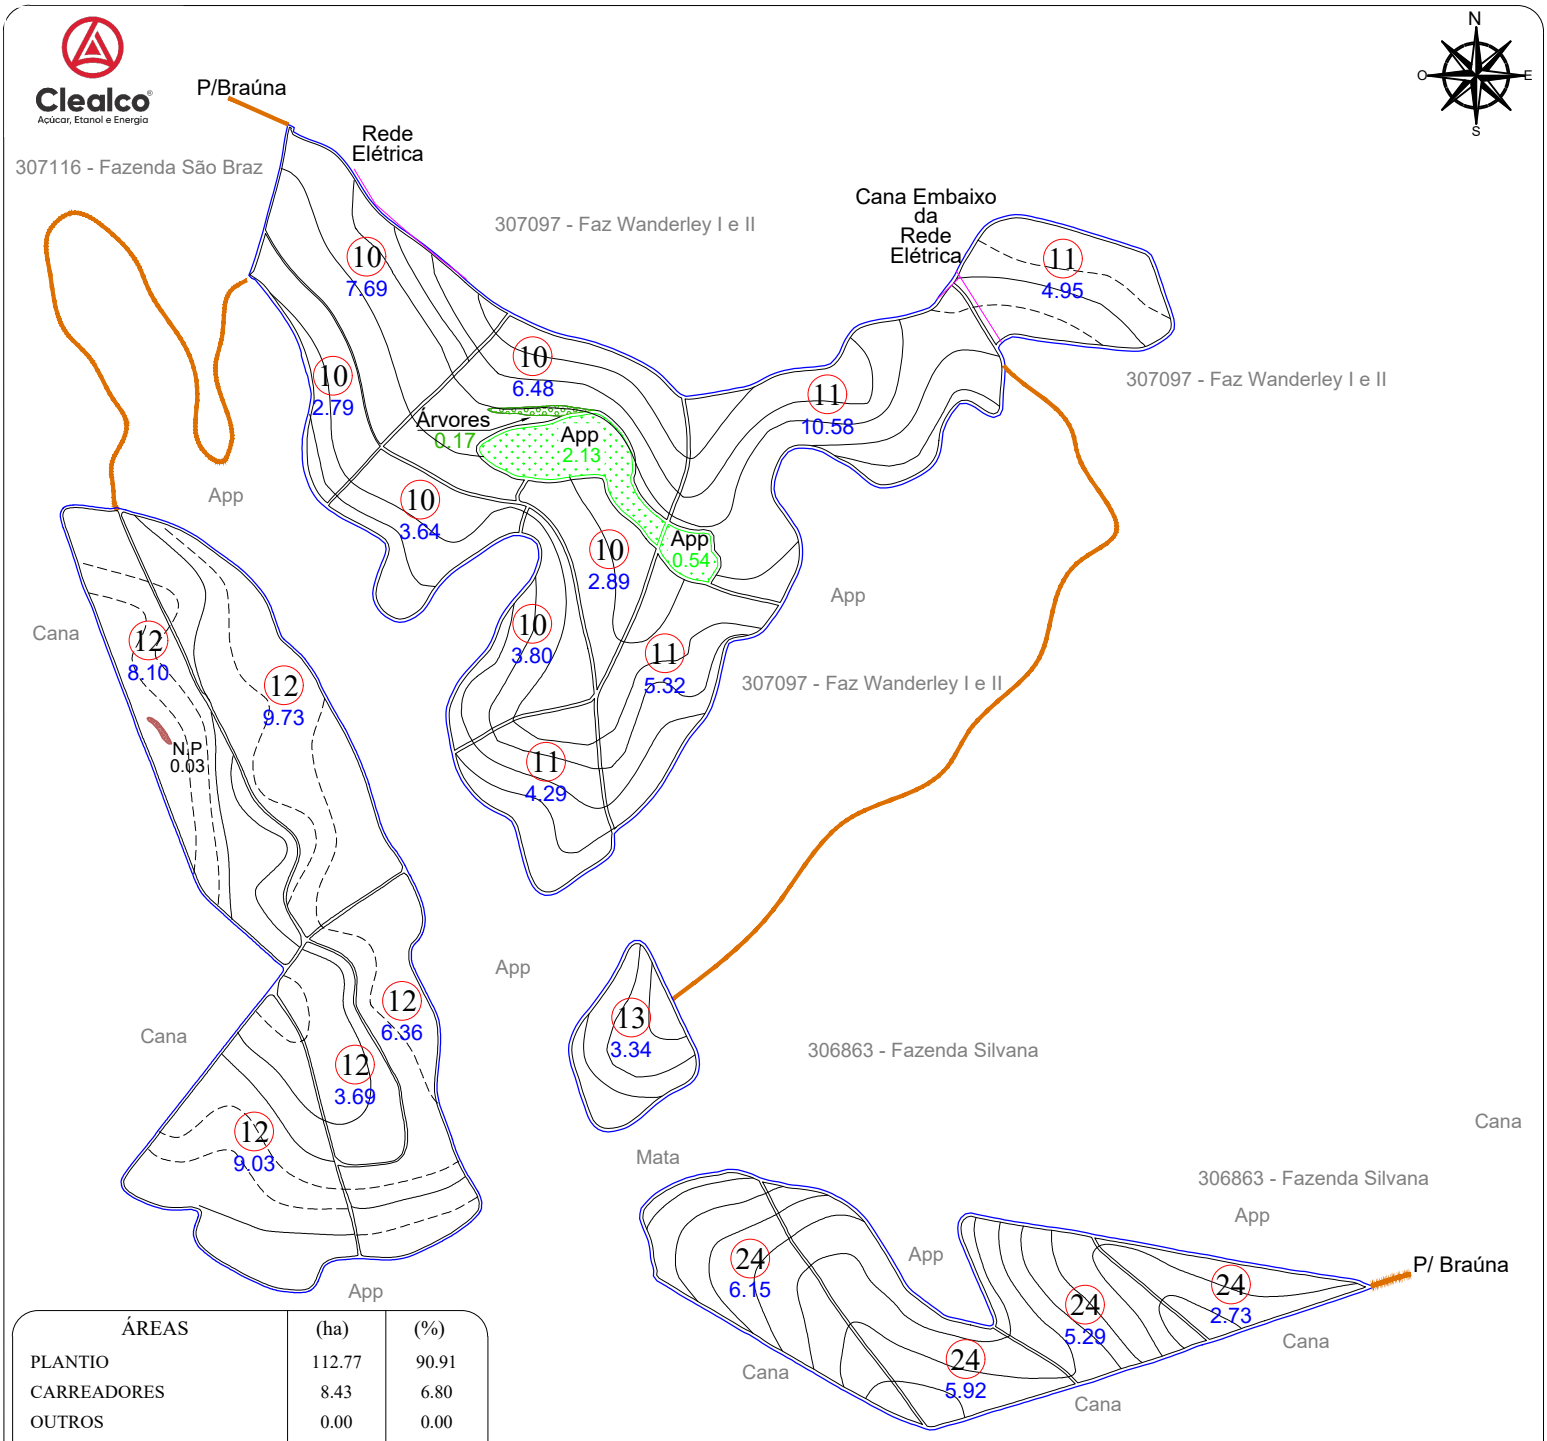


ÁREAS	(ha)	(%)
PLANTIO	112.77	90.91
CARREADORES	8.43	6.80
OUTROS	0.00	0.00
SUB TOTAL AGRICULTÁVEL	121.20	97.71
AP.P.	2.67	2.15
ÁRVORES	0.17	0.14
OUTROS	0.00	0.00
SUB TOTAL NÃO AGRICULT.	2.84	2.29
ÁREA TOTAL	124.04	100.00

C. NÍVEL: 16431.23 m/l 3.78 ha 3.05 %

LEGENDA

- FAZENDA
- TALHÃO
- REDE ELÉTRICA
- TERRAÇO BASE LARGA
- TERRAÇO EMBUTIDO
- (P.O.A) PATIO DE OPERAÇÃO


ESPAÇAMENTO: 1.50 x 1.50
TIRO MÉDIO ESTIMADO: 000.00 m
D.V: 0.00 %

(N.P)-NÃO PLANTOU	
TALHÃO	(ha)
12	0.03
Total	0.03

Nº TAL.	DATA PL.	ÁREA (ha)	VARIEDADE
10	04/2021	27.29	RB96 6928
11		25.14	
12	04/2026	36.91	RB05 5464
13	04/2021	3.34	RB96 6928
24	05/2020	20.09	CTC 04
TOTAL PLANTIO		112.77	

ESCALA: 1: 12.000

CROQUI DE ACESSO

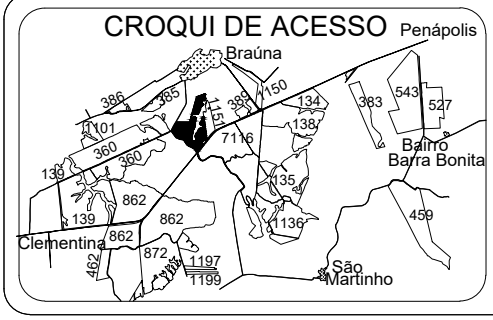

FAZENDA SÃO BRAZ

PROPRIETÁRIO: FERNANDO BOUGO AVELHAN
COMPRADOR: CLEALCO
MUNICÍPIO: BRAÚNA - SP

DISTÂNCIAS (km):
UNID. I - Asfalto: 18.50 Terra.: 2.00
UNID.I I - Asfalto: 75.00 Terra.: 0.00

COORDENADAS: E(X): 569747.70 N(Y): 7619831.84
LAT: -21°31'22.3607" LONG: -50°19'35.4994"
CLEALCO - AÇÚCAR E ALCOOL S/A - DEPARTAMENTO DE GEOTECNOLOGIA

LEVANTAMENTO VIA:
- SATÉLITE
- GPS / VANT
- GOOGLE

UNIDADE: I
PARTE: B/C
FUNDO AGRÍCOLA: 307116

M:\01-Mapa de safra\Mapas Atualizados\Terceiro\307116 - Fazenda São Braz (Fernando Bougo Avelhan)\307116 B - Fazenda São Braz (Fernando Bougo Avelhan).dwg

Bruno Gamboa 27/08/26