

Clealco
Açúcar, Etanol e Energia

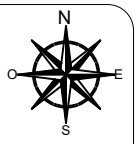

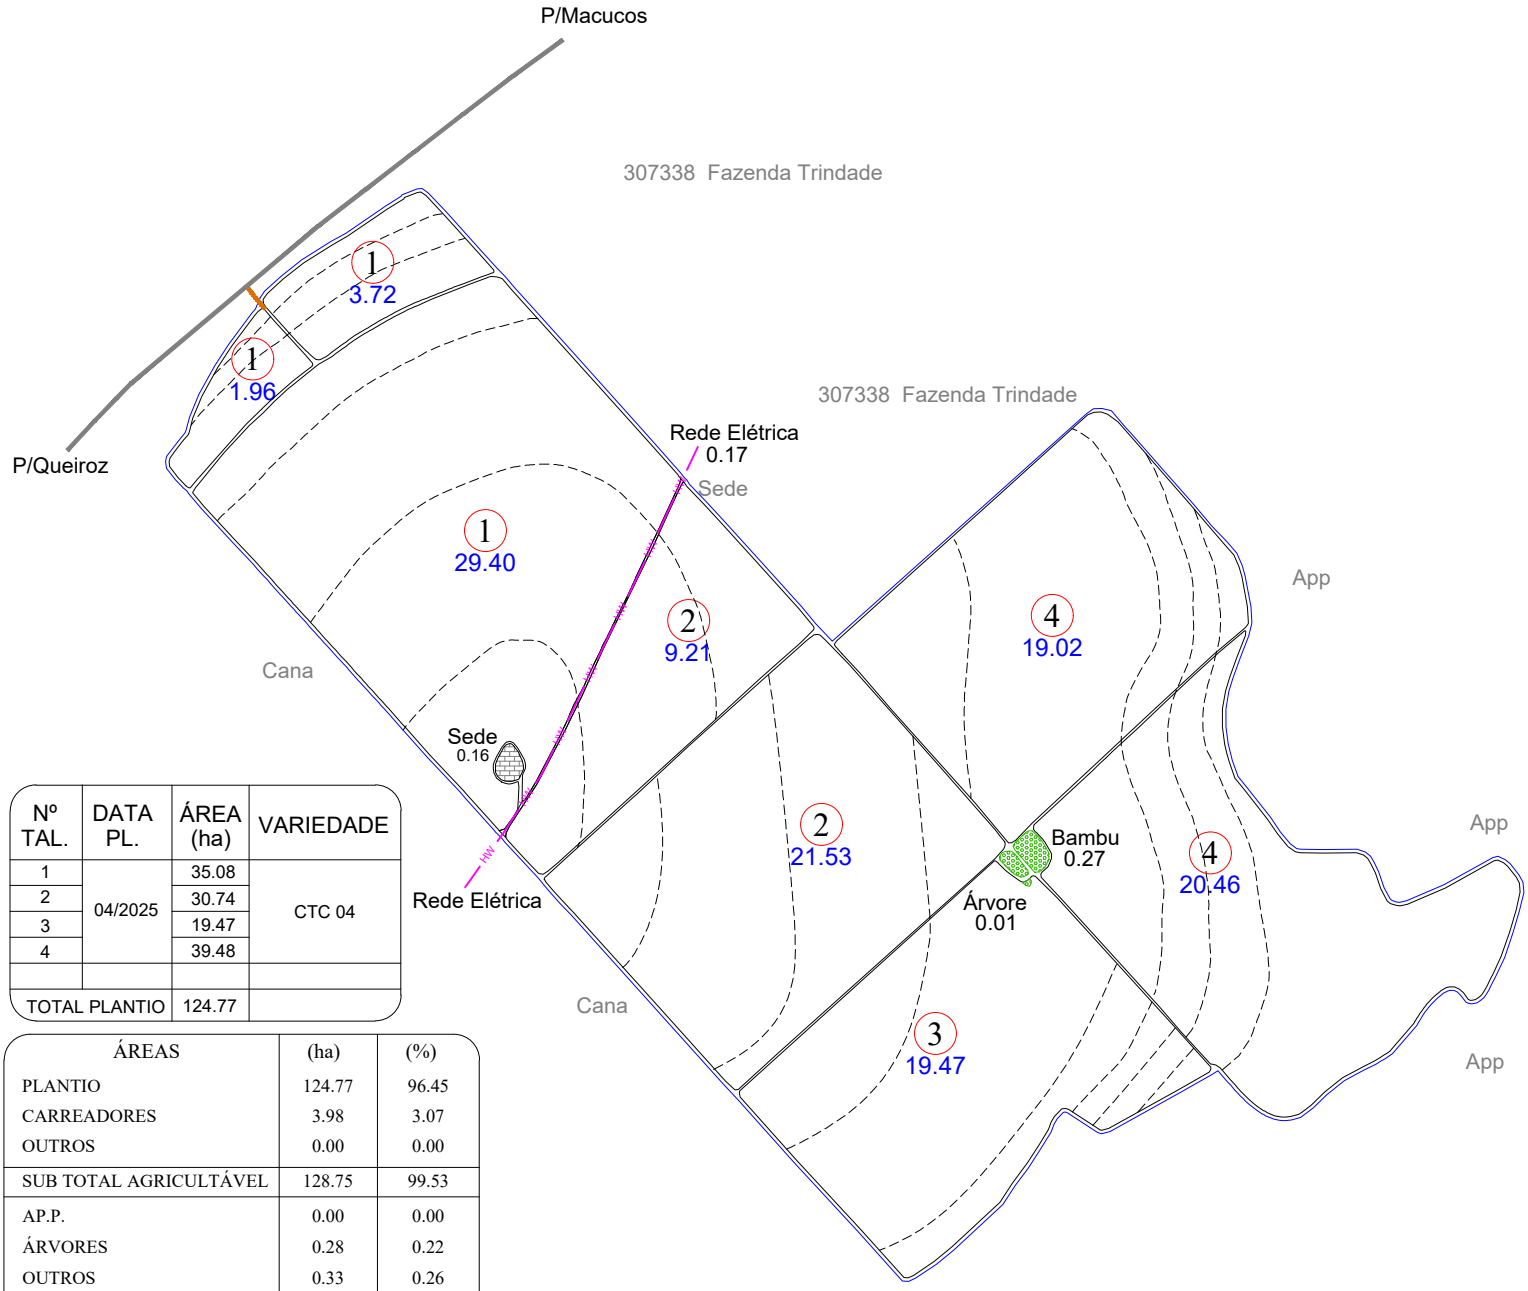

Nº TAL.	DATA PL.	ÁREA (ha)	VARIEDADE
1	04/2025	35.08	CTC 04
2		30.74	
3		19.47	
4		39.48	
TOTAL PLANTIO		124.77	

ÁREAS	(ha)	(%)
PLANTIO	124.77	96.45
CARREADORES	3.98	3.07
OUTROS	0.00	0.00
SUB TOTAL AGRICULTÁVEL	128.75	99.53
AP.P.	0.00	0.00
ÁRVORES	0.28	0.22
OUTROS	0.33	0.26
SUB TOTAL NÃO AGRICULT.	0.61	0.47
ÁREA TOTAL	129.36	100.00

C. NÍVEL: 0.00 m/l 0.00 ha 0.00 %


LEGENDA

- FAZENDA
- TALHÃO
- REDE ELÉTRICA
- TERRAÇO BASE LARGA
- TERRAÇO EMBUTIDO
- (P.O.A) PATIO DE OPERAÇÃO

ESPAÇAMENTO: 1.50 x 1.50
TIRO MÉDIO ESTIMADO: 330.57 m
D.V: 5.28 %

ESCALA: 1: 11.000

CROQUI DE ACESSO

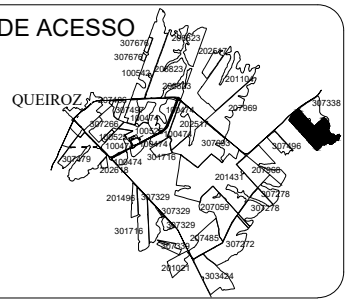

SÍTIO SÃO MANOEL

PROPRIETÁRIO: FRANCISCO GARCIA SOLER FILHO
COMPRADOR: CLEALCO
MUNICÍPIO: QUEIROZ - SP

DISTÂNCIAS (km):
UNID. I - Asfalto: 62.00 Terra.: 0.50
UNID.I I - Asfalto: 9.00 Terra.: 0.50

COORDENADAS: E(X): 587443.21 N(Y): 7588655.73
LAT: -21°48'13.4803" LONG: -50°9'14.5247"

CLEALCO - AÇÚCAR E ALCOOL S/A - DEPARTAMENTO DE GEOTECNOLOGIA

LEVANTAMENTO VIA:
- SATÉLITE
- GPS / VANT
- GOOGLE

UNIDADE: II
PARTE: A/A
FUNDO AGRÍCOLA: 307119

M:\01-Mapa de safra\Mapas Atualizados\Terceiro\307119 - Sítio São Manoel (Francisco Garcia Soler Filho)\307119 - Sítio São Manoel (Francisco Garcia Soler Filho).dwg

Bruno Gamboa 16/12/25