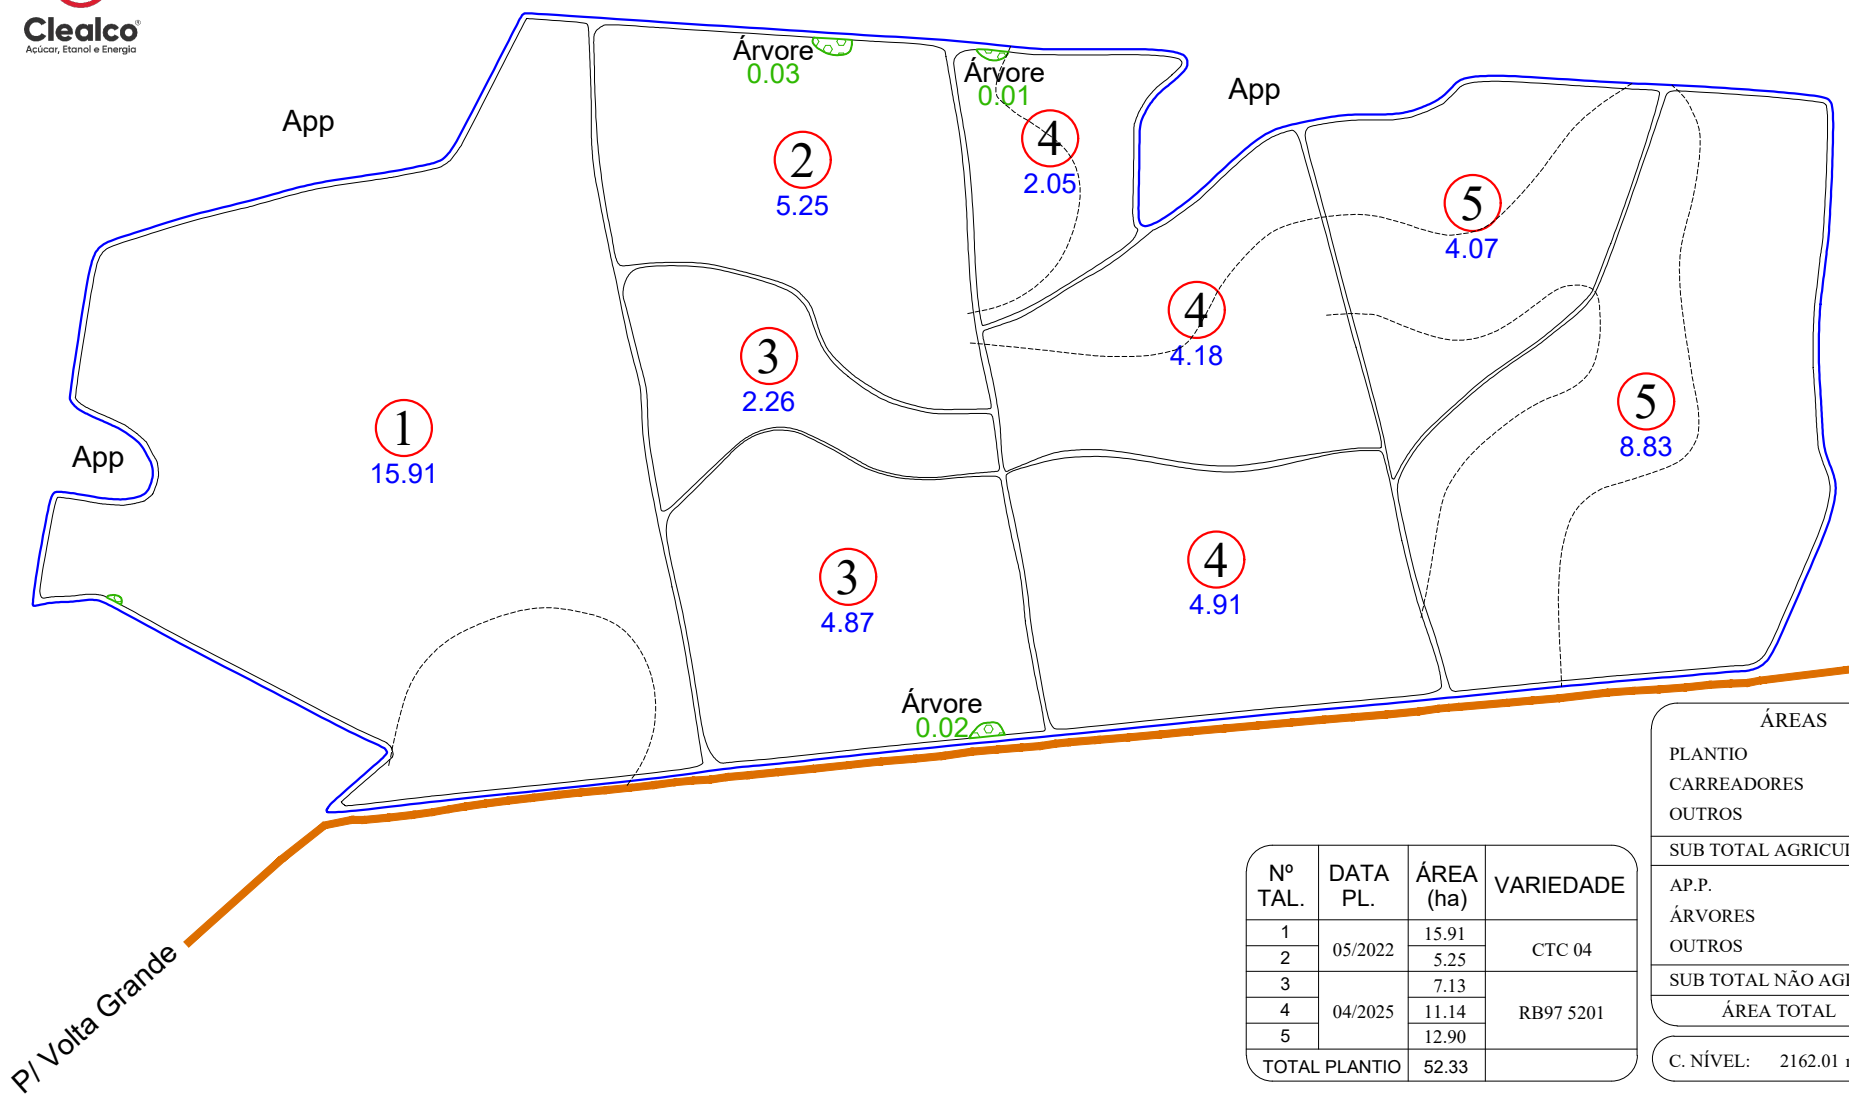


Nº TAL.	DATA PL.	ÁREA (ha)	VARIEDADE
1	05/2022	15.91	CTC 04
2		5.25	
3	04/2025	7.13	RB97 5201
4		11.14	
5		12.90	
TOTAL PLANTIO		52.33	

ÁREAS	(ha)	(%)
PLANTIO	21.16	38.61
CARREADORES	2.42	4.41
OUTROS	31.17	56.87
SUB TOTAL AGRICULTÁVEL	54.75	99.89
AP.P.	0.00	0.00
ÁRVORES	0.06	0.11
OUTROS	0.00	0.00
SUB TOTAL NÃO AGRICULT.	0.06	0.11
ÁREA TOTAL	54.81	100.00

C. NÍVEL:	2162.01 m/l	0.50 ha	0.91 %


ESCALA: 1: 5.500

LEGENDA

- FAZENDA
- TALHÃO
- REDE ELÉTRICA
- TERRAÇO BASE LARGA
- TERRAÇO EMBUTIDO

ESPAÇAMENTO:	1.50 x 1.50	D.V: 3.61 %
TIRO MÉDIO ESTIMADO:	000.00 m	

CROQUI DE ACESSO

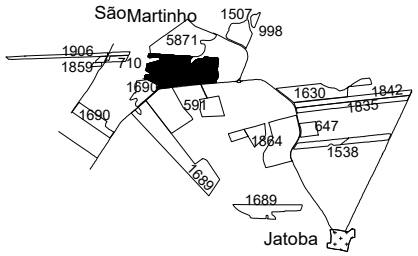

ESTÂCIA ICERI

PROPRIETÁRIO: WILLIAN AVILA PEREIRA
COMPRADOR: CLEALCO
MUNICÍPIO: ALTO ALEGRE - SP

DISTÂNCIAS (km):
UNID. I - Asfalto: 46.50 Terra.: 0.00
UNID.I I - Asfalto: 33.00 Terra.: 0.40

COORDENADAS: E(X): 575715.15 N(Y): 7611409.01
LAT: -21°35'55.4281" LONG: -50°16'6.7037"

CLEALCO - AÇÚCAR E ALCOOL S/A - DEPARTAMENTO DE GEOTECNOLOGIA

LEVANTAMENTO VIA:
- SATÉLITE
- GPS / VANT
- GOOGLE

UNIDADE: II

PARTE: A/A

FUNDO AGRÍCOLA: 307120

M:\01-Mapa de safra\Mapas Atualizados\Terceiro\307120 - Estância Iceri (Willian Avila Pereira)\307120 - Estância Iceri (Willian Avila Pereira).dwg

Bruno Gamboa 24/07/25