D.V.	Nº TAL.	DATA PL.	ÁREA (ha)	VARIEDADE
5.05 %	2	04/2024	2.71	RB966928
	3		23.10	
TOTAL PLANTIO			25.81	

ÁREAS	(ha)	(%)
PLANTIO	25.81	94.70
CARREADORES	1.20	4.39
OUTROS	0.00	0.00
SUB TOTAL AGRICULTÁVEL	27.01	99.08
AP.P.	0.00	0.00
ÁRVORES	0.06	0.22
OUTROS	0.19	0.70
SUB TOTAL NÃO AGRICULT.	0.25	0.92
ÁREA TOTAL	27.26	100.00


C. NÍVEL: 3716.59 m/l 0.85 ha 3.14 %

LEGENDA


- FAZENDA
- TALHÃO
- REDE ELÉTRICA
- TERRAÇO BASE LARGA
- TERRAÇO EMBUTIDO

ESPAÇAMENTO: 1.50 x 1.50

TIRO MÉDIO ESTIMADO: 146.13 m

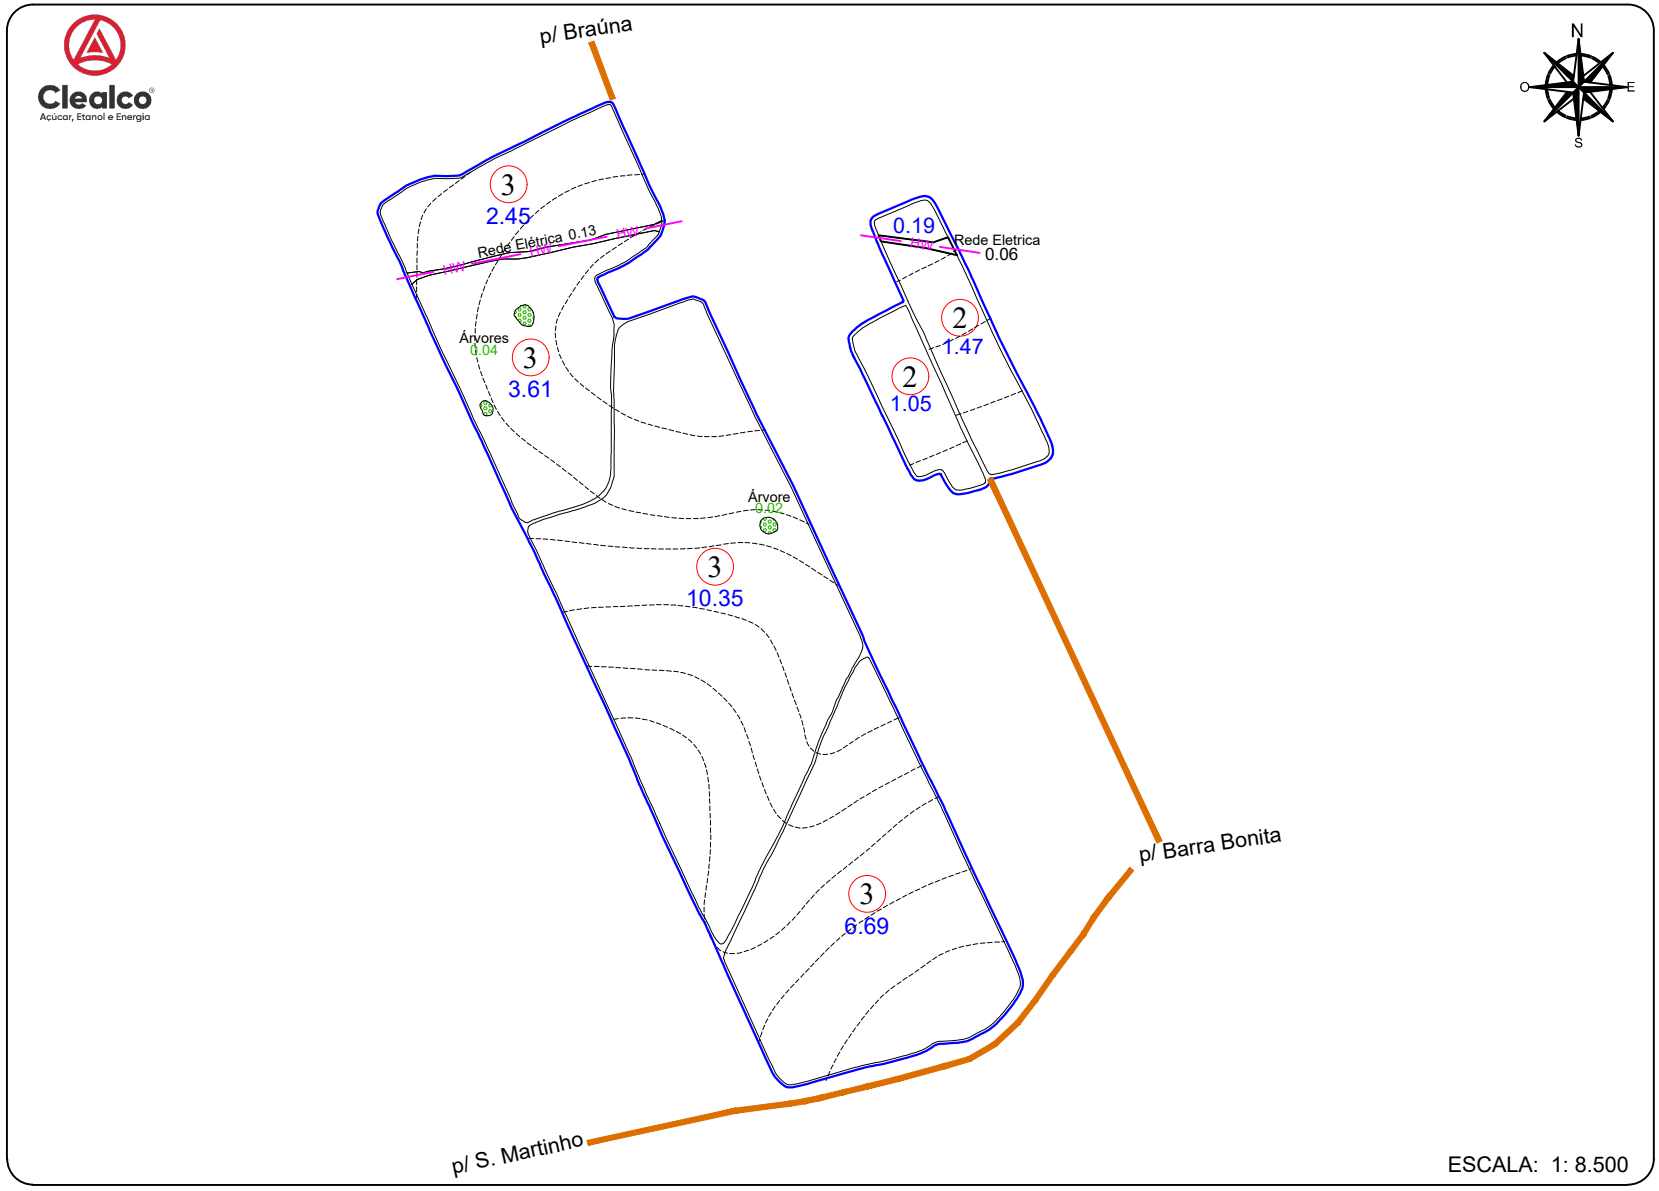

CROQUI DE ACESSO

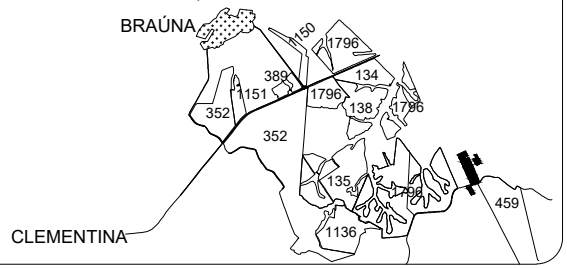

SITIO BARRA BONITA

PROPRIETÁRIO: CARLOS SUSUMO NAKAMURA
COMPRADOR: CLEALCO S/A
MUNICÍPIO: PENÁPOLIS - SP

DISTÂNCIAS (km):
UNIDADE I - 33.00
UNIDADE I I - 43.00

COORDENADAS: E(X): 577653.96 N(Y): 7618107.46
LAT: -21°32'17.2720" LONG: -50°15'0.3989"

CLEALCO - AÇÚCAR E ALCOOL S/A - DEPARTAMENTO DE GEOTECNOLOGIA

UNIDADE: I

PARTE: B/B

FUNDO AGRÍCOLA: 307142