ZONA	Nº TAL.	DATA PL.	ÁREA (ha)	VAR.
999 5.52%	1	06/2021	26.74	CTC 04 RB 97 5242 RB 97 5201
	2		10.79	
	3		9.51	
	4		9.84	
	5		27.44	
	6		26.12	
TOTAL PLANTIO			110.44	--------


ÁREAS	(ha)	(%)
PLANTIO	110.44	94.80
CARREADORES	5.02	4.31
OUTROS	0.00	0.00
SUB TOTAL AGRICULTÁVEL	115.46	99.11
AP.P.	0.00	0.00
MATA	0.00	0.00
OUTROS	1.04	0.89
SUB TOTAL NÃO AGRICULT.	1.04	0.89
ÁREA TOTAL	116.50	100.00

C. NÍVEL: 11342.79 m/l 2.61 ha 2.36 %

LEGENDA

- FAZENDA
- TALHÃO
- CURVA DE NÍVEL
- CARREADOR
- CONFRONTANTE
- REDE ELÉTRICA
- TRAJETO VAZIO
- TRAJETO CARREGADO


PLANTIO MANUAL - ESPAÇAMENTO: 1.40 X 1.40
TIRO MÉDIO ESTIMADO: 391.15 m

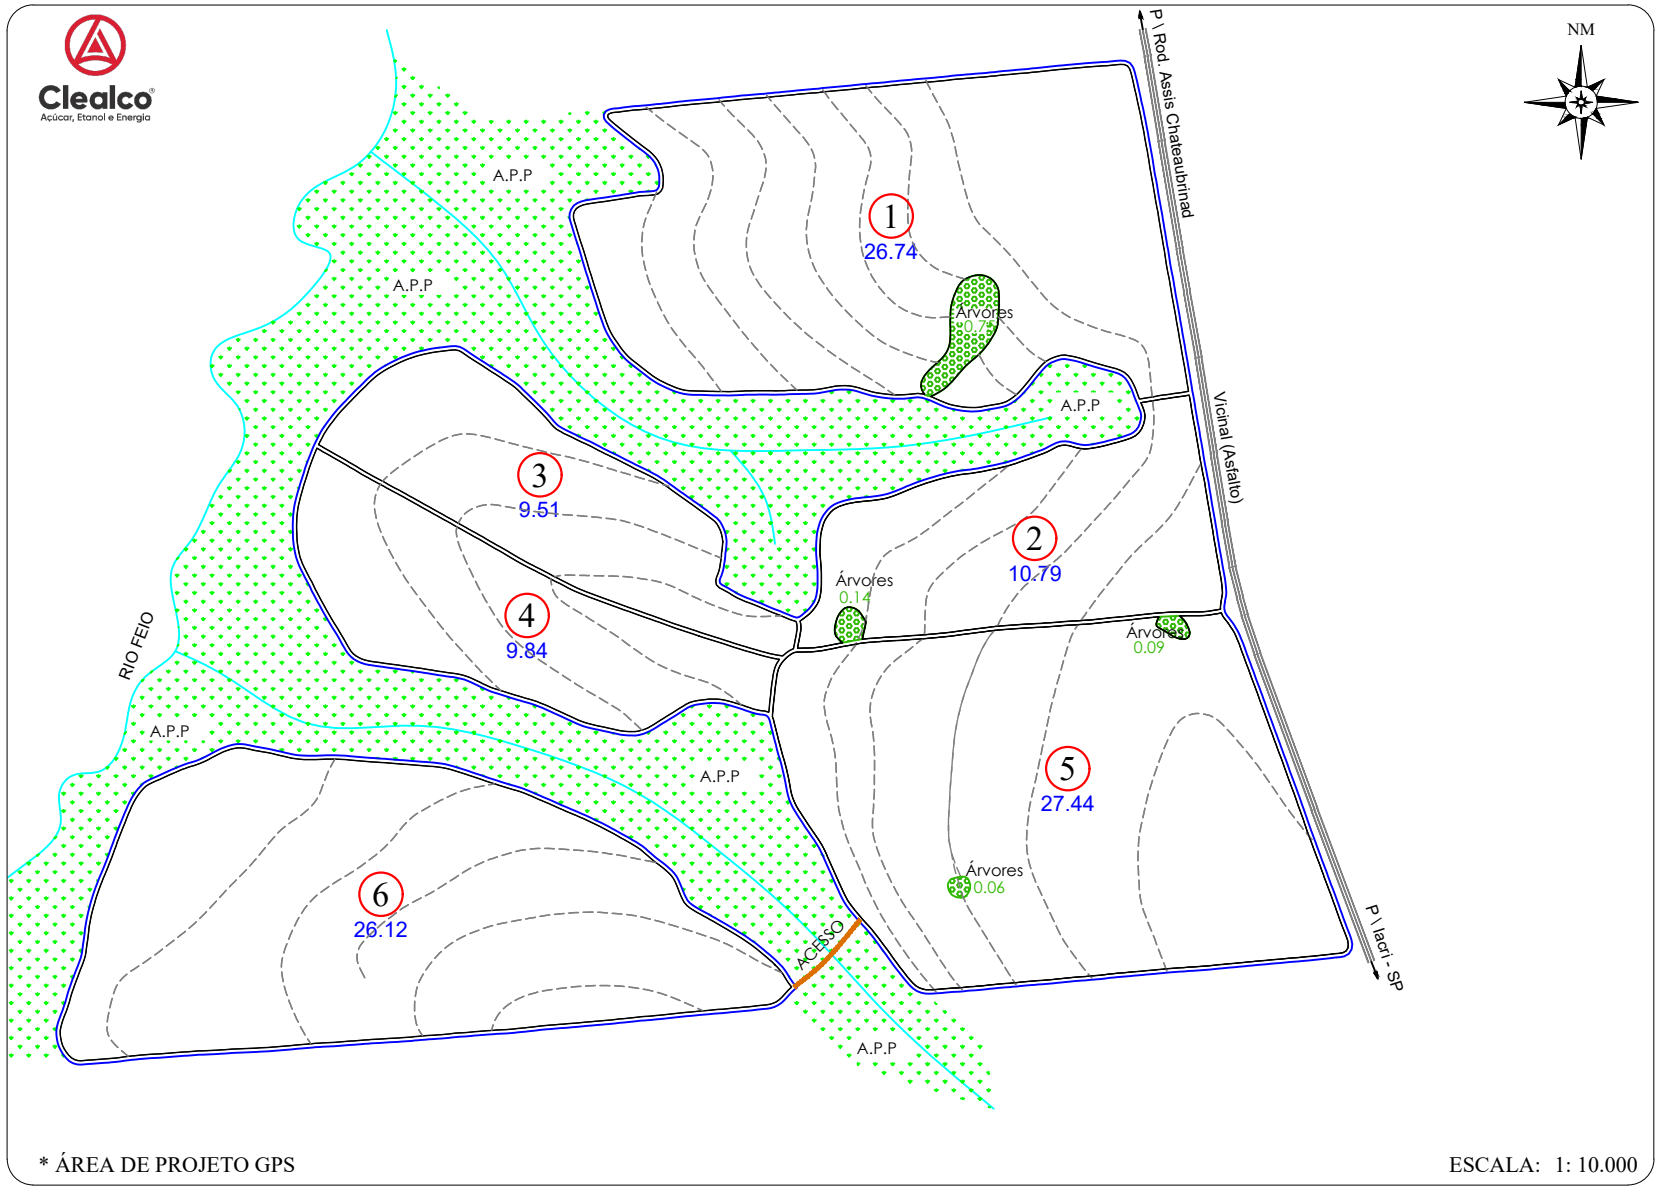

* ÁREA DE PROJETO GPS

ESCALA: 1: 10.000

CROQUI DE ACESSO

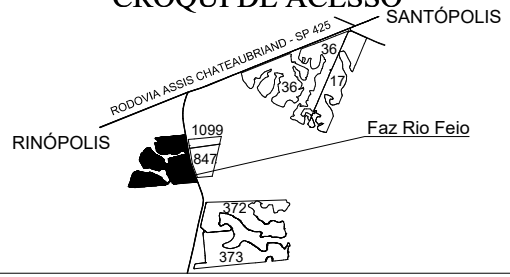

FAZENDA RIO FEIO

PROPRIETÁRIO: VILMAR JOSÉ GASTALDI
COMPRADOR: CLEALCO S/A
MUNICÍPIO: SANTÓPOLIS DO AGUAPEÍ

DISTÂNCIAS (km):
UNID. I - Asfalto: 25.00 Terra.: 1.00
UNID.I I - Asfalto: 59.00 Terra.: 1.00
UNID. III -Asfalto: 67.00 Terra.: 1.00

COORDENADAS: E(X): 541.169,47 N(Y): N: N: 7.600.812,70
LAT: 21°41'44" LONG: 50°36'07"

CLEALCO - AÇÚCAR E ALCOOL S/A - DEPARTAMENTO DE TOPOGRAFIA

UNIDADE: I
PARTE: A/A
FUNDO AGRÍCOLA: 307201