ZONA DV	Nº TAL.	DATA PL.	ÁREA (ha)	VARIEDADE
999 4.89%	1	04/2021	6.20	RB 975201
	2		15.88	
	3		10.87	CV 7870
TOTAL PLANTIO			32.95	--------


ÁREAS	(ha)	(%)
PLANTIO	32.95	92.25
CARREADORES	2.77	7.75
OUTROS	0.00	0.00
SUB TOTAL AGRICULTÁVEL	35.72	100.00
AP.P.	0.00	0.00
ÁRVORES	0.00	0.00
OUTROS	0.00	0.00
SUB TOTAL NÃO AGRICULT.	0.00	0.00
ÁREA TOTAL	35.72	100.00

C. NÍVEL: 2543.26 m/l 0.58 ha 1.64 %


LEGENDA

- FAZENDA
- TALHÃO
- CURVA DE NÍVEL
- CARREADOR
- CONFRONTANTE
- REDE ELÉTRICA
- TRAJETO VAZIO
- TRAJETO CARREGADO

PLANTIO MANUAL - ESPAÇAMENTO: 1.50 X 1.50
TIRO MÉDIO ESTIMADO: 209.63 m

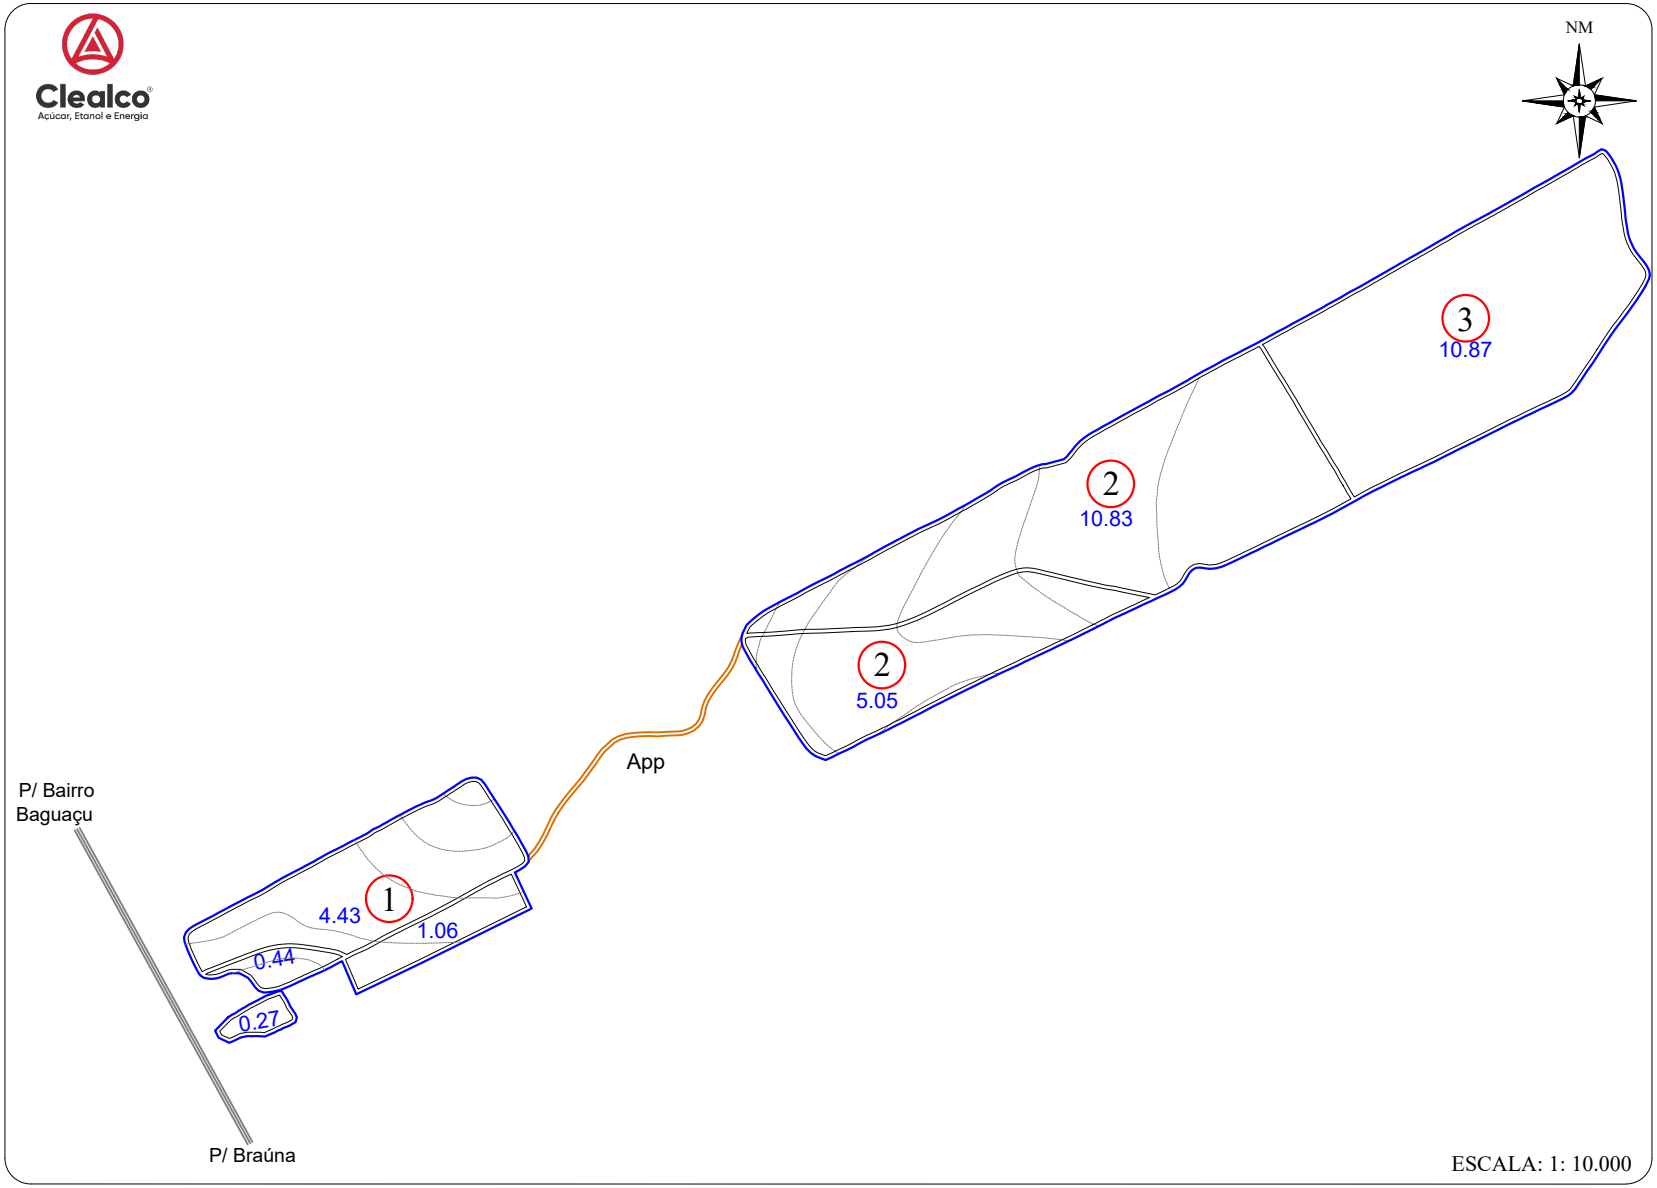

CROQUI DE ACESSO

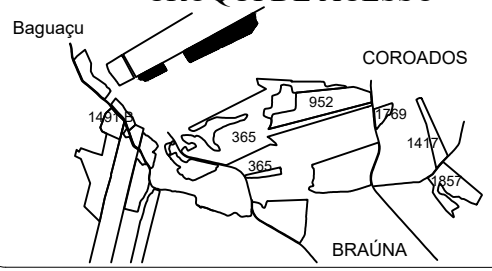

SÍTIO PRIMAVERA

PROPRIETÁRIO: THIAGO TUNES DOS SANTOS
COMPRADOR: CLEALCO S/A
MUNICÍPIO: COROADOS

DISTÂNCIAS (km):
UNID. I - Asfalto: 27.00 Terra.: 0.50
UNID.I I - Asfalto: 75.00 Terra.: 0.50
UNID. III -Asfalto: 69.00 Terra.: 0.50

COORDENADAS: E(X): 567966.23 N(Y): 7627223.62
LAT: -21°27'22.1948" LONG: -50°20'38.4998"

CLEALCO - AÇÚCAR E ALCOOL S/A - DEPARTAMENTO DE TOPOGRAFIA

UNIDADE: I
PARTE: A/A
FUNDO AGRÍCOLA: 307203

M:\01-Mapa de safra\Mapas Atualizados\Terceiro\307203 - Sítio Primavera (Thiago Tunes dos Santos)\307203 - Sítio Primavera (Thiago Tunes dos Santos).dwg

Bruno Gamboa 14/05/24