ZONA DV	Nº TAL.	DATA PL.	ÁREA (ha)	VARIEDADE
999 2.50%	1	06/2022	18.88	RB 966928
	2		21.96	
	3		17.84	
TOTAL PLANTIO			58.68	--------


ÁREAS	(ha)	(%)
PLANTIO	58.68	95.63
CARREADORES	1.86	3.03
OUTROS	0.00	0.00
SUB TOTAL AGRICULTÁVEL	60.54	98.66
AP.P.	0.00	0.00
MATA	0.65	1.06
OUTROS	0.17	0.28
SUB TOTAL NÃO AGRICULT.	0.82	1.34
ÁREA TOTAL	61.36	100.00

C. NÍVEL: 7441.90 m/l 1.71 ha 2.79 %


LEGENDA

- FAZENDA
- TALHÃO
- CURVA DE NÍVEL
- CARREADOR
- CONFRONTANTE
- REDE ELÉTRICA
- TRAJETO VAZIO
- TRAJETO CARREGADO

PLANTIO MANUAL - ESPAÇAMENTO: 1.50 X 1.50
TIRO MÉDIO ESTIMADO: 467.79 m

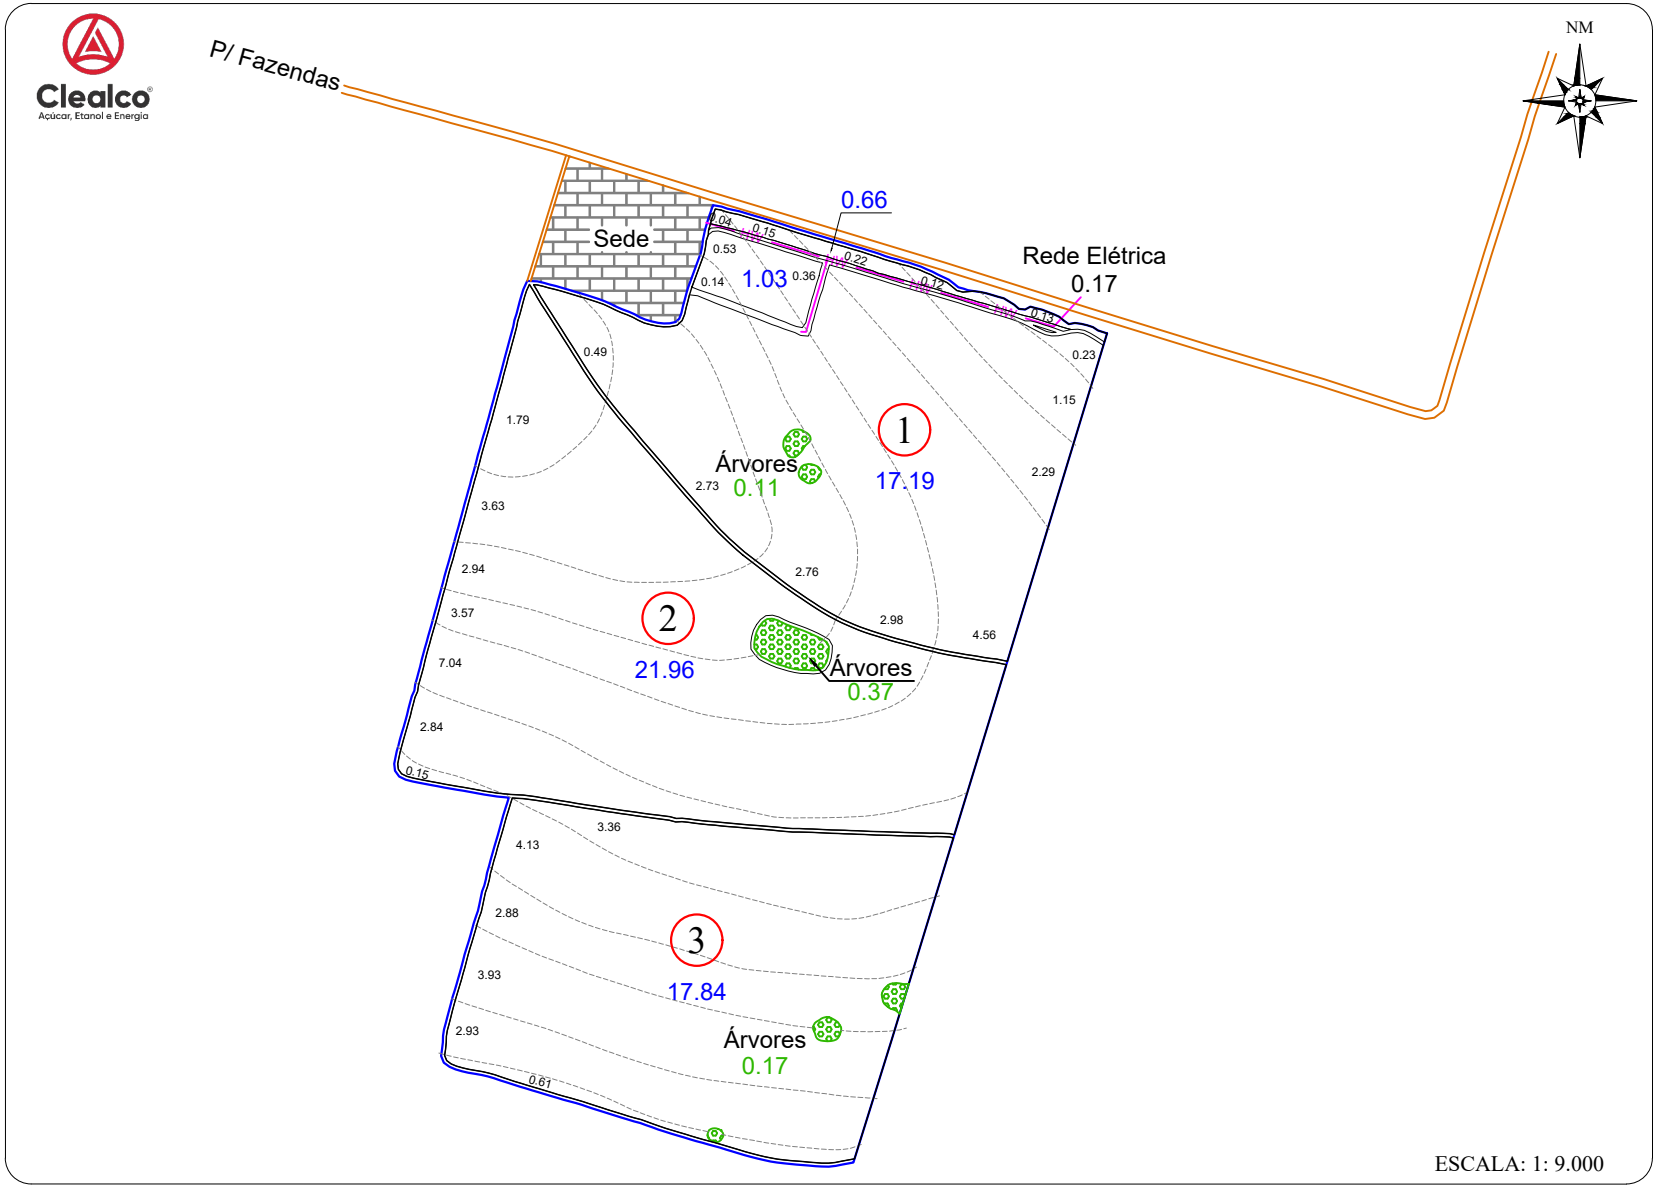

CROQUI DE ACESSO

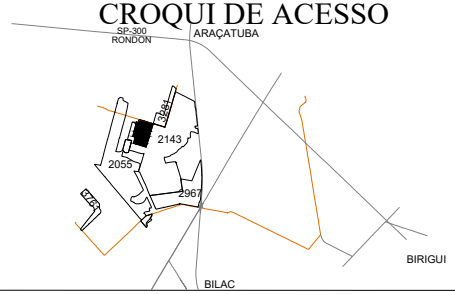

FAZENDA SANTA CLARA DA BELA ESPERANÇA

PROPRIETÁRIO: FERNANDO MOIMAZ
ARRENDATÁRIO: CLEALCO S/A
MUNICÍPIO: ARAÇATUBA

DISTÂNCIAS (km):
UNID. I - Asfalto: 35.50 Terra.: 3.00
UNID.I I - Asfalto: 93.50 Terra.: 3.00
UNID. III -Asfalto: 55.00 Terra.: 3.00

COORDENADAS: E(X): 552824.38 N(Y): 7650018.20
LAT: -21°15'2.6185" LONG: -50°29'27.1507"

CLEALCO - AÇÚCAR E ALCOOL S/A - DEPARTAMENTO DE TOPOGRAFIA

UNIDADE: I
PARTE: A/A
FUNDO AGRÍCOLA: 307207

M:\01-Mapa de safra\Mapas Atualizados\Terceiro\307207 - Fazenda Santa Clara da Bela Esperança (Fernando Moimas)\307207 - Fazenda Santa Clara da Bela Esperança (Fernando Moimas).dwg

Fernanda Bezerra 15/08/22