ZONA DV	Nº TAL.	DATA PL.	ÁREA (ha)	VARIEDADE
999 4.83 %	1	06/2022	41.79	RB867515
	2		39.70	
	3		14.19	
TOTAL PLANTIO			95.68	--------


ÁREAS	(ha)	(%)
PLANTIO	95.68	95.79
CARREADORES	4.08	4.08
OUTROS	0.00	0.00
SUB TOTAL AGRICULTÁVEL	99.76	99.87
AP.P.	0.00	0.00
ÁRVORES	0.13	0.13
OUTROS	0.00	0.00
SUB TOTAL NÃO AGRICULT.	0.13	0.13
ÁREA TOTAL	99.89	100.00

C. NÍVEL: 14278.62 m/l 3.28 ha 3.29 %


LEGENDA

- FAZENDA
- TALHÃO
- CURVA DE NÍVEL
- CARREADOR
- CONFRONTANTE
- REDE ELÉTRICA
- TRAJETO VAZIO
- TRAJETO CARREGADO

PLANTIO MANUAL - ESPAÇAMENTO: 1.50 X 1.50
TIRO MÉDIO ESTIMADO: 457.11 m

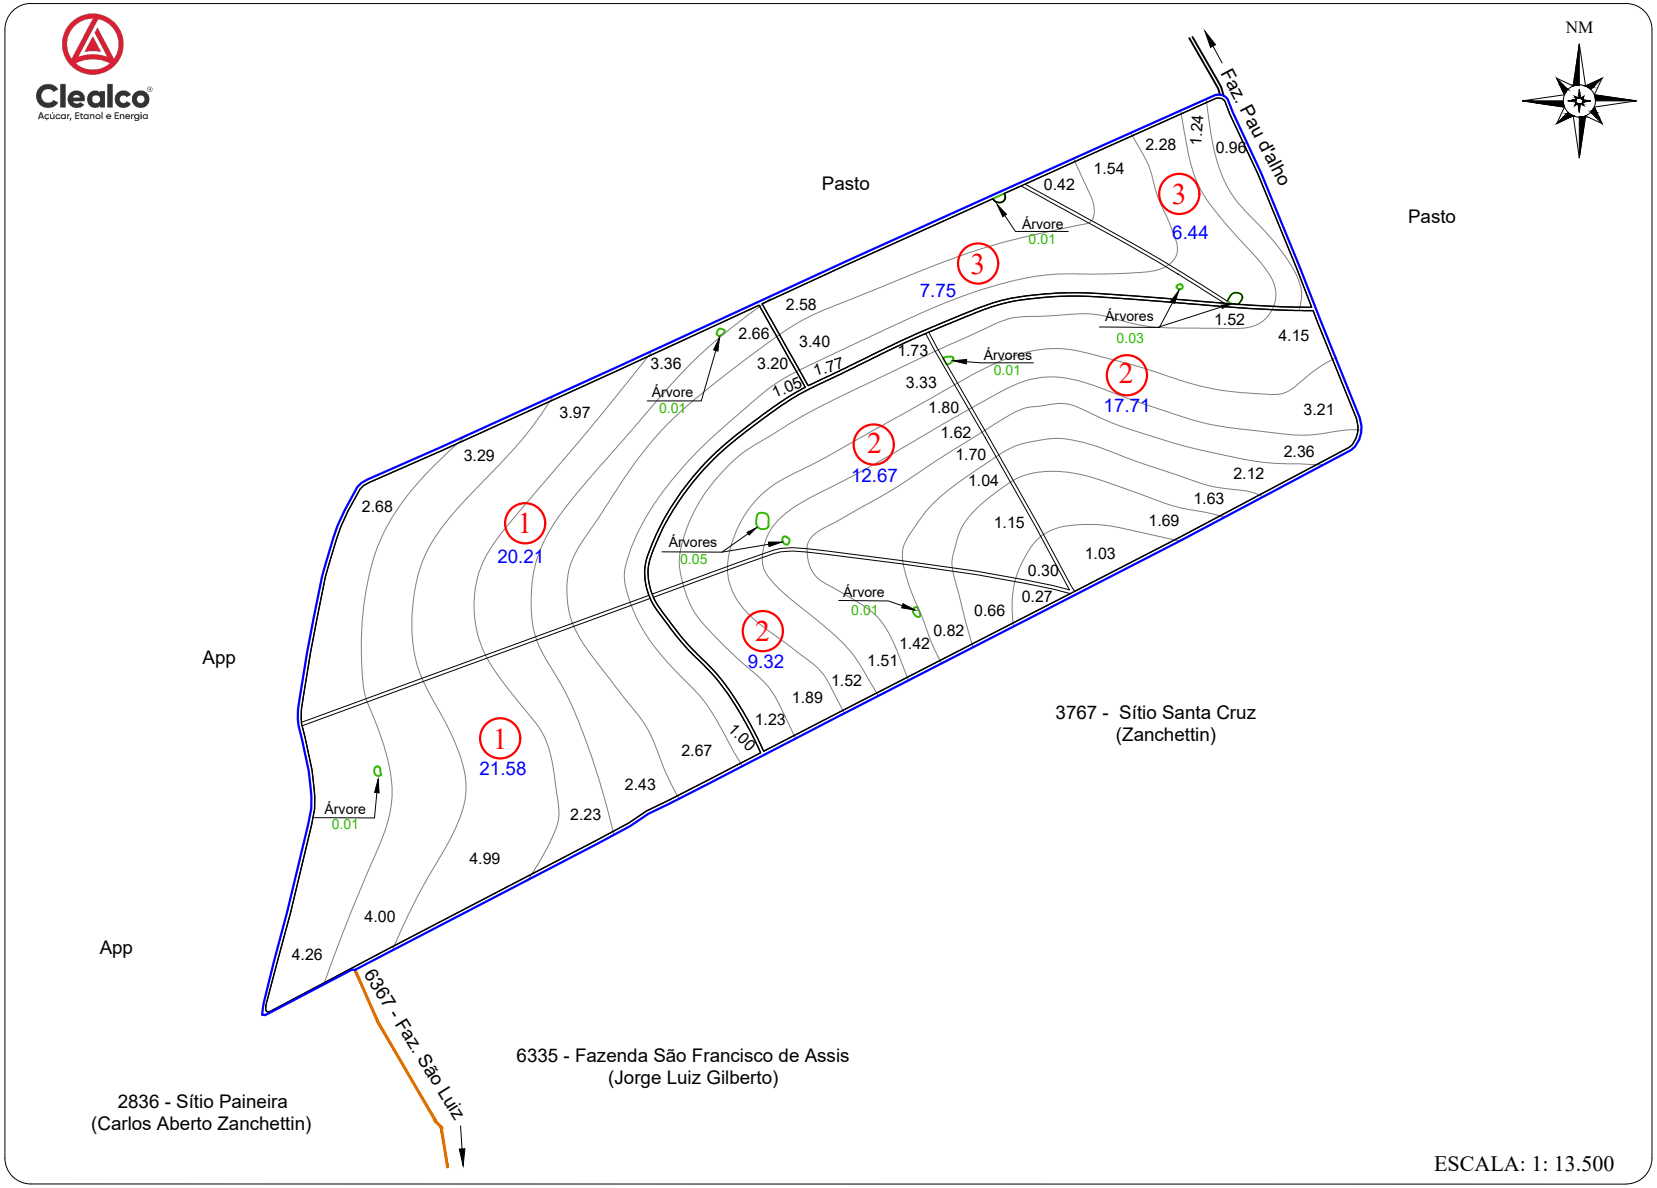

CROQUI DE ACESSO

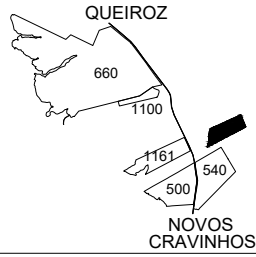

SÍTIO JANGADA

PROPRIETÁRIO: CARLOS ZANCHETTIN
ARRENDATÁRIO: CLEALCO S/A
MUNICÍPIO: POMPÉIA

DISTÂNCIAS (km):
UNID. I - Asfalto: 79.00 Terra.: 2.00
UNID.I I - Asfalto: 18.50 Terra.: 2.00
UNID. III -Asfalto: 71.00 Terra.: 2.00

COORDENADAS: E(X): 590949.3525 N(Y): 7574627.4497
LAT: 21°55'48,78516" LONG: 50°07'09,63973"

CLEALCO - AÇÚCAR E ALCOOL S/A - DEPARTAMENTO DE TOPOGRAFIA

UNIDADE: II
PARTE: A/A
FUNDO AGRÍCOLA: 307212