ZONA D.V.	Nº TAL.	DATA PL.	ÁREA (ha)	VAR.
999 3.57 %	1	04/2022	20.61	RB 975242
	2		28.48	
	3		20.71	
1	4	05/2024	13.07	RB 867515
TOTAL PLANTIO			82.87	--------

ÁREAS	(ha)	(%)
PLANTIO	82.87	96.38
CARREADORES	3.11	3.62
OUTROS	0.00	0.00
SUB TOTAL AGRICULTÁVEL	85.98	100.00
AP.P.	0.00	0.00
ÁRVORES	0.00	0.00
OUTROS	0.00	0.00
SUB TOTAL NÃO AGRICULT.	0.00	0.00
ÁREA TOTAL	85.98	100.00


C. NÍVEL: 6910.04 m/l 1.59 ha 1.85 %

LEGENDA

- FAZENDA
- TALHÃO
- CURVA DE NÍVEL
- CARREADOR
- CONFRONTANTE
- REDE ELÉTRICA
- TRAJETO VAZIO
- TRAJETO CARREGADO


PLANTIO MANUAL - ESPAÇAMENTO: 1.50 X 1.50
TIRO MÉDIO ESTIMADO: 000.00m

Clealco
Açúcar, Etanol e Energia

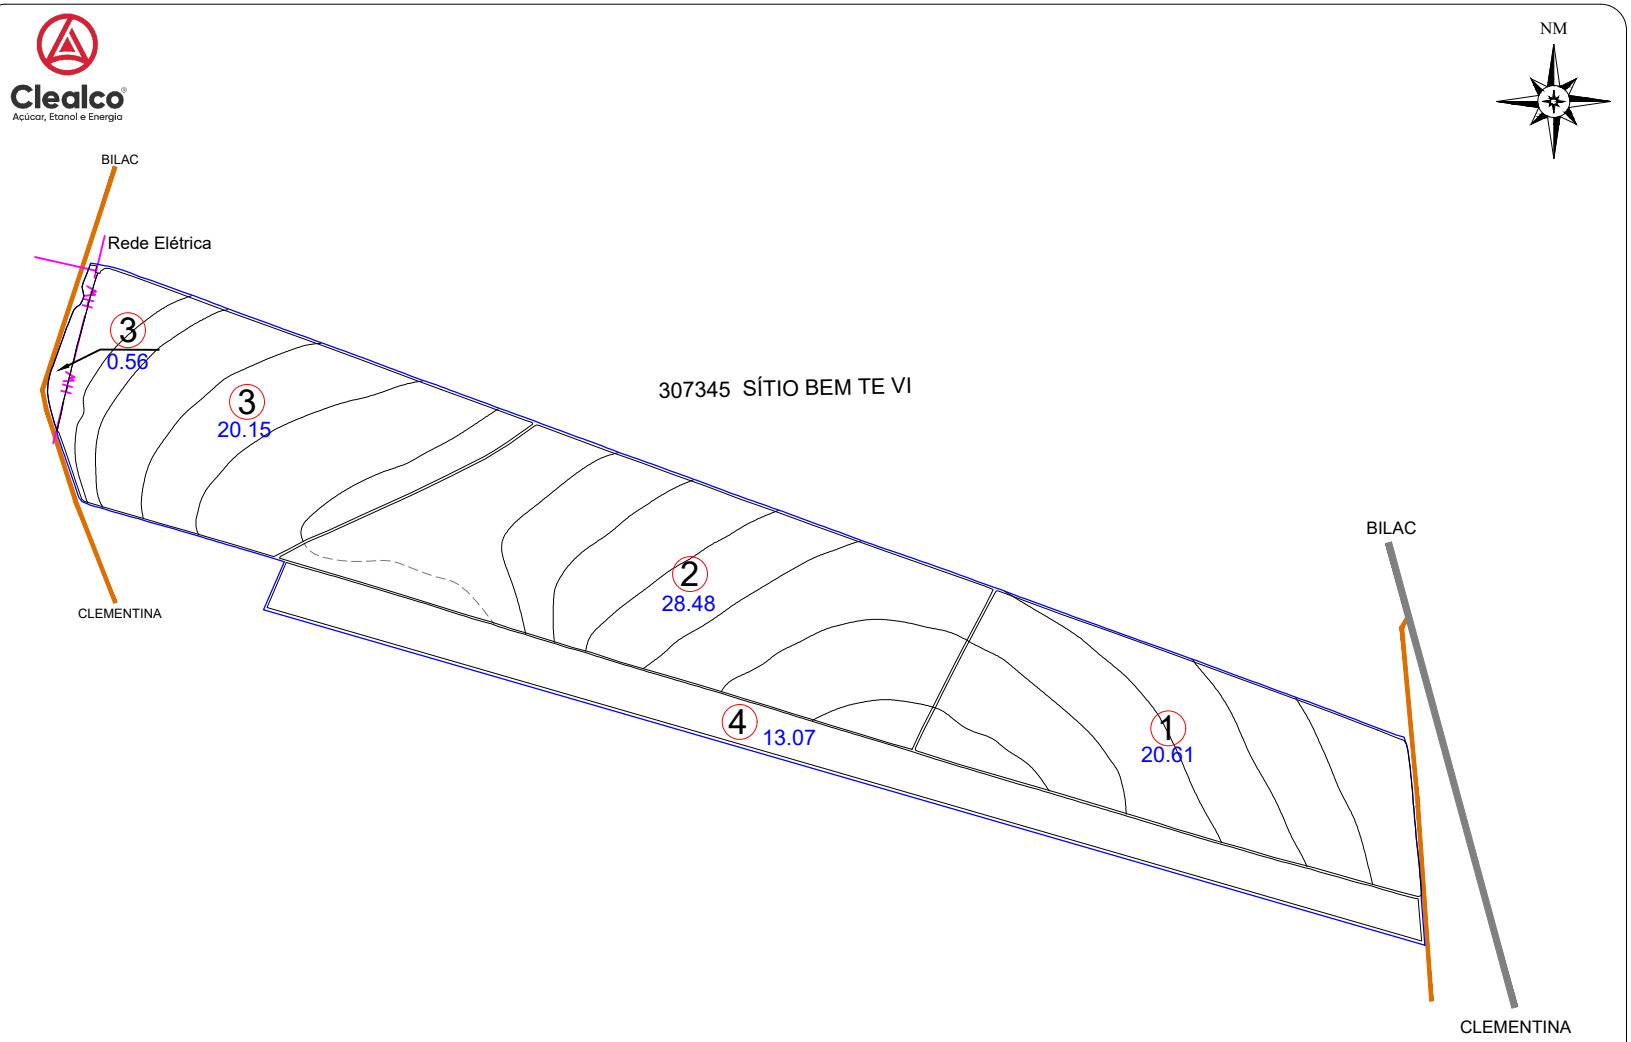

ESCALA: 1: 12.500

CROQUI DE ACESSO

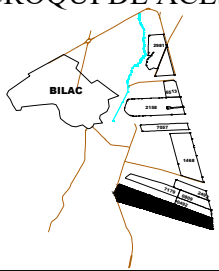

SÍTIO DOIS IRMÃOS

PROPRIETÁRIO: PAULO BENTO BOGO
COMPRADOR: CLEALCO S/A
MUNICÍPIO: BILAC - SP

DISTÂNCIAS (km):
UNID. I - Asfalto: 18.00 Terra.: 0.50
UNID.I I - Asfalto: 75.00 Terra.: 0.50
UNID. III -Asfalto: 59.00 Terra.: 0.50

COORDENADAS: E(X): 556305.59 N(Y): 7630658.09
LAT: -21°25'31.9405" LONG: -50°27'24.0495"

CLEALCO - AÇÚCAR E ALCOOL S/A - DEPARTAMENTO DE TOPOGRAFIA

UNIDADE: I
PARTE: A/A
FUNDO AGRÍCOLA: 307214

M:\01-Mapa de safra\Mapas Atualizados\Terceiro\307214 - Sítio Dois Irmãos (Paulo Bento Bogo)\307214 - Sítio Dois Irmãos (Paulo Bento Bogo).dwg

Bruno Gamboa 17/06/2025