ZONA DV	Nº TAL.	DATA PL.	ÁREA (ha)	VARIEDADE
999 4.63 %	1	04/2022	19.62	RB 867515
	2		40.67	
	3		5.16	
	4		22.61	
TOTAL PLANTIO			88.06	--------

ÁREAS	(ha)	(%)
PLANTIO	88.06	94.64
CARREADORES	4.60	4.94
OUTROS	0.00	0.00
SUB TOTAL AGRICULTÁVEL	92.66	99.58
AP.P.	0.00	0.00
ÁRVORES	0.34	0.37
OUTROS	0.05	0.05
SUB TOTAL NÃO AGRICULT.	0.39	0.42
ÁREA TOTAL	93.05	100.00

C. NÍVEL: 8220.74 m/l 1.89 ha 2.03 %


LEGENDA

- FAZENDA
- TALHÃO
- CURVA DE NÍVEL
- CARREADOR
- CONFRONTANTE
- REDE ELÉTRICA
- TRAJETO VAZIO
- TRAJETO CARREGADO

PLANTIO MANUAL - ESPAÇAMENTO: 1.50 X 1.50
TIRO MÉDIO ESTIMADO: 509.98 m


Clealco
Açúcar, Etanol e Energia

NM

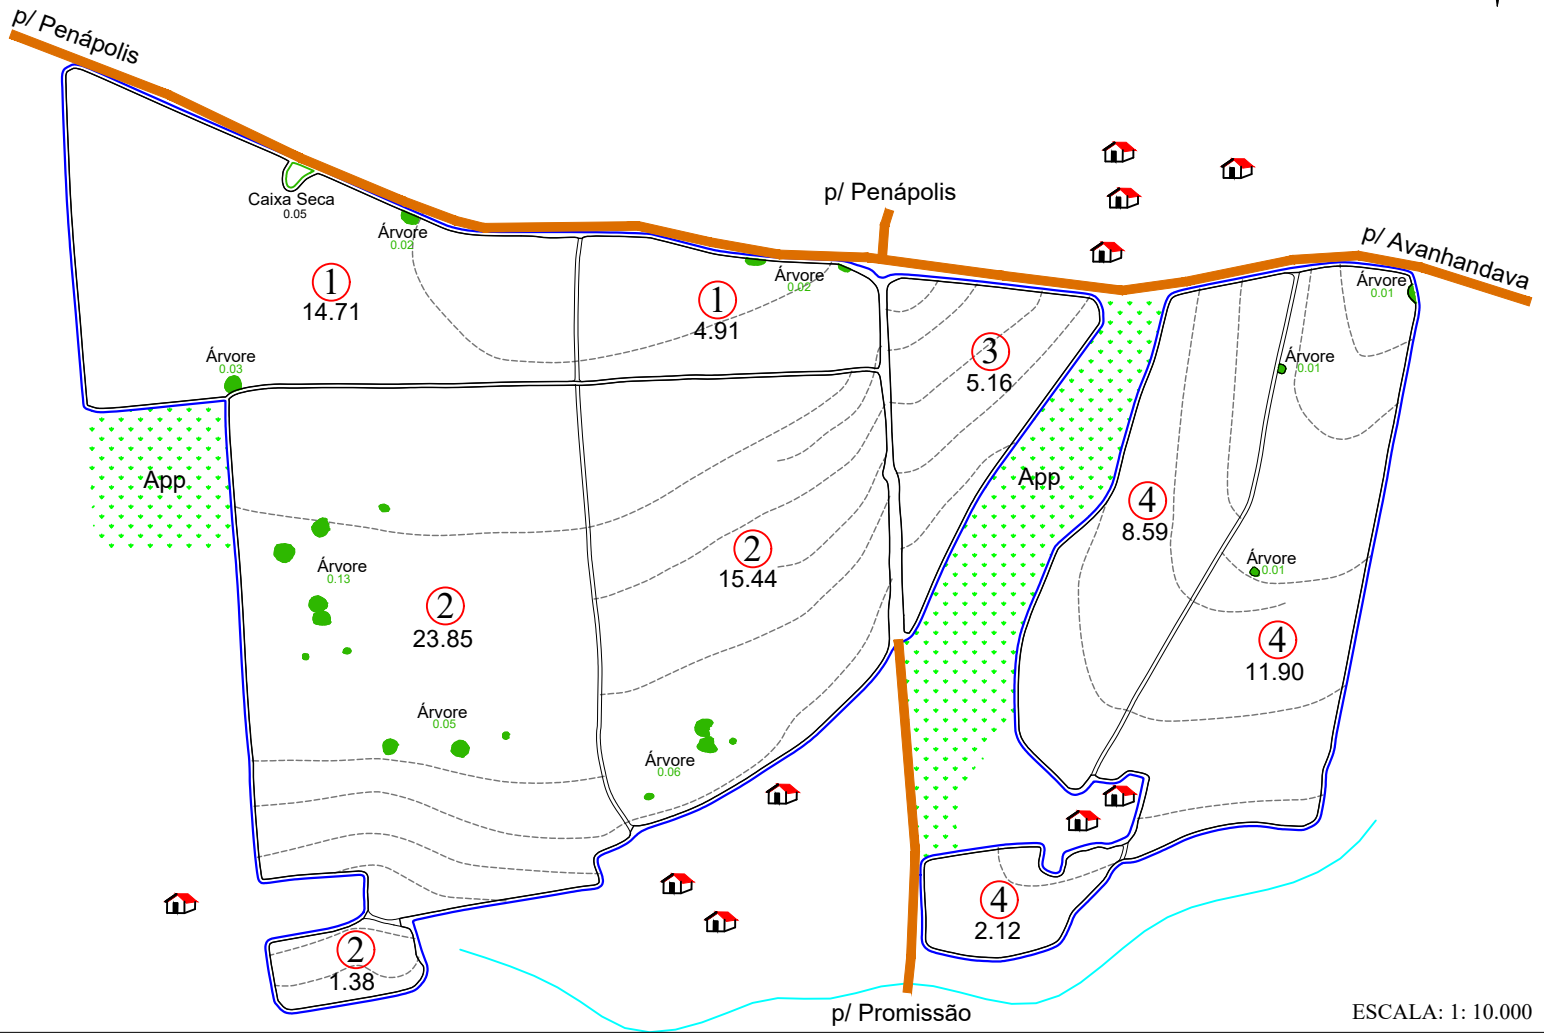

ESCALA: 1: 10.000

CROQUI DE ACESSO

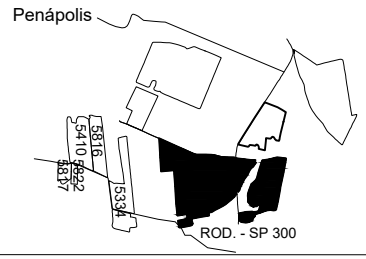

SITIO QUATRO MENINAS

PROPRIETÁRIO: ADENILSON PONTIN
COMPRADOR: CLEALCO S/A
MUNICÍPIO: PENAPOLIS

DISTÂNCIAS (km):
UNID. I - Asfalto: 53.50 Terra.: 5.00
UNID.I I - Asfalto: 67.00 Terra.: 4.30
UNID. III -Asfalto: 13.50 Terra.: 5.30

COORDENADAS: E(X): 600517 N(Y): 7624217
LAT: 21°28'54,48051" LONG: 50°01'46,97243"

CLEALCO - AÇÚCAR E ALCOOL S/A - DEPARTAMENTO DE TOPOGRAFIA

UNIDADE: II
PARTE: A/A
FUNDO AGRÍCOLA: 307218

M:\01-Mapa de safra\Mapas Atualizados\Terceiro\307218 - Sítio Quatro Meninas (Adenilson Pontin)\307218 - Sítio Quatro Meninas (Adenilson Pontin).dwg

Benati 12/12/2022