
Clealco
Açúcar, Etanol e Energia

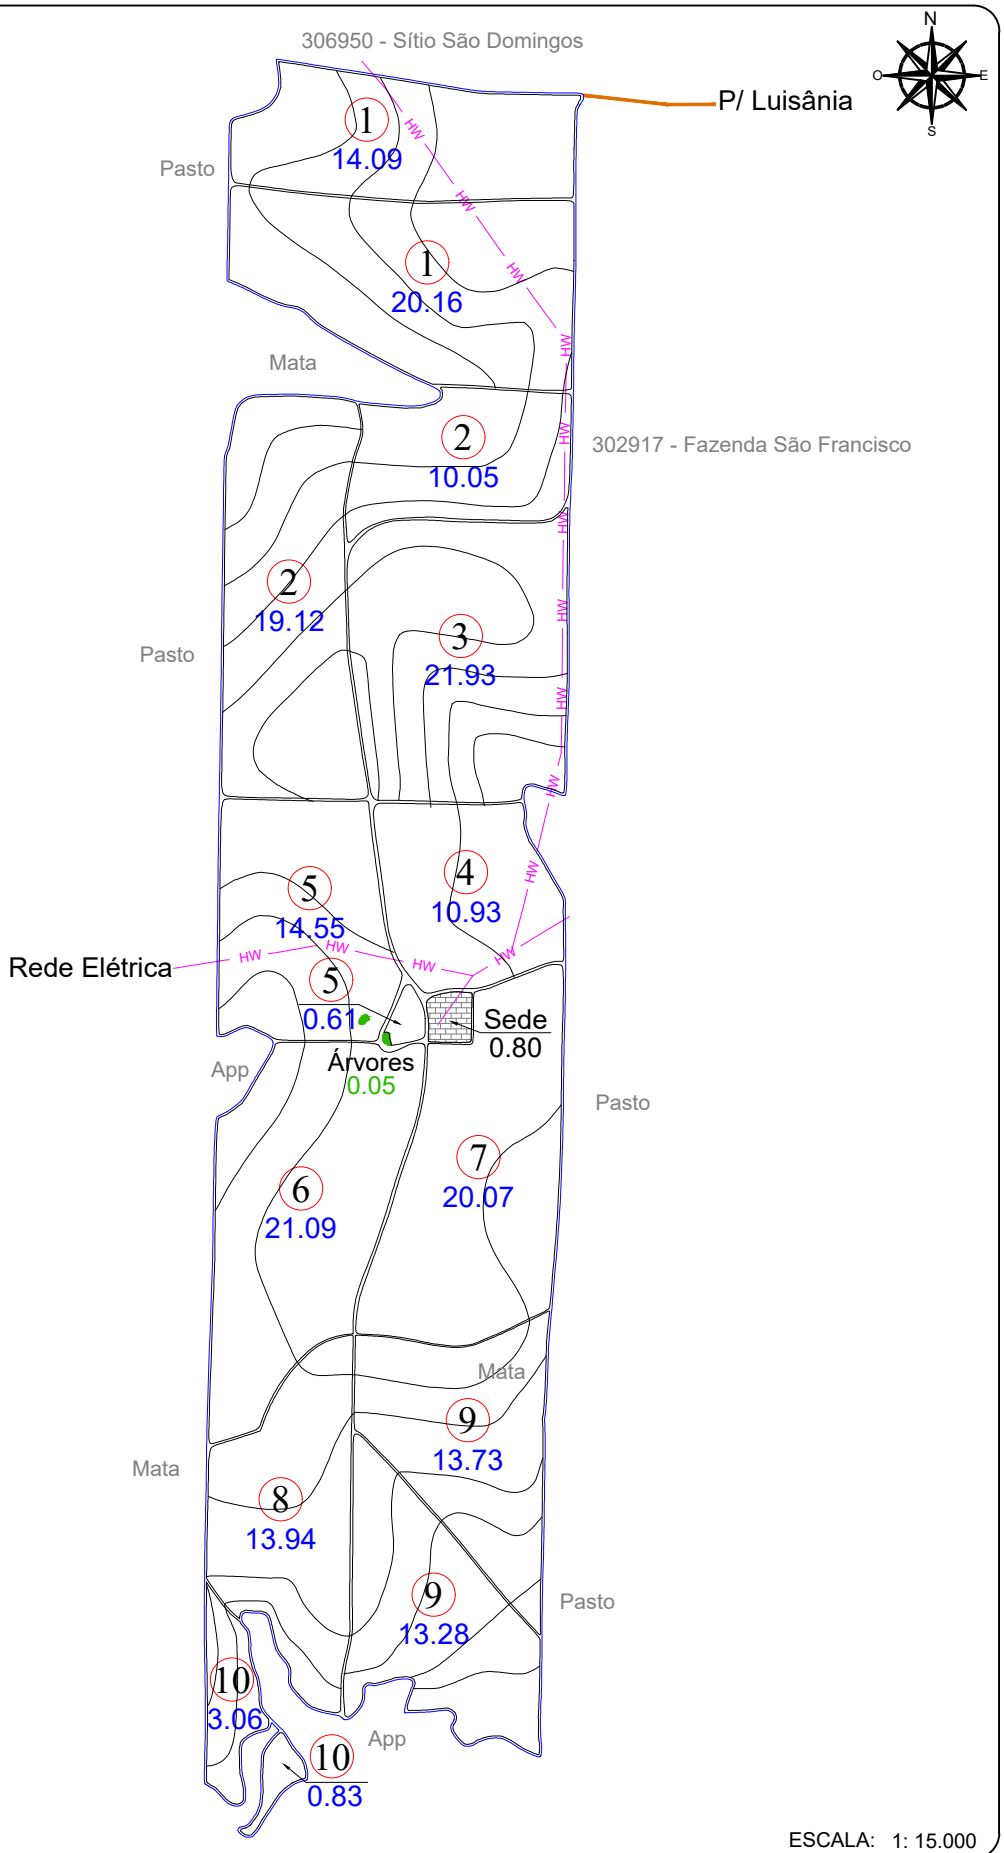

Nº TAL.	DATA PL.	ÁREA (ha)	VARIEDADE
1	04/2021	34.25	CTC 04
2		29.17	
3		21.93	
4		10.93	
5		15.16	
6		21.09	
7		20.07	
8		13.94	
9		27.01	
10		3.89	
TOTAL PLANTIO		197.44	--------

ÁREAS	(ha)	(%)
PLANTIO	197.44	95.93
CARREADORES	7.53	3.66
OUTROS	0.00	0.00
SUB TOTAL AGRICULTÁVEL	204.97	99.59
AP.P.	0.00	0.00
ÁRVORES	0.05	0.02
OUTROS	0.80	0.39
SUB TOTAL NÃO AGRICULT.	0.85	0.41
ÁREA TOTAL	205.82	100.00

C. NÍVEL: 15723.37 m/l 3.62 ha 1.76 %


LEGENDA

- FAZENDA
- TALHÃO
- REDE ELÉTRICA
- VAZIO
- TERRAÇO BASE LARGA
- TERRAÇO EMBUTIDO
- (P.O.A) PATIO DE OPERAÇÃO
- CARREGADO

ESPAÇAMENTO: 1.50 x 1.50
TIRO MÉDIO ESTIMADO: 000.00 m
D.V: 0.00 %

ESCALA: 1: 15.000

CROQUI DE ACESSO

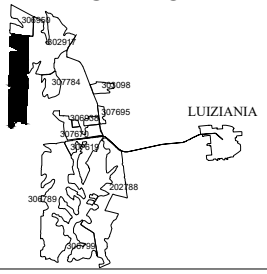

FAZENDA PARAISO

PROPRIETÁRIO: WILLIAN AVILA PEREIRA
COMPRADOR: CLEALCO
MUNICÍPIO: LUIZIÂNIA - SP

DISTÂNCIAS (km):
UNID. I - Asfalto: 28.00 Terra.: 5.50
UNID.I I - Asfalto: 32.00 Terra.: 3.80

COORDENADAS: E(X): 562108.38 N(Y): 7605007.85
LAT: -21°39'25.5131" LONG: -50°23'59.0519"

CLEALCO - AÇÚCAR E ALCOOL S/A - DEPARTAMENTO DE GEOTECNOLOGIA

LEVANTAMENTO VIA:
- SATÉLITE
- GPS / VANT
- GOOGLE

UNIDADE: I
PARTE: A/A
FUNDO AGRÍCOLA: 307262

M:\01-Mapa de safra\Mapas Atualizados\Terceiro\307262 - Fazenda Paraiso (Willian Avila Pereira)\307262 - Fazenda Paraiso (Willian Avila Pereira).dwg

Bruno Gamboa 05/08/26