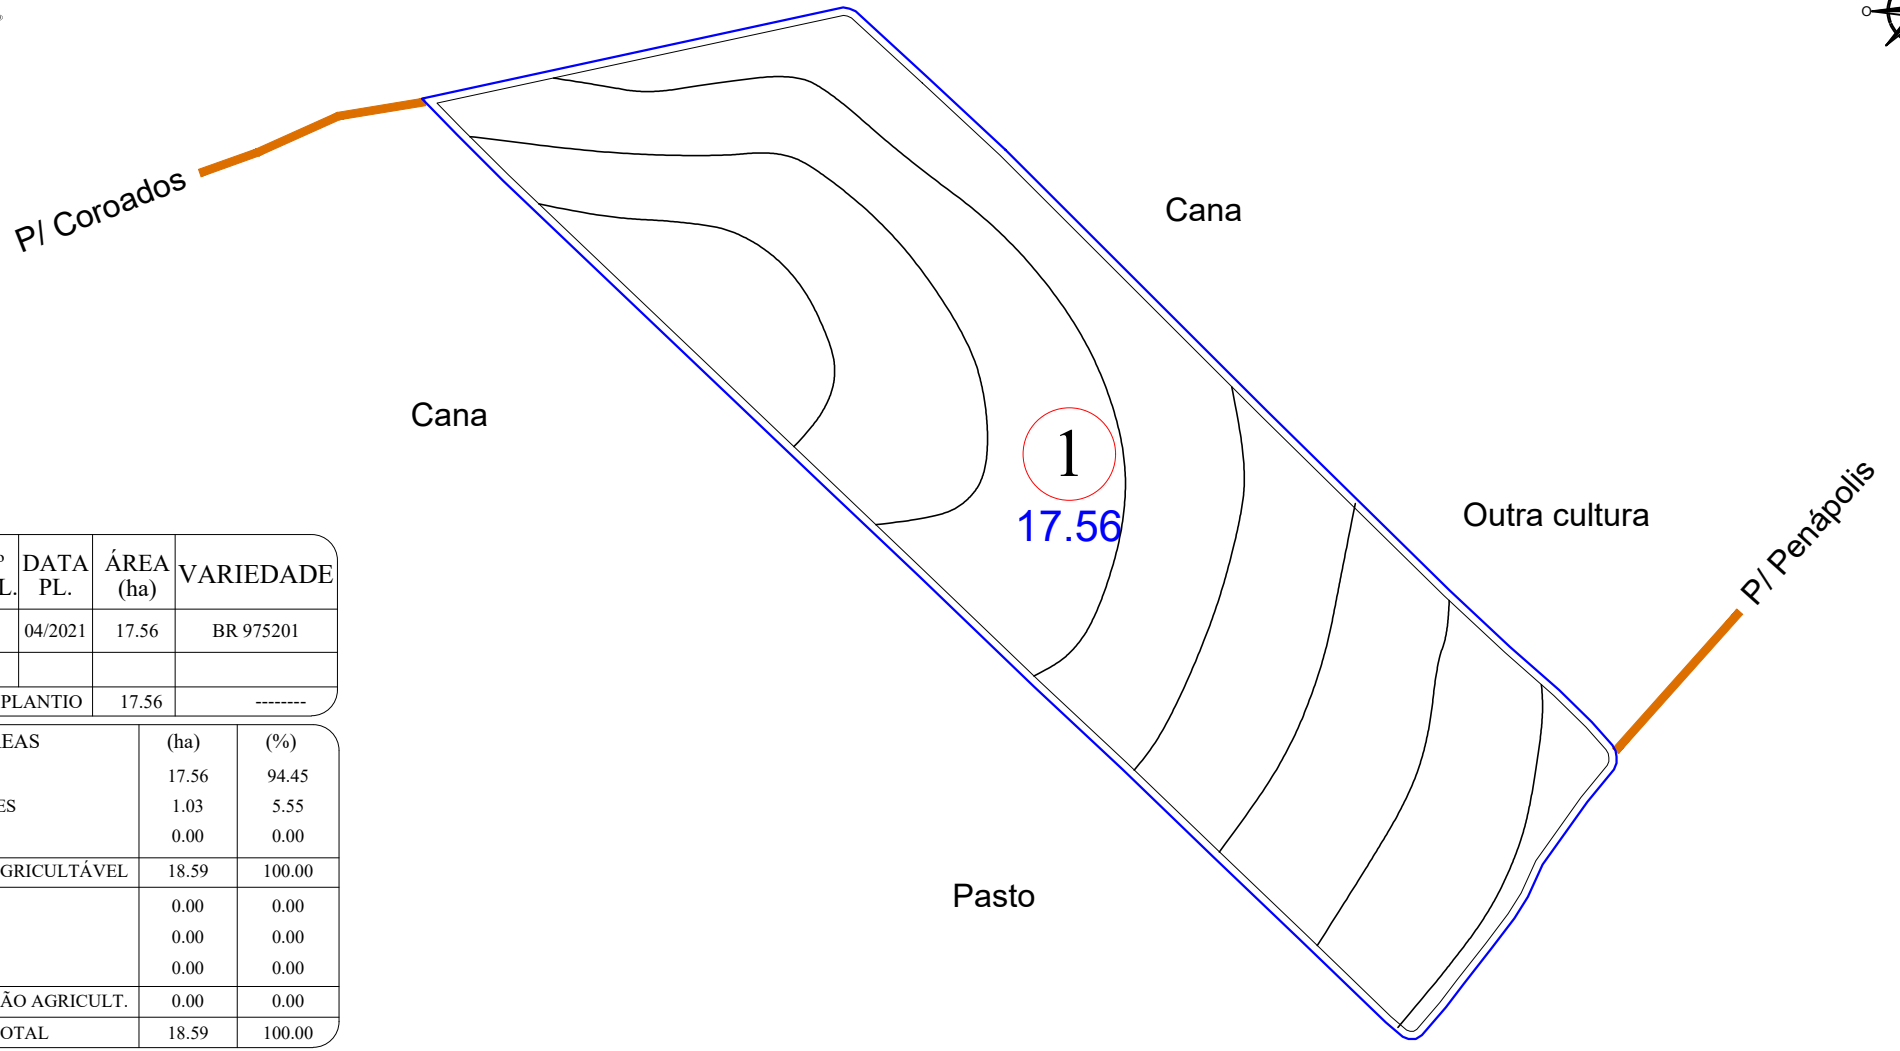


ZONA	Nº TAL.	DATA PL.	ÁREA (ha)	VARIEDADE
999	1	04/2021	17.56	BR 975201
TOTAL PLANTIO			17.56	--------

ÁREAS	(ha)	(%)
PLANTIO	17.56	94.45
CARREADORES	1.03	5.55
OUTROS	0.00	0.00
SUB TOTAL AGRICULTÁVEL	18.59	100.00
AP.P.	0.00	0.00
ÁRVORES	0.00	0.00
OUTROS	0.00	0.00
SUB TOTAL NÃO AGRICULT.	0.00	0.00
ÁREA TOTAL	18.59	100.00

C. NÍVEL: 2658.79 m/l 0.61 ha 3.29 %


ESCALA: 1: 5.000

LEGENDA

- FAZENDA
- TALHÃO
- REDE ELÉTRICA
- TERRAÇO BASE LARGA
- TERRAÇO EMBUTIDO

ESPAÇAMENTO: 1.50 x 1.50
TIRO MÉDIO ESTIMADO: 246.78 m
D.V: 5.74 %

CROQUI DE ACESSO

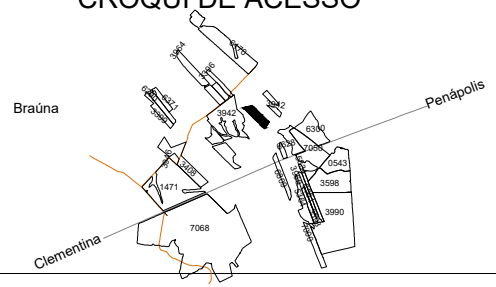

SÍTIO SÃO PEDRO

PROPRIETÁRIO: CARLOS A. BROGIM DUCATTI
COMPRADOR: CLEALCO
MUNICÍPIO: BRAÚNA - SP

DISTÂNCIAS (km):
UNID. I - Asfalto: 24.00 Terra.: 4.80
UNID.I I - Asfalto: 16.50 Terra.: 11.50

COORDENADAS: E(X): 576250.00 N(Y): 7623450.38
LAT: -21°29'23.7179" LONG: -50°15'50.0790"
CLEALCO - AÇÚCAR E ALCOOL S/A - DEPARTAMENTO DE GEOTECNOLOGIA

LEVANTAMENTO VIA:
SATÉLITE
GPS / VANT
GOOGLE

UNIDADE: I
PARTE: A/A
FUNDO AGRÍCOLA: 307270

M:\01-Mapa de safra\Mapas Atualizados\Terceiro\307270 - Sítio São Pedro (Carlos Augusto Brogim Ducatti)\307270 - Sítio São Pedro (Carlos Augusto Brogim Ducatti).dwg

Bruno Gamboa 24/07/25