ZONA DV	Nº TAL.	DATA PL.	ÁREA (ha)	VARIEDADE
999 6.65 %	1	04/2021	11.94	RB 975201
	2		23.03	
	3	04/2022	22.37	
TOTAL PLANTIO			57.34	--------

ÁREAS	(ha)	(%)
PLANTIO	57.34	95.69
CARREADORES	2.58	4.31
OUTROS	0.00	0.00
SUB TOTAL AGRICULTÁVEL	59.92	100.00
AP.P.	0.00	0.00
ÁRVORES	0.00	0.00
OUTROS	0.00	0.00
SUB TOTAL NÃO AGRICULT.	0.00	0.00
ÁREA TOTAL	59.92	100.00


C. NÍVEL: 0.00 m/l 0.00 ha 0.00 %

LEGENDA

- FAZENDA
- TALHÃO
- CURVA DE NÍVEL
- CARREADOR
- CONFRONTANTE
- REDE ELÉTRICA
- TRAJETO VAZIO
- TRAJETO CARREGADO


PLANTIO MANUAL - ESPAÇAMENTO: 1.50 X 1.50
TIRO MÉDIO ESTIMADO: 257.95 m

Clealco
Açúcar, Etanol e Energia

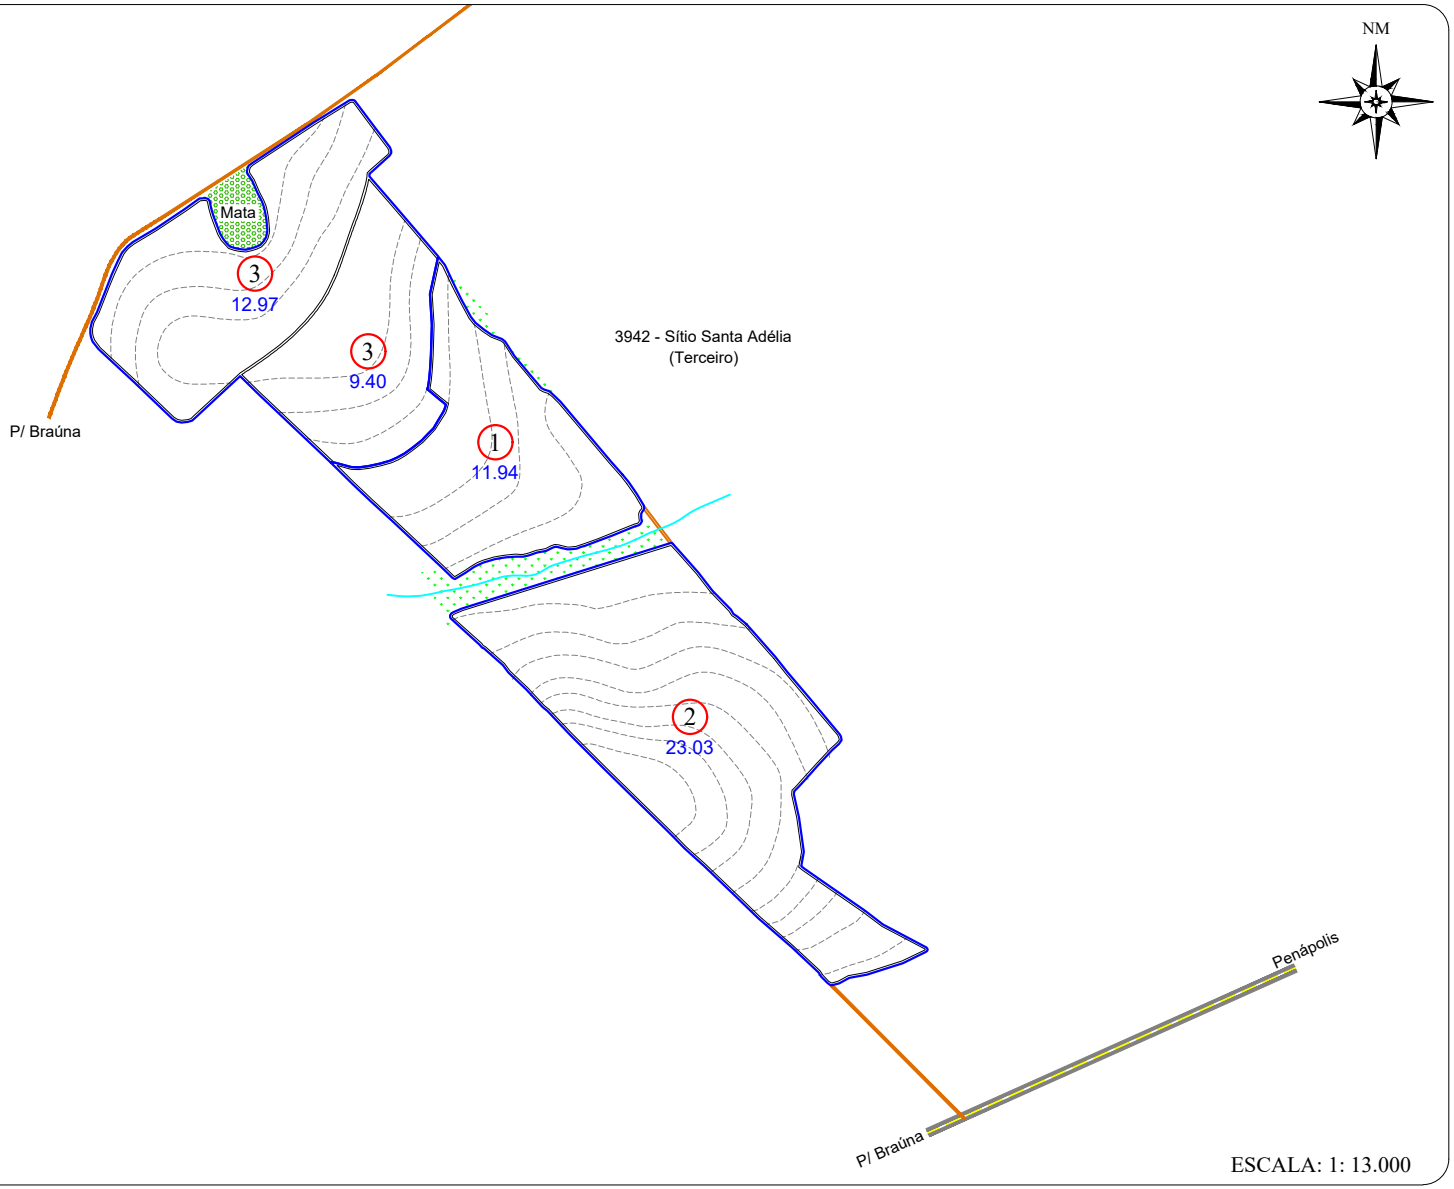

ESCALA: 1: 13.000

CROQUI DE ACESSO

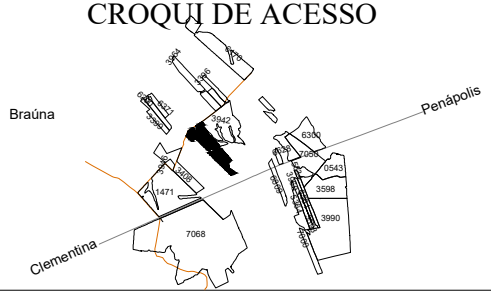

SÍTIO ÁGUA LIMPA

PROPRIETÁRIO: NILTON CEZÁRIO ANNELLI
COMPRADOR: CLEALCO S/A
MUNICÍPIO: BRAÚNA

DISTÂNCIAS (km):
UNID. I - Asfalto: 18.50 Terra.: 4.80
UNID.I I - Asfalto: 16.50 Terra.: 11.50
UNID. III -Asfalto: 5.80 Terra.: 4.80

COORDENADAS: E(X): 574587.58 N(Y): 7623161.59
LAT: -21°29'33.3623" LONG: -50°16'47.8036"

CLEALCO - AÇÚCAR E ALCOOL S/A - DEPARTAMENTO DE TOPOGRAFIA

UNIDADE: I
PARTE: A/A
FUNDO AGRÍCOLA: 307279

M:\01-Mapa de safra\Mapas Atualizados\Terceiro\307279 - Sitio Agua Limpa (Nilton Cezário Annelli)\307279 - Sitio Agua Limpa (Nilton Cezário Annelli).dwg

Fernanda Bezerra 13/02/22