
Clealco
Açúcar, Etanol e Energia

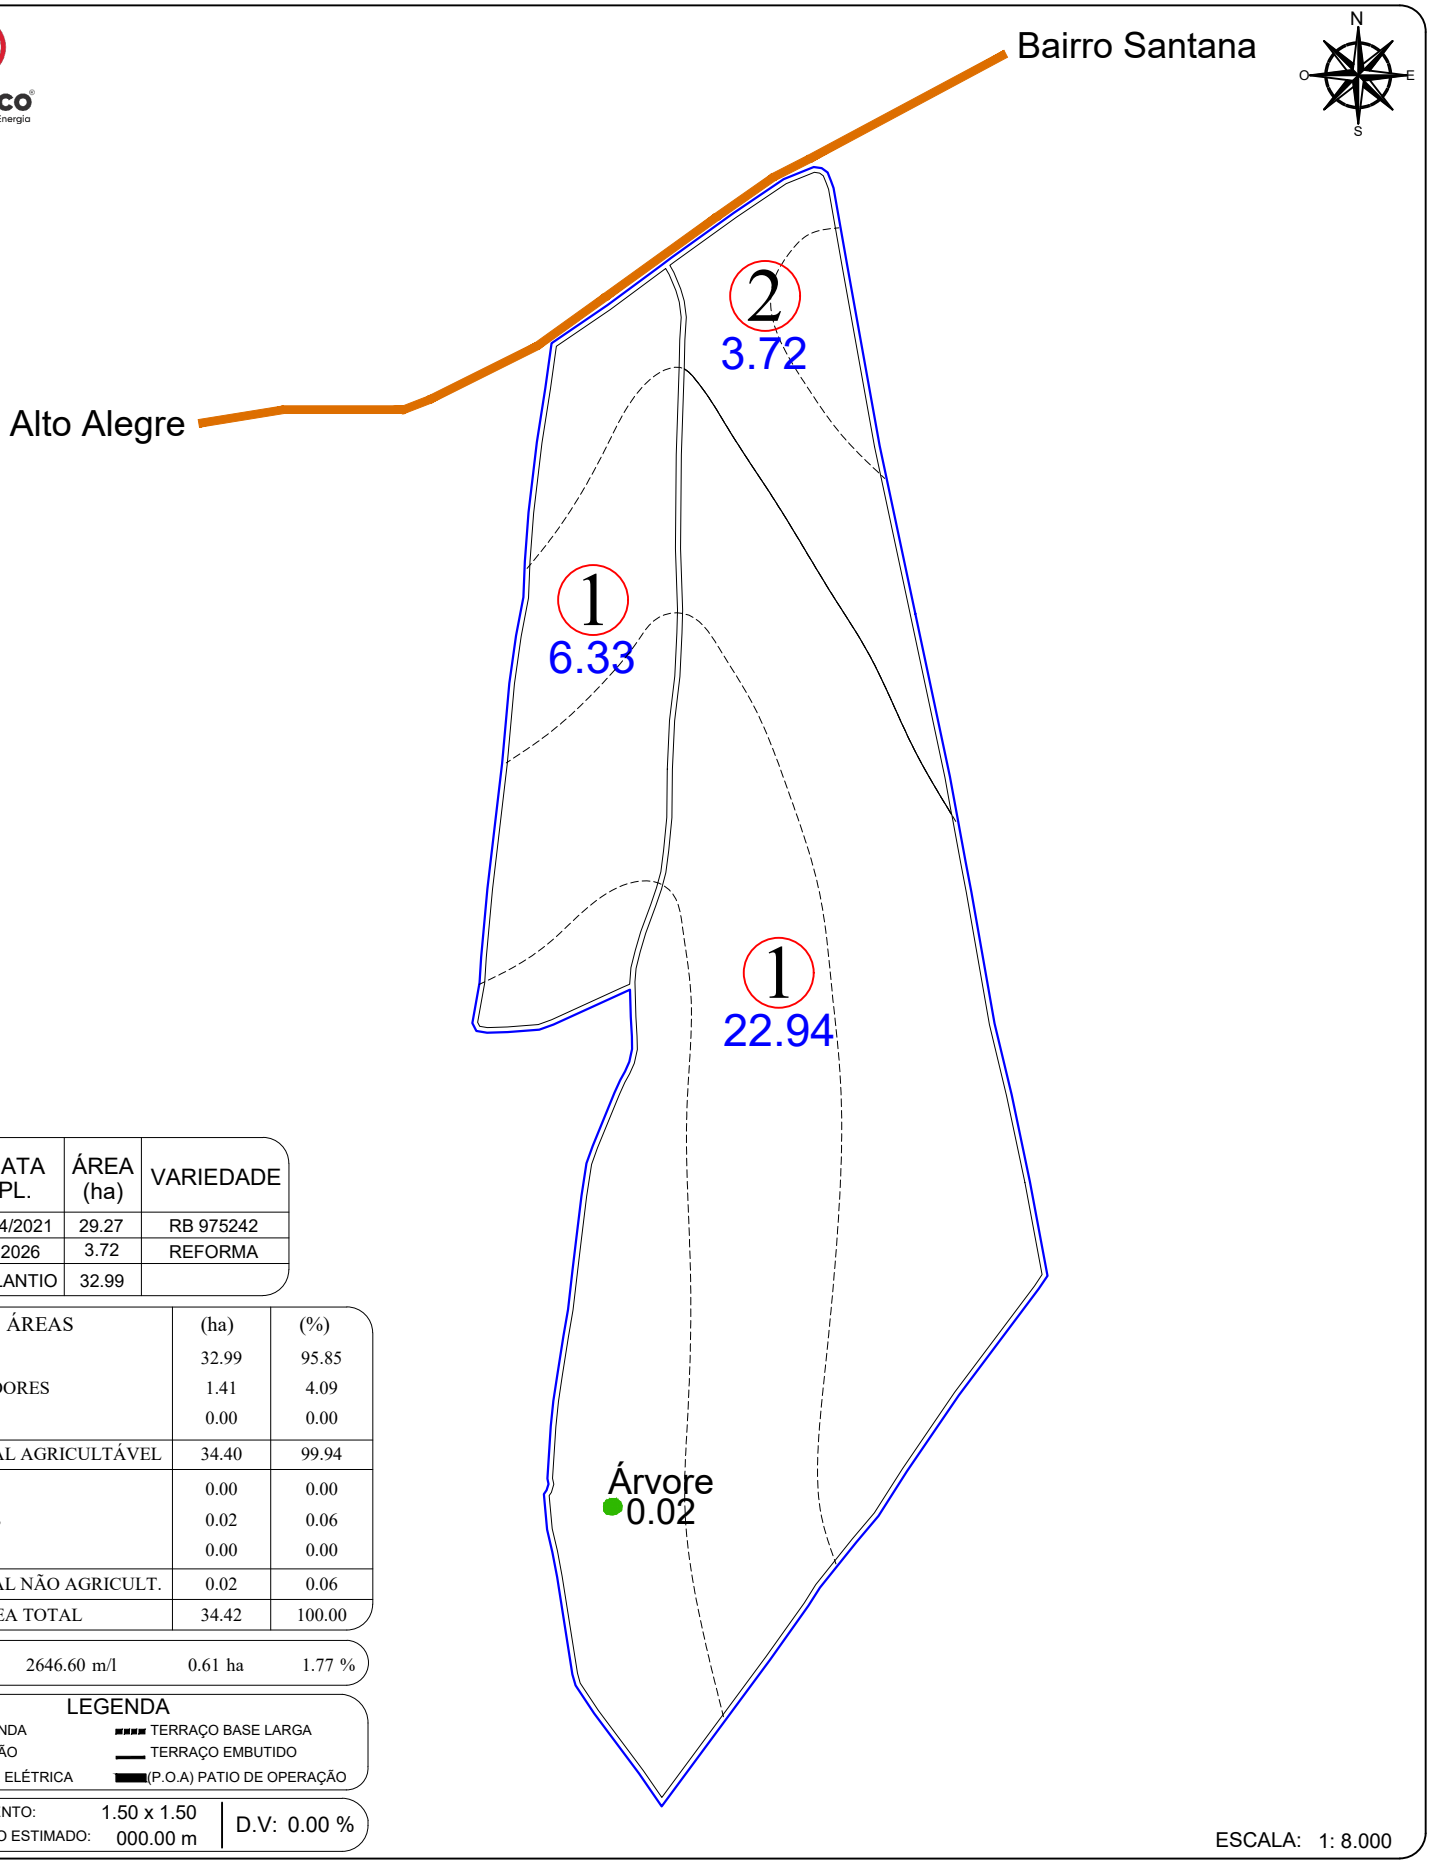

Nº TAL.	DATA PL.	ÁREA (ha)	VARIEDADE
1	04/2021	29.27	RB 975242
2	2026	3.72	REFORMA
TOTAL PLANTIO		32.99	

ÁREAS	(ha)	(%)
PLANTIO	32.99	95.85
CARREADORES	1.41	4.09
OUTROS	0.00	0.00
SUB TOTAL AGRICULTÁVEL	34.40	99.94
AP.P.	0.00	0.00
ÁRVORES	0.02	0.06
OUTROS	0.00	0.00
SUB TOTAL NÃO AGRICULT.	0.02	0.06
ÁREA TOTAL	34.42	100.00

C. NÍVEL: 2646.60 m/l 0.61 ha 1.77 %


LEGENDA

- FAZENDA
- TALHÃO
- REDE ELÉTRICA
- TERRAÇO BASE LARGA
- TERRAÇO EMBUTIDO
- (P.O.A) PATIO DE OPERAÇÃO

ESPAÇAMENTO: 1.50 x 1.50
TIRO MÉDIO ESTIMADO: 000.00 m
D.V: 0.00 %

ESCALA: 1: 8.000

CROQUI DE ACESSO

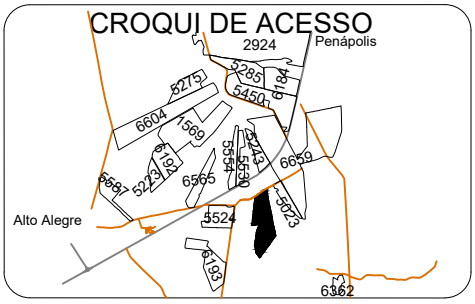

SÍTIO DOIS IRMÃOS III

PROPRIETÁRIO: MARCIA DOMINGUES C. PEREIRA
COMPRADOR: CLEALCO
MUNICÍPIO: ALTO ALEGRE - SP

DISTÂNCIAS (km):
UNID. I - Asfalto: 53.00 Terra.: 1.50
UNID.I I - Asfalto: 45.20 Terra.: 1.50

COORDENADAS: E(X): 589884.32 N(Y): 7613447.59
LAT: -21°34'46.7604" LONG: -50°7'54.3493"

CLEALCO - AÇÚCAR E ALCOOL S/A - DEPARTAMENTO DE GEOTECNOLOGIA

LEVANTAMENTO VIA:
- SATÉLITE
- GPS / VANT
- GOOGLE

UNIDADE: II
PARTE: A/A
FUNDO AGRÍCOLA: 307281

M:\01-Mapa de safra\Mapas Atualizados\Terceiro\307281 - Sítio Dois Irmãos III (Marcia Domingues Cruz Pereira)\307281 - Sítio Dois Irmãos III (Marcia Domingues Cruz Pereira).dwg

Benati 05/03/2026