
Clealco
Açúcar, Etanol e Energia

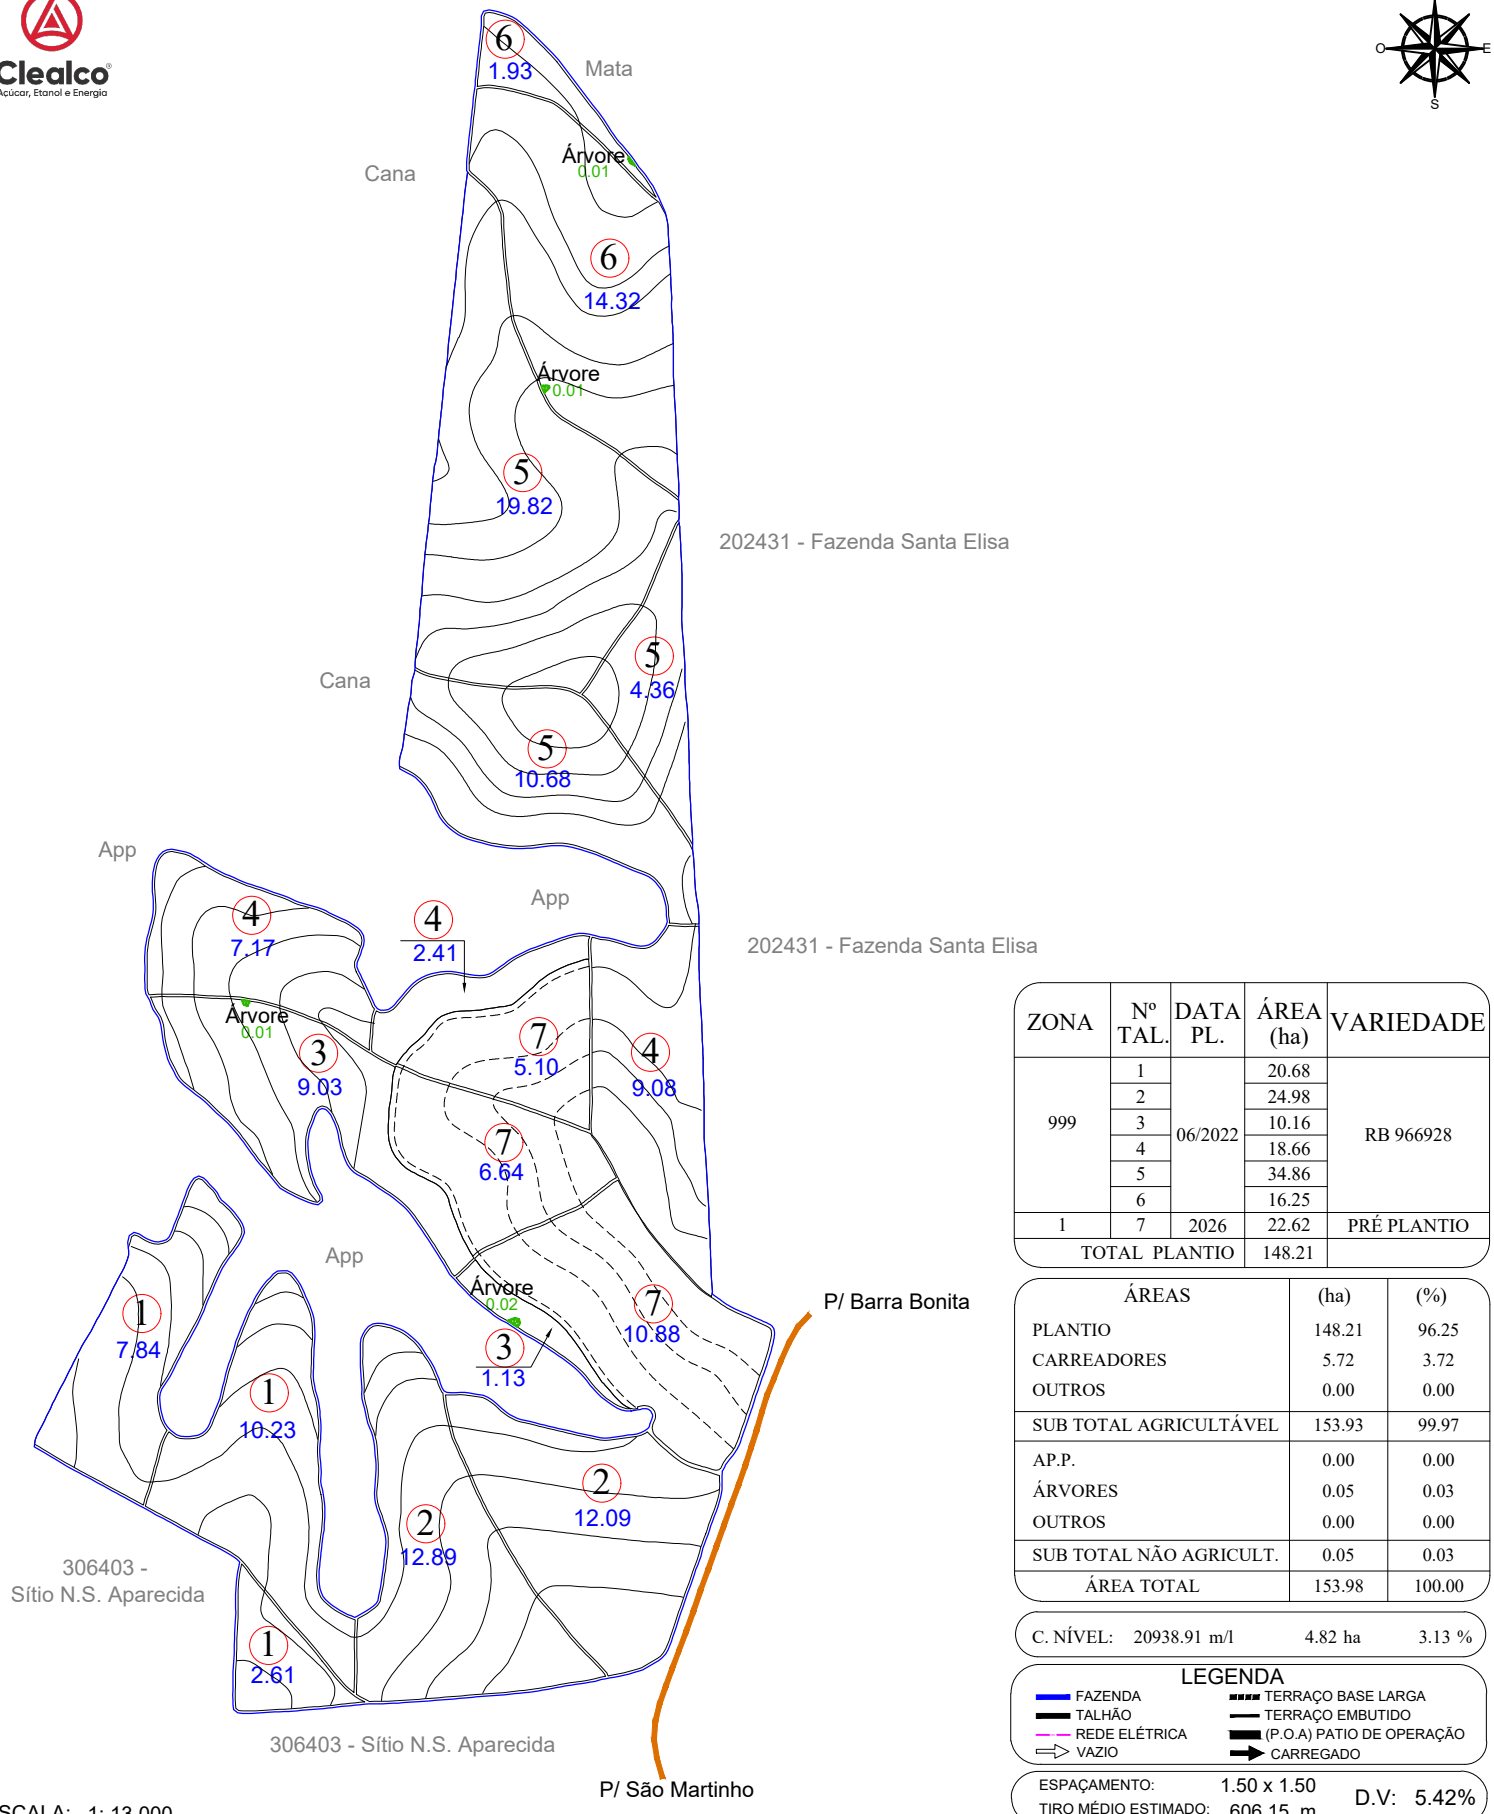

ESCALA: 1: 13.000

ZONA	Nº TAL.	DATA PL.	ÁREA (ha)	VARIEDADE
999	1	06/2022	20.68	RB 966928
	2		24.98	
	3		10.16	
	4		18.66	
	5		34.86	
	6		16.25	
1	7	2026	22.62	PRÉ PLANTIO
TOTAL PLANTIO			148.21	

ÁREAS	(ha)	(%)
PLANTIO	148.21	96.25
CARREADORES	5.72	3.72
OUTROS	0.00	0.00
SUB TOTAL AGRICULTÁVEL	153.93	99.97
AP.P.	0.00	0.00
ÁRVORES	0.05	0.03
OUTROS	0.00	0.00
SUB TOTAL NÃO AGRICULT.	0.05	0.03
ÁREA TOTAL	153.98	100.00


C. NÍVEL: 20938.91 m/l 4.82 ha 3.13 %

LEGENDA

- FAZENDA
- TALHÃO
- REDE ELÉTRICA
- VAZIO
- TERRAÇO BASE LARGA
- TERRAÇO EMBUTIDO
- (P.O.A) PATIO DE OPERAÇÃO
- CARREGADO

ESPAÇAMENTO: 1.50 x 1.50
TIRO MÉDIO ESTIMADO: 606.15 m
D.V: 5.42%

CROQUI DE ACESSO

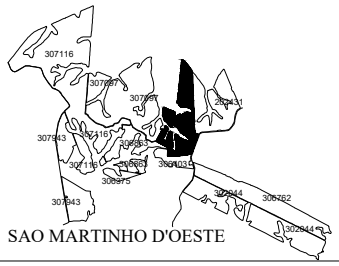

FAZENDA BONITO

PROPRIETÁRIO: CLEBER AMARAL HUNGARO
COMPRADOR: CLEALCO
MUNICÍPIO: PENÁPOLIS - SP

DISTÂNCIAS (km):
UNID. I - Asfalto: 20.50 Terra.: 2.00
UNID.I I - Asfalto: 68.00 Terra.: 2.00

COORDENADAS: E(X): 575653.70 N(Y): 7617285.27
LAT: -21°32'44.3209" LONG: -50°16'9.7988"

CLEALCO - AÇÚCAR E ALCOOL S/A - DEPARTAMENTO DE GEOTECNOLOGIA

LEVANTAMENTO VIA:
- SATÉLITE
- GPS / VANT
- GOOGLE

UNIDADE: I
PARTE: A/A
FUNDO AGRÍCOLA: 307286

M:\01-Mapa de safra\Mapas Atualizados\Terceiro\307286 - Fazenda Bonito (Cleber Amaral Hungaro)\307286 - Fazenda Bonito (Cleber Amaral Hungaro).dwg

Bruno Gamboa 25/06/26