ZONA DV	Nº TAL.	DATA PL.	ÁREA (ha)	VARIEDADE
999 4.46%	1	05/2021	6.00	RB 975242
	2		9.19	
	3		29.56	
TOTAL PLANTIO			44.75	--------

ÁREAS	(ha)	(%)
PLANTIO	44.75	91.90
CARREADORES	3.86	7.92
OUTROS	0.00	0.00
SUB TOTAL AGRICULTÁVEL	48.61	99.82
AP.P.	0.00	0.00
ÁRVORES	0.09	0.18
OUTROS	0.00	0.00
SUB TOTAL NÃO AGRICULT.	0.09	0.18
ÁREA TOTAL	48.70	100.00


C. NÍVEL: 0.00 m/l 0.00 ha 0.00 %

LEGENDA

- FAZENDA
- TALHÃO
- CURVA DE NÍVEL
- CARREADOR
- CONFRONTANTE
- REDE ELÉTRICA
- TRAJETO VAZIO
- TRAJETO CARREGADO


PLANTIO MANUAL - ESPAÇAMENTO: 1.50 X 1.50
TIRO MÉDIO ESTIMADO: 174.03 m

Clealco
Açúcar, Etanol e Energia

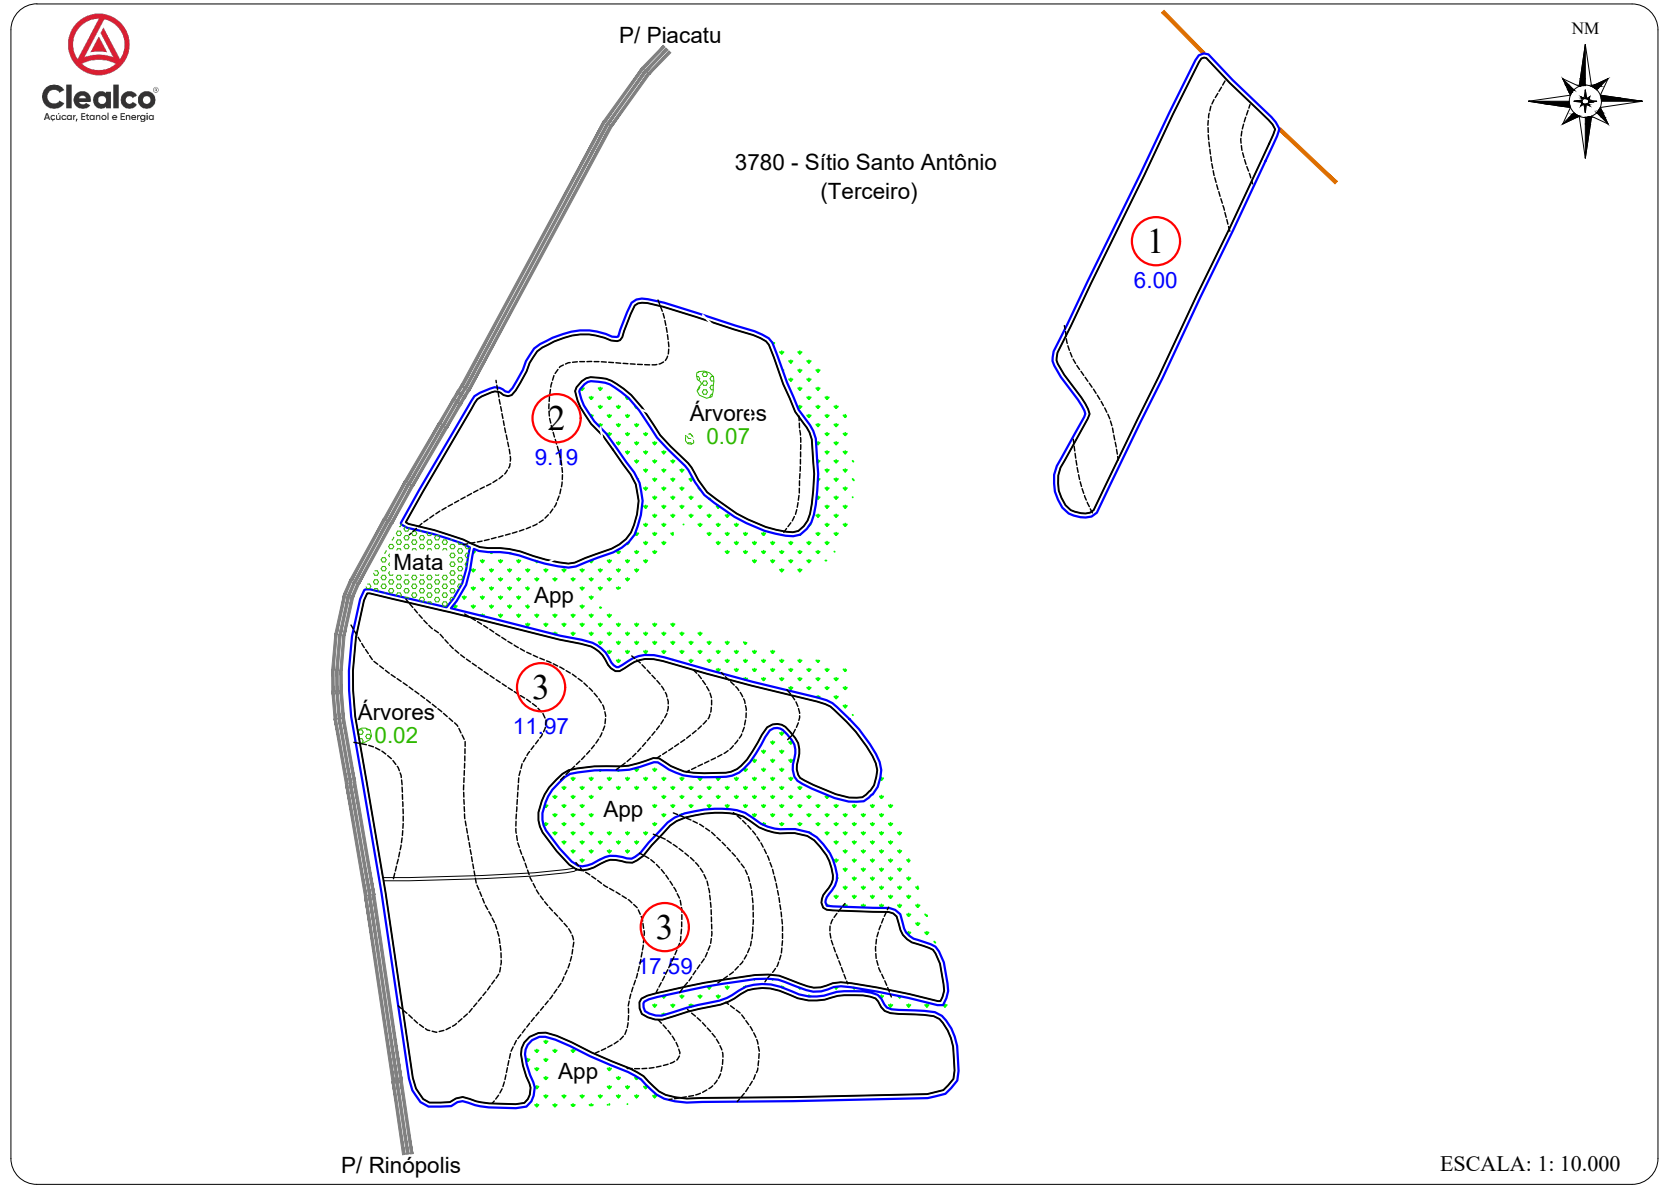

ESCALA: 1: 10.000

CROQUI DE ACESSO

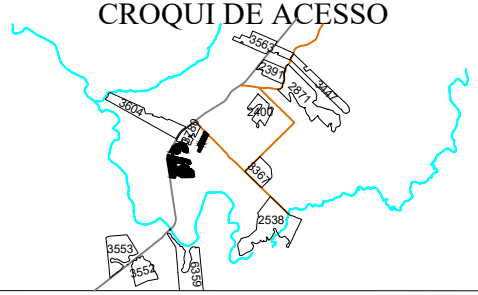

SÍTIO SÃO JOÃO

PROPRIETÁRIO: VERA LUCIA LEMES DA SILVA
COMPRADOR: CLEALCO S/A
MUNICÍPIO: PIACATU

DISTÂNCIAS (km):
UNID. I - Asfalto: 26.00 Terra.: 4.00
UNID.I I - Asfalto: 62.00 Terra.: 1.50
UNID. III -Asfalto: 61.00 Terra.: 4.00

COORDENADAS: E(X): 538398.76 N(Y): 7608104.96
LAT: -21°37'47.1915" LONG: -50°37'44.2252"

CLEALCO - AÇÚCAR E ALCOOL S/A - DEPARTAMENTO DE TOPOGRAFIA

UNIDADE: I
PARTE: A/A
FUNDO AGRÍCOLA: 307296

M:\01-Mapa de safra\Mapas Atualizados\Terceiro\307296 - Sítio São João (Vera Lucia Lemes da Silva)\307296 - Sítio São João (Vera Lucia Lemes da Silva).dwg

Fernanda Bezerra 07/04/22