ZONA DV	Nº TAL.	DATA PL.	ÁREA (ha)	VARIEDADE
999	1	04/2021	16.77	RB975201
2.88 %	2	04/2022	8.86	
TOTAL PLANTIO			25.63	--------


ÁREAS	(ha)	(%)
PLANTIO	25.63	94.66
CARREADORES	1.21	4.49
OUTROS	0.00	0.00
SUB TOTAL AGRICULTÁVEL	26.84	99.15
AP.P.	0.00	0.00
ÁRVORES	0.09	0.33
OUTROS	0.14	0.52
SUB TOTAL NÃO AGRICULT.	0.23	0.85
ÁREA TOTAL	27.07	100.00

C. NÍVEL: 329.12 m/l 0.08 ha 0.28 %


LEGENDA

- FAZENDA
- TALHÃO
- CURVA DE NÍVEL
- CARREADOR
- CONFRONTANTE
- REDE ELÉTRICA
- TRAJETO VAZIO
- TRAJETO CARREGADO

PLANTIO MANUAL - ESPAÇAMENTO: 1.50 X 1.50
TIRO MÉDIO ESTIMADO: 400.78 m

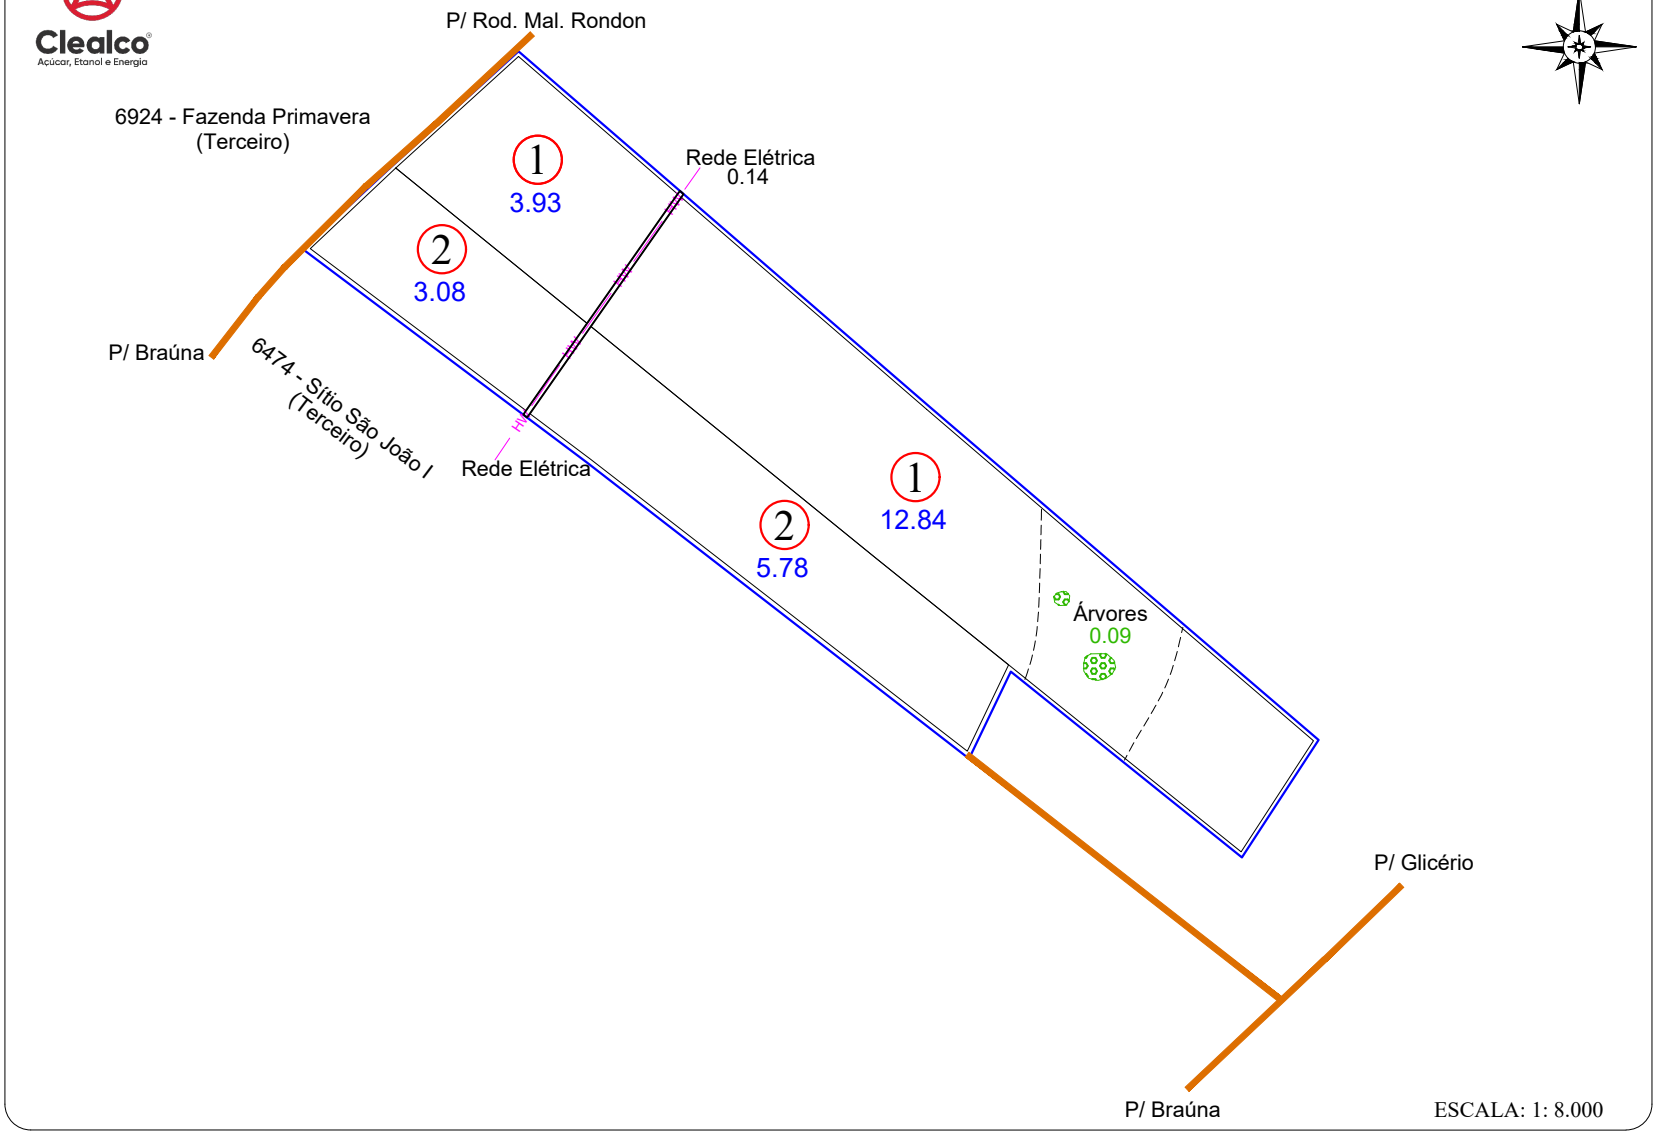

CROQUI DE ACESSO

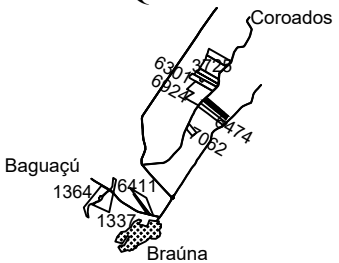

SÍTIO NOSSA SENHORA DAS GRAÇAS

PROPRIETÁRIO: MAURO BARZOTTI
COMPRADOR: CLEALCO S/A
MUNICÍPIO: PENÁPOLIS

DISTÂNCIAS (km):
UNID. I - Asfalto: 27.50 Terra.: 4.30
UNID.I I - Asfalto: 71.50 Terra.: 3.60
UNID. III -Asfalto: 32.00 Terra.: 1.00

COORDENADAS: E(X): 573349.33 N(Y): 7627081.08
LAT: -21°27'26.0687" LONG: -50°17'31.4509"

CLEALCO - AÇÚCAR E ALCOOL S/A - DEPARTAMENTO DE TOPOGRAFIA

UNIDADE: I
PARTE: A/A
FUNDO AGRÍCOLA: 307298

M:\01-Mapa de safra\Mapas Atualizados\Terceiro\307298 - Sitio Nossa Senhora das Graças (Mauro Barzotti)\307298 - Sitio Nossa Senhora das Graças (Mauro Barzotti).dwg