ZONA DV	Nº TAL.	DATA PL.	ÁREA (ha)	VARIEDADE
999 5.36 %	1	04/2020	9.07	CTC 04
	2		9.69	
	3	03/2022	8.95	
	4		36.05	
TOTAL PLANTIO			63.76	--------

ÁREAS	(ha)	(%)
PLANTIO	63.76	95.32
CARREADORES	3.13	4.68
OUTROS	0.00	0.00
SUB TOTAL AGRICULTÁVEL	66.89	100.00
AP.P.	0.00	0.00
ÁRVORES	0.00	0.00
OUTROS	0.00	0.00
SUB TOTAL NÃO AGRICULT.	0.00	0.00
ÁREA TOTAL	66.89	100.00


C. NÍVEL: 7813.97 m/l 1.80 ha 2.69 %

LEGENDA

- FAZENDA
- TALHÃO
- CURVA DE NÍVEL
- CARREADOR
- CONFRONTANTE
- REDE ELÉTRICA
- TRAJETO VAZIO
- TRAJETO CARREGADO


PLANTIO MANUAL - ESPAÇAMENTO: 1.50 X 1.50
TIRO MÉDIO ESTIMADO: 199.54m

Clealco
Açúcar, Etanol e Energia

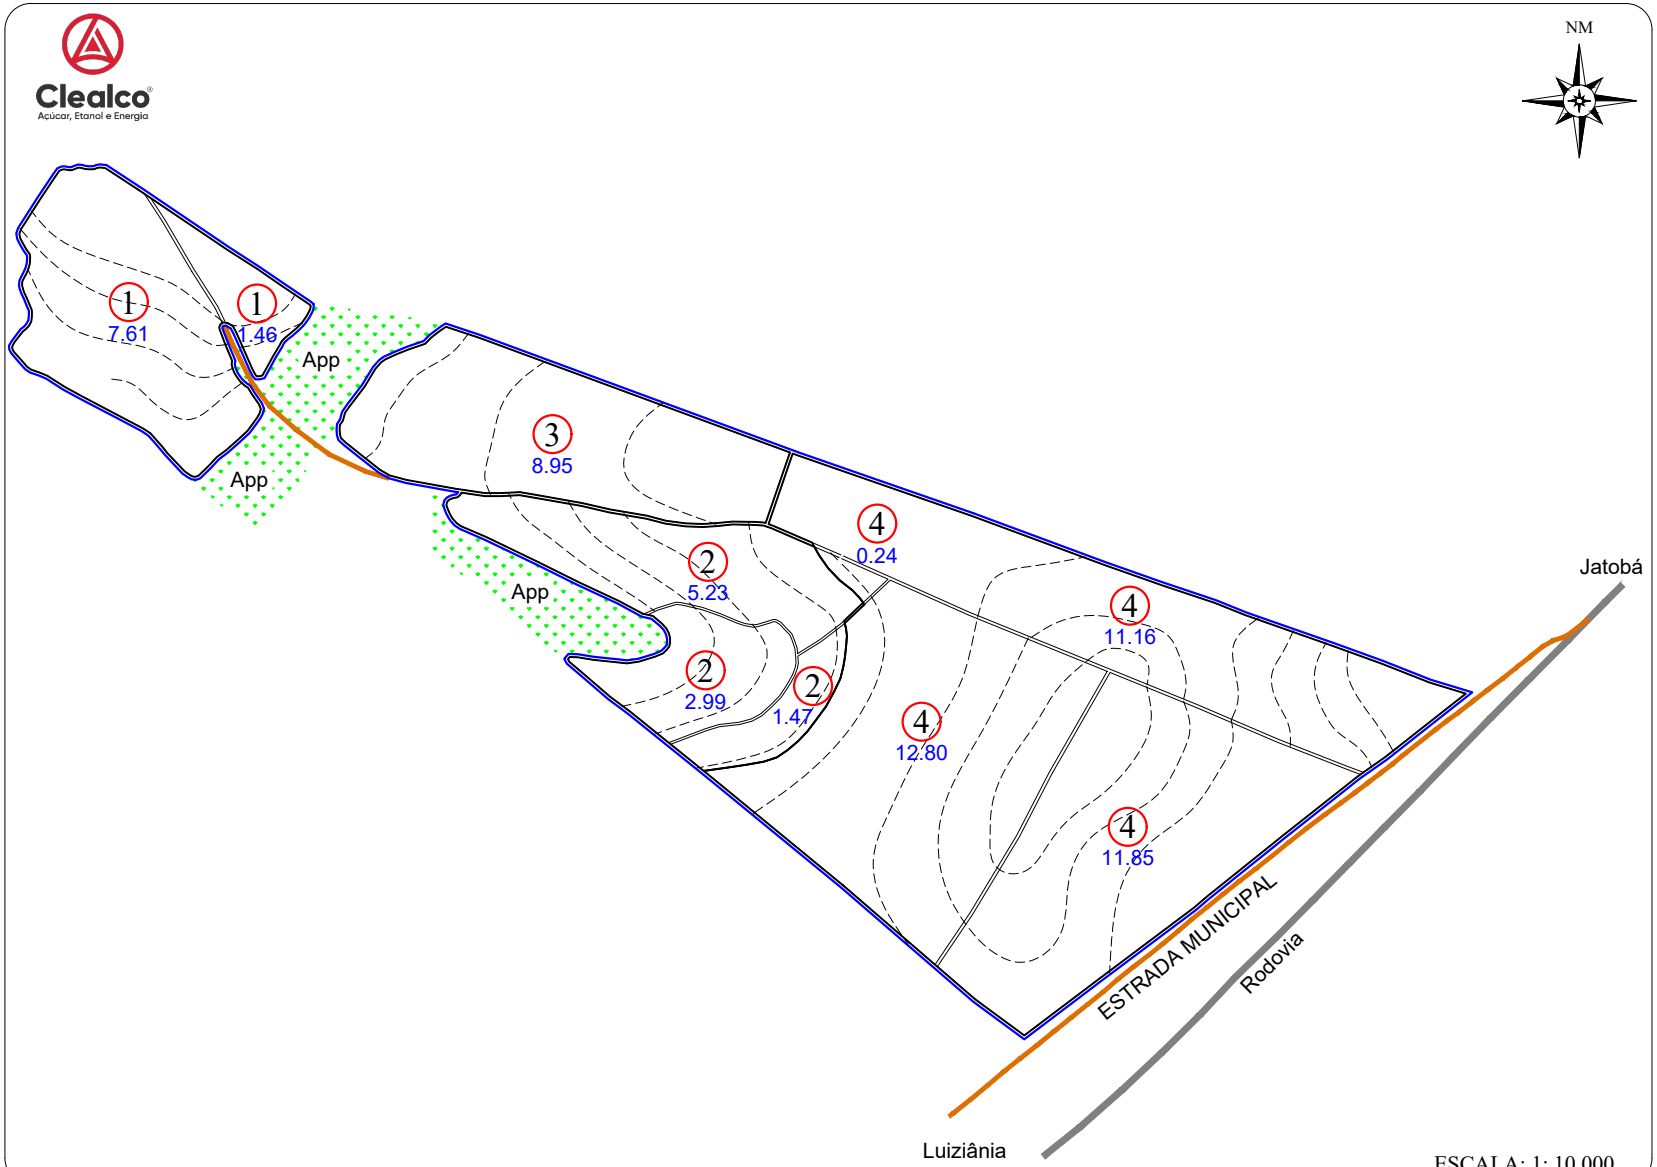

ESCALA: 1: 10.000

CROQUI DE ACESSO

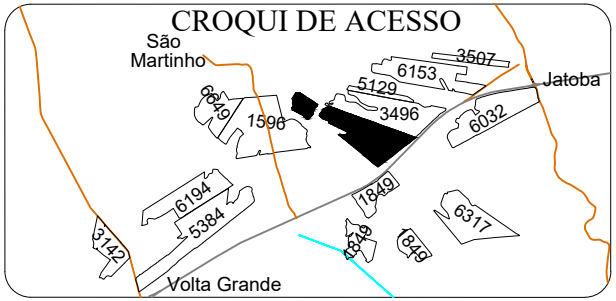

SITIO BOA VISTA

PROPRIETÁRIO: NATAN REVOREDO DIAS
COMPRADOR: CLEALCO S/A
MUNICÍPIO: ALTO ALEGRE

DISTÂNCIAS (km):
UNID. I - Asfalto: 41.00 Terra.: 6.00
UNID.I I - Asfalto: 27.30 Terra.: 2.00
UNID. III -Asfalto: 27.00 Terra.: 1.30

COORDENADAS: E(X): 574883.21 N(Y): 7607755.18
LAT: -21°37'54.3892" LONG: -50°16'35.0447"

CLEALCO - AÇÚCAR E ALCOOL S/A - DEPARTAMENTO DE TOPOGRAFIA

UNIDADE: I
PARTE: A/A
FUNDO AGRÍCOLA: 307307

M:\01-Mapa de safra\Mapas Atualizados\Terceiro\307307 - Sítio Boa Vista (Natan Revoredo Dias)\307307 - Sítio Boa Vista (Natan Revoredo Dias).dwg

Peterson Santos 13/03/2023