ZONA D.V.	Nº TAL.	DATA PL.	ÁREA (ha)	VAR.
1 8.70%	1	04/2022	16.17	RB975242
	2		13.35	
	3		40.18	RB966928
	4		38.17	RB975242
	5		51.64	RB966928
	6		31.70	CTC4
	7		26.40	
	8		25.17	
	9		14.02	
	10		66.93	
TOTAL PLANTIO			323.73	--------

ÁREAS	(ha)	(%)
PLANTIO	323.73	96.11
CARREADORES	12.13	3.60
OUTROS	0.00	0.00
SUB TOTAL AGRICULTÁVEL	335.86	99.71
AP.P.	0.91	0.27
ÁRVORES	0.05	0.01
OUTROS	0.00	0.00
SUB TOTAL NÃO AGRICULT.	0.96	0.29
ÁREA TOTAL	336.82	100.00


C. NÍVEL: 15314.10 m/l 3.52 ha 1.05 %

LEGENDA

- FAZENDA
- TALHÃO
- CURVA DE NÍVEL
- CARREADOR
- CONFRONTANTE
- REDE ELÉTRICA
- TRAJETO VAZIO
- TRAJETO CARREGADO

PLANTIO MANUAL - ESPAÇAMENTO: 1.50 X 1.50
TIRO MÉDIO ESTIMADO: 000.00m


Clealco
Açúcar, Etanol e Energia

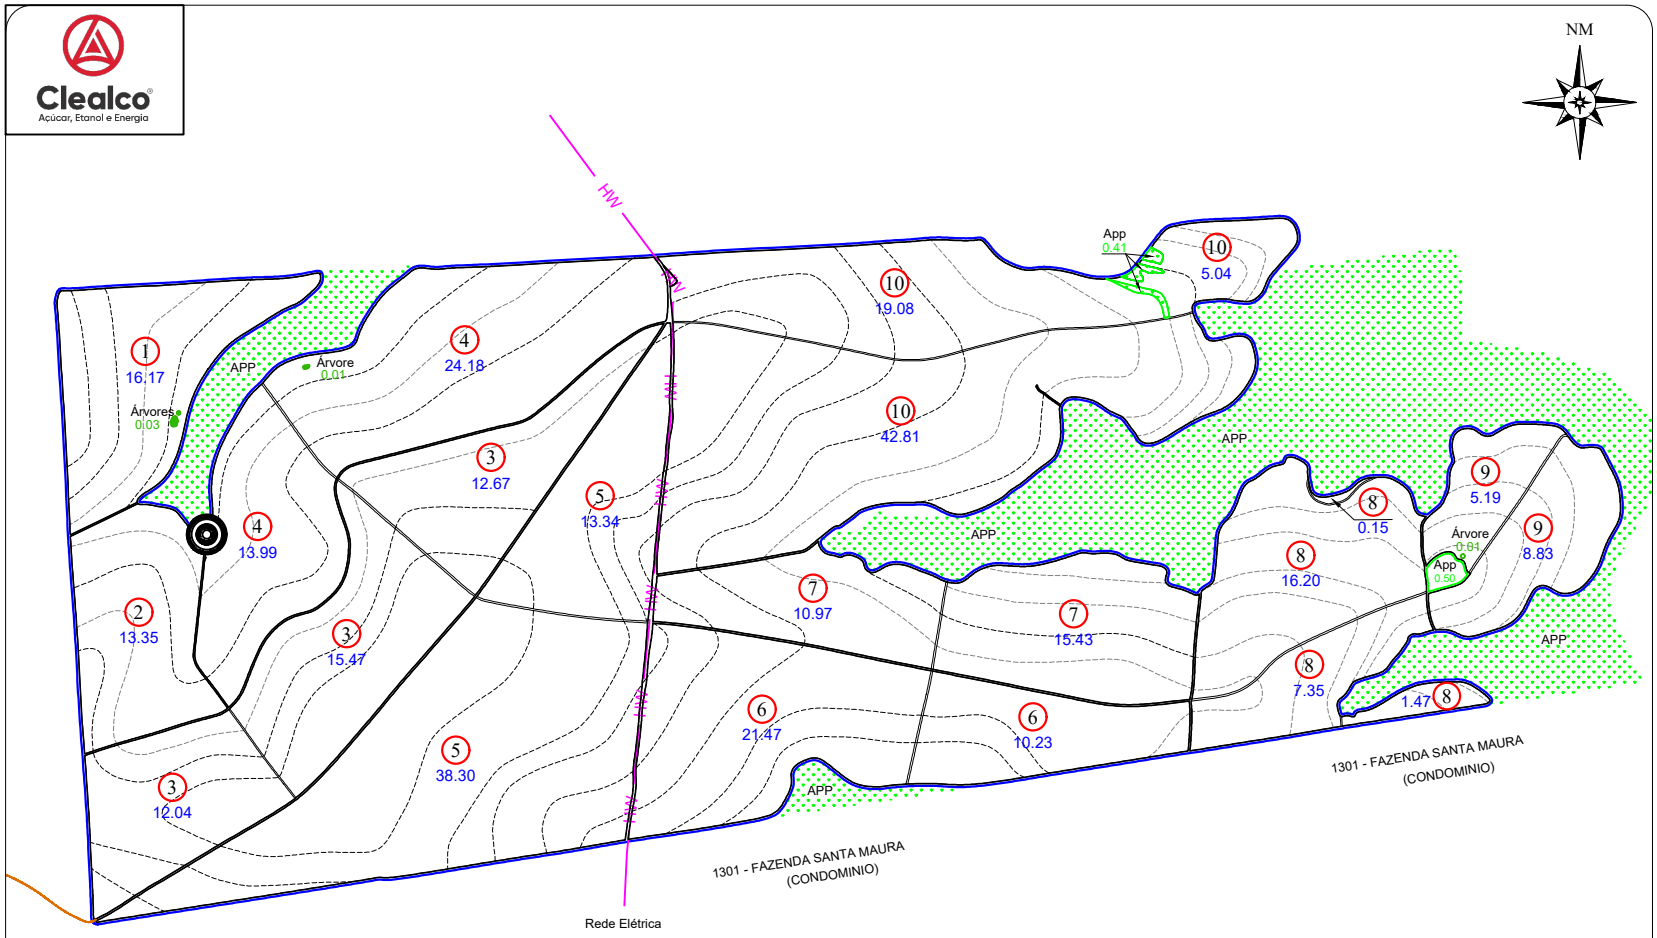

POÇO DE MONITORAMENTO DE ÁGUA

ESCALA: 1: 17.000

CROQUI DE ACESSO

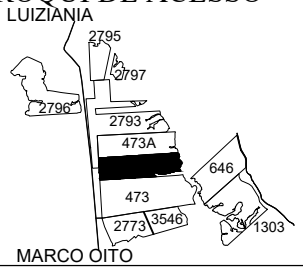

FAZENDA SANTA ODETE

PROPRIETÁRIO: WILLIAN ÁVILA PEREIRA E OUTRO
COMPRADOR: CLEALCO S/A
MUNICÍPIO: QUEIROZ

DISTÂNCIAS (km):
UNID. I - Asfalto: 32.80 Terra.: 11.00
UNID.I I - Asfalto: 17.00 Terra.: 15.40
UNID. III -Asfalto: 34.00 Terra.: 12.60

COORDENADAS: E(X): 571712.7731 N(Y): 7594673.348
LAT: 21°45'0,3231" LONG: 50°18'23,2922"

CLEALCO - AÇÚCAR E ALCOOL S/A - DEPARTAMENTO DE TOPOGRAFIA

UNIDADE: I
PARTE: A/A
FUNDO AGRÍCOLA: 307310

M:\01-Mapa de safra\Mapas Atualizados\Terceiro\307310 - Fazenda Santa Odete (Willian Ávila)\307310 - Fazenda Santa Odete (Willian Ávila).dwg

Peterson Santos 02/09/22