ZONA DV	Nº TAL.	DATA PL.	ÁREA (ha)	VARIEDADE
999 5.03 %	1	06/2022	27.93	RB 975242
	2		11.04	
	3		42.29	
	4		31.21	
	5		32.49	
	6		25.78	
	7		33.43	
	8		33.01	
TOTAL PLANTIO			237.18	--------

ÁREAS	(ha)	(%)
PLANTIO	237.18	96.18
CARREADORES	9.25	3.75
OUTROS	0.00	0.00
SUB TOTAL AGRICULTÁVEL	246.43	99.93
AP.P.	0.00	0.00
ÁRVORES	0.18	0.07
OUTROS	0.00	0.00
SUB TOTAL NÃO AGRICULT.	0.18	0.07
ÁREA TOTAL	246.61	100.00


C. NÍVEL: 38470.76 m/l 8.85 ha 3.59 %

LEGENDA

- FAZENDA
- TALHÃO
- CURVA DE NÍVEL
- CARREADOR
- CONFRONTANTE
- REDE ELÉTRICA
- TRAJETO VAZIO
- TRAJETO CARREGADO


PLANTIO MANUAL - ESPAÇAMENTO: 1.50 X 1.50
TIRO MÉDIO ESTIMADO: 708.66m

Clealco
Açúcar, Etanol e Energia

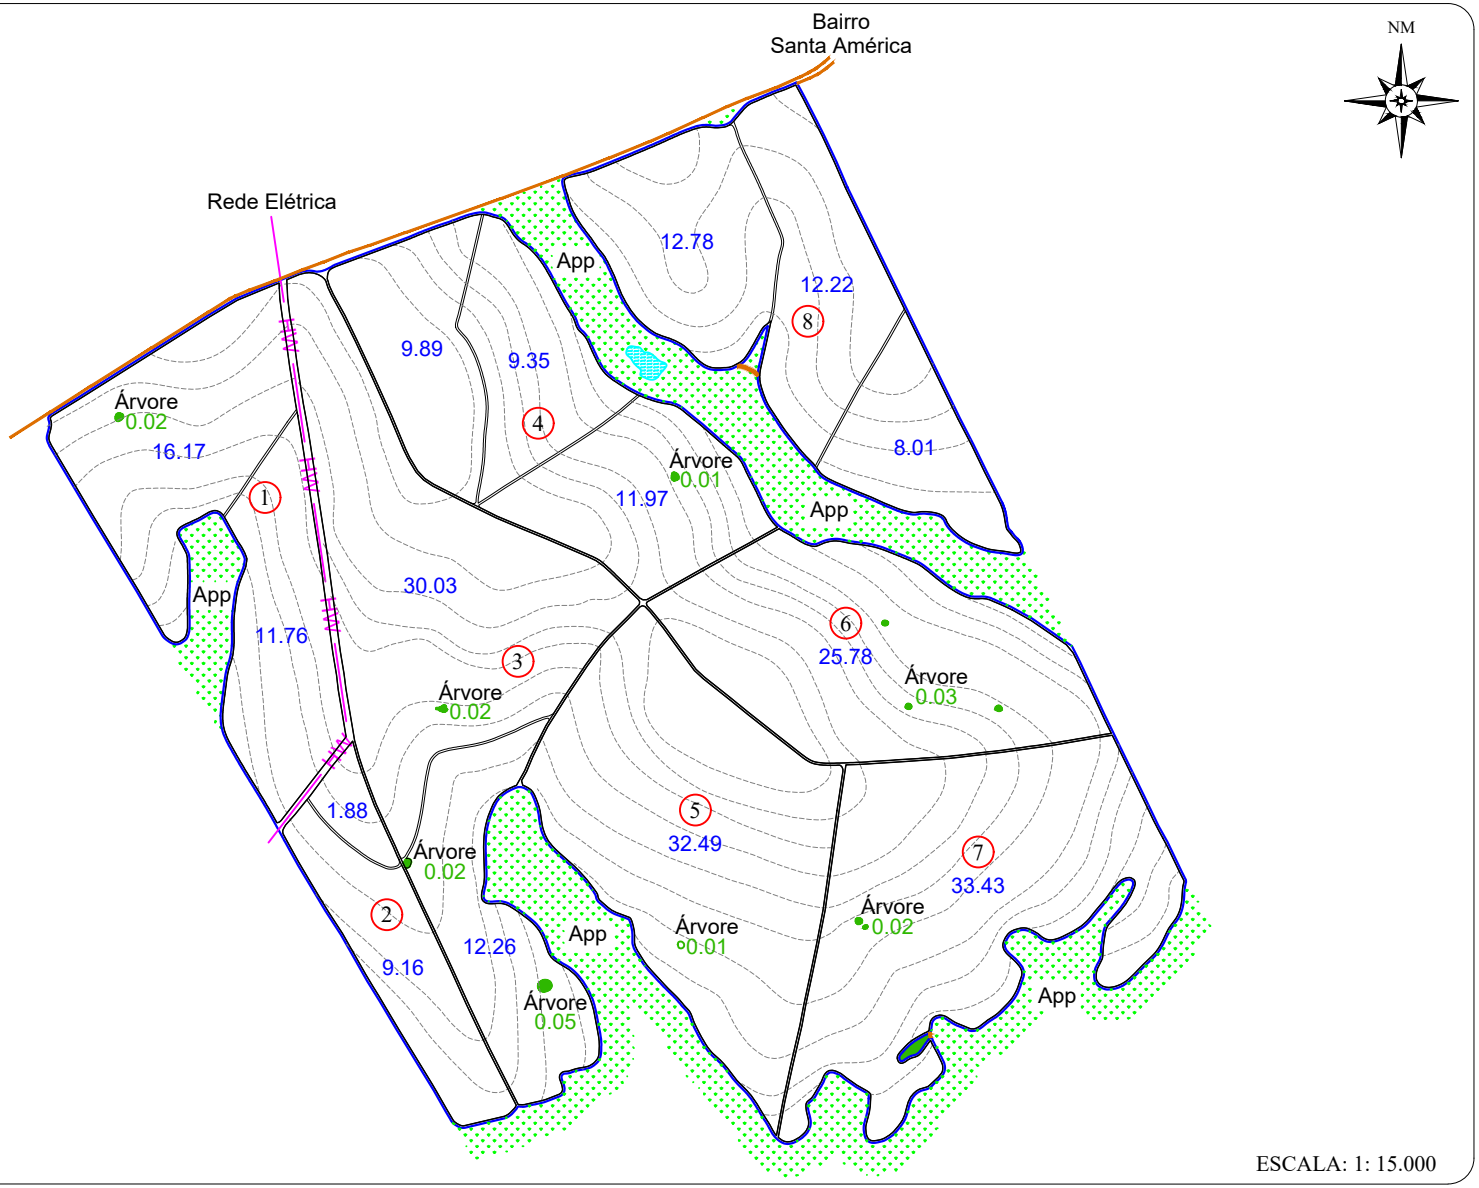

ESCALA: 1: 15.000

CROQUI DE ACESSO

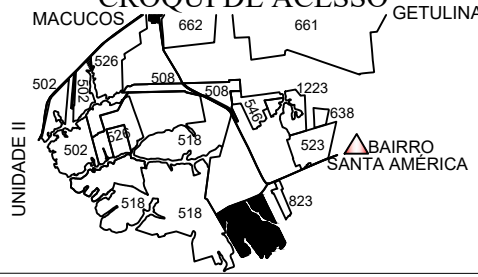

FAZENDA CANAA

PROPRIETÁRIO: WALDEMIR APARICIO CAPUTO
COMPRADOR: CLEALCO S/A
MUNICÍPIO: GETULINA - SP

DISTÂNCIAS (km):
UNID. I - Asfalto: 81.00 Terra.: 1.00
UNID.I I - Asfalto: 24.50 Terra.: 1.00
UNID. III -Asfalto: 62.00 Terra.: 1.00

COORDENADAS: E(X): 595709.53 N(Y): 7587246.76
LAT: -21°48'57.7572" LONG: -50°4'26.3580"

CLEALCO - AÇÚCAR E ALCOOL S/A - DEPARTAMENTO DE TOPOGRAFIA

UNIDADE: I
PARTE: A/A
FUNDO AGRÍCOLA: 307313

M:\01-Mapa de safra\Mapas Atualizados\Terceiro\307313 - Fazenda Canaa (Waldemir Aparicio Caputo)\307313 - Fazenda Canaa (Waldemir Aparicio Caputo).dwg

Fernanda Bezerra 31/10/22