ZONA DV	Nº TAL.	DATA PL.	ÁREA (ha)	VARIEDADE
999 5.87 %	1	06/2022	8.63	RB 975242
	2		41.34	
	3		32.14	
	4		23.49	
	5		17.76	
	6		29.47	
	7		18.15	
	8		4.95	
	9		13.15	
	10	04/2024	12.40	RB 127825
TOTAL PLANTIO			201.48	--------


ÁREAS	(ha)	(%)
PLANTIO	201.48	95.75
CARREADORES	5.56	2.64
OUTROS	0.00	0.00
SUB TOTAL AGRICULTÁVEL	207.04	98.40
AP.P.	0.00	0.00
ÁRVORES	0.90	0.43
OUTROS	2.47	1.17
SUB TOTAL NÃO AGRICULT.	3.37	1.60
ÁREA TOTAL	210.41	100.00

C. NÍVEL: 29961.60 m/l 6.89 ha 3.28 %

LEGENDA


- FAZENDA
- TALHÃO
- CURVA DE NÍVEL
- CARREADOR
- CONFRONTANTE
- REDE ELÉTRICA
- TRAJETO VAZIO
- TRAJETO CARREGADO

PLANTIO MANUAL - ESPAÇAMENTO: 1.50 X 1.50
TIRO MÉDIO ESTIMADO: 194.21 m

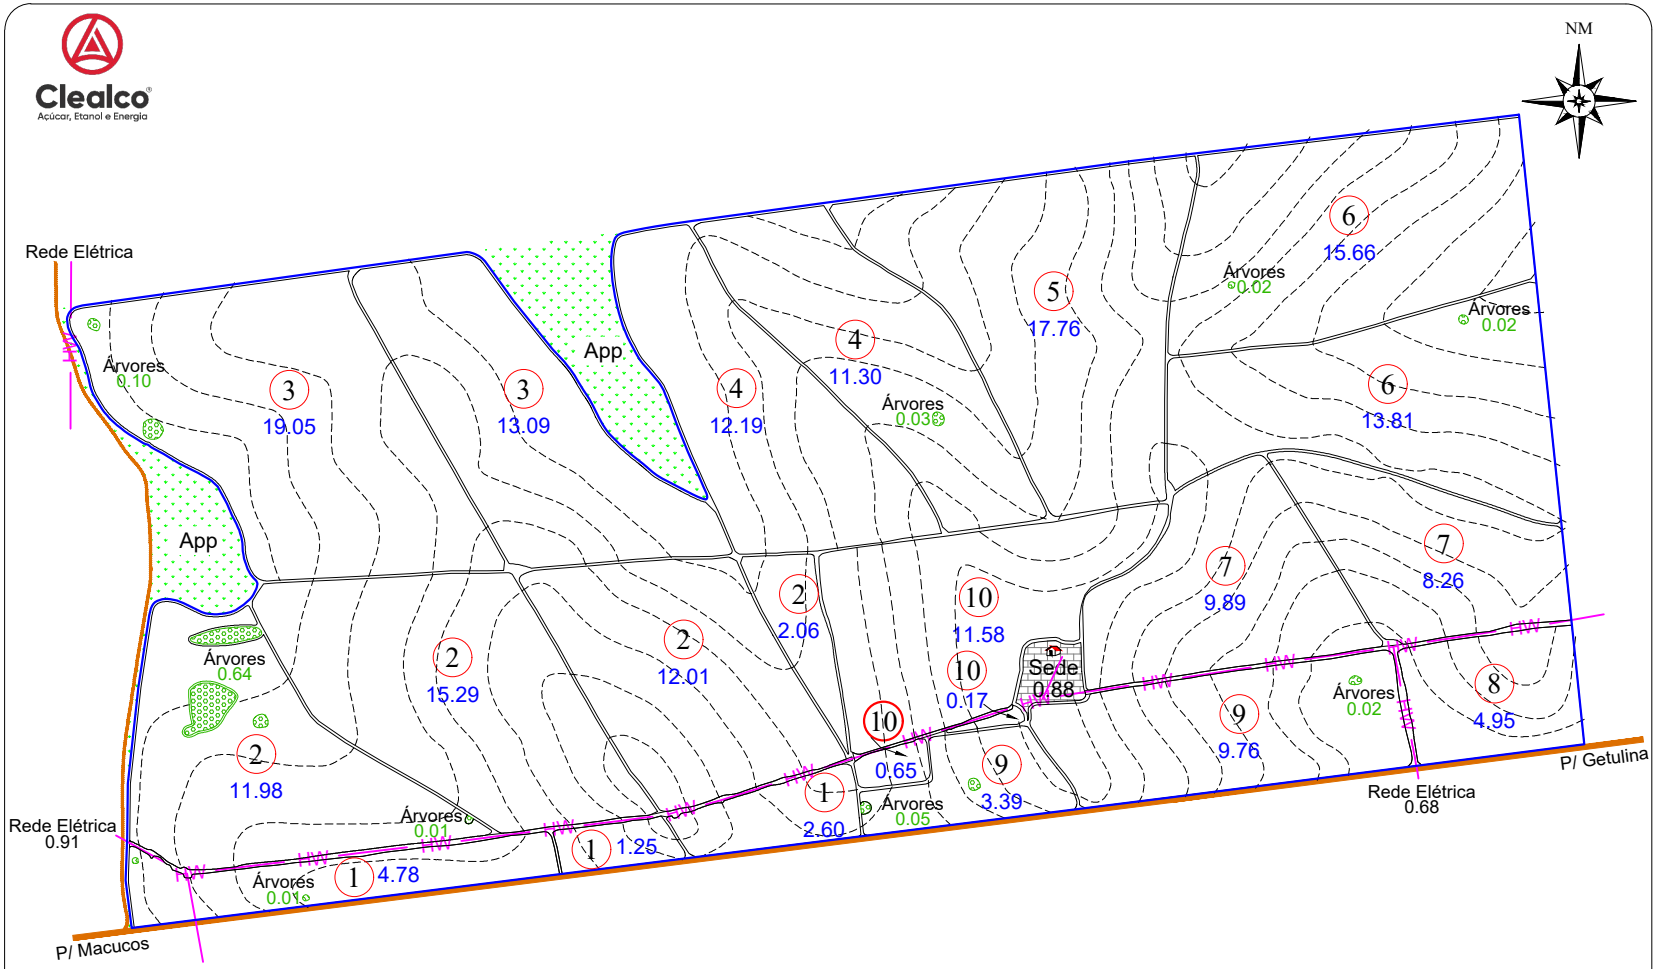

ESCALA: 1: 12.000

CROQUI DE ACESSO

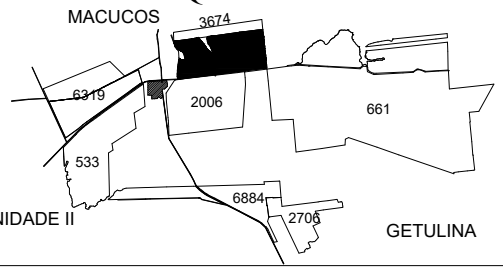

FAZENDA NOSSA SENHORA APARECIDA

PROPRIETÁRIO: JULIO CESAR RIOS DE BARROS
COMPRADOR: CLEALCO S/A
MUNICÍPIO: GETULINA

DISTÂNCIAS (km):
UNID. I - Asfalto: 72.00 Terra.: 2.50
UNID.I I - Asfalto: 16.00 Terra.: 2.50
UNID. III -Asfalto: 75.00 Terra.: 2.50

COORDENADAS: E(X): 594036.60 N(Y): 7595943.96
LAT: -21°44'15.2376" LONG: -50°5'26.4053"

CLEALCO - AÇÚCAR E ALCOOL S/A - DEPARTAMENTO DE TOPOGRAFIA

UNIDADE: I
PARTE: A/A
FUNDO AGRÍCOLA: 307314

M:\01-Mapa de safra\Mapas Atualizados\Terceiro\307314 - Fazenda Nossa Senhora Aparecida (Julio Cesar Rios de Barros)\307314 A - Fazenda Nossa Senhora Aparecida (Julio Cesar Rios de Barros).dwg

Bruno Gamboa 20/08/24