ZONA DV	Nº TAL.	DATA PL.	ÁREA (ha)	VARIEDADE
999	1	05/2022	31.39	RB 975242
4.72%	2		35.48	
TOTAL PLANTIO			66.87	--------

ÁREAS	(ha)	(%)
PLANTIO	66.87	95.38
CARREADORES	3.07	4.38
OUTROS	0.00	0.00
SUB TOTAL AGRICULTÁVEL	69.94	99.76
AP.P.	0.00	0.00
ÁRVORES	0.17	0.24
OUTROS	0.00	0.00
SUB TOTAL NÃO AGRICULT.	0.17	0.24
ÁREA TOTAL	70.11	100.00

C. NÍVEL:	7715.28 m/l	1.77 ha	2.53 %

LEGENDA

FAZENDA	CONFRONTANTE
TALHÃO	REDE ELÉTRICA
CURVA DE NÍVEL	TRAJETO VAZIO
CARREADOR	TRAJETO CARREGADO

PLANTIO MANUAL - ESPAÇAMENTO: 1.50 X 1.50
TIRO MÉDIO ESTIMADO: 300.59m

Clealco
Açúcar, Etanol e Energia

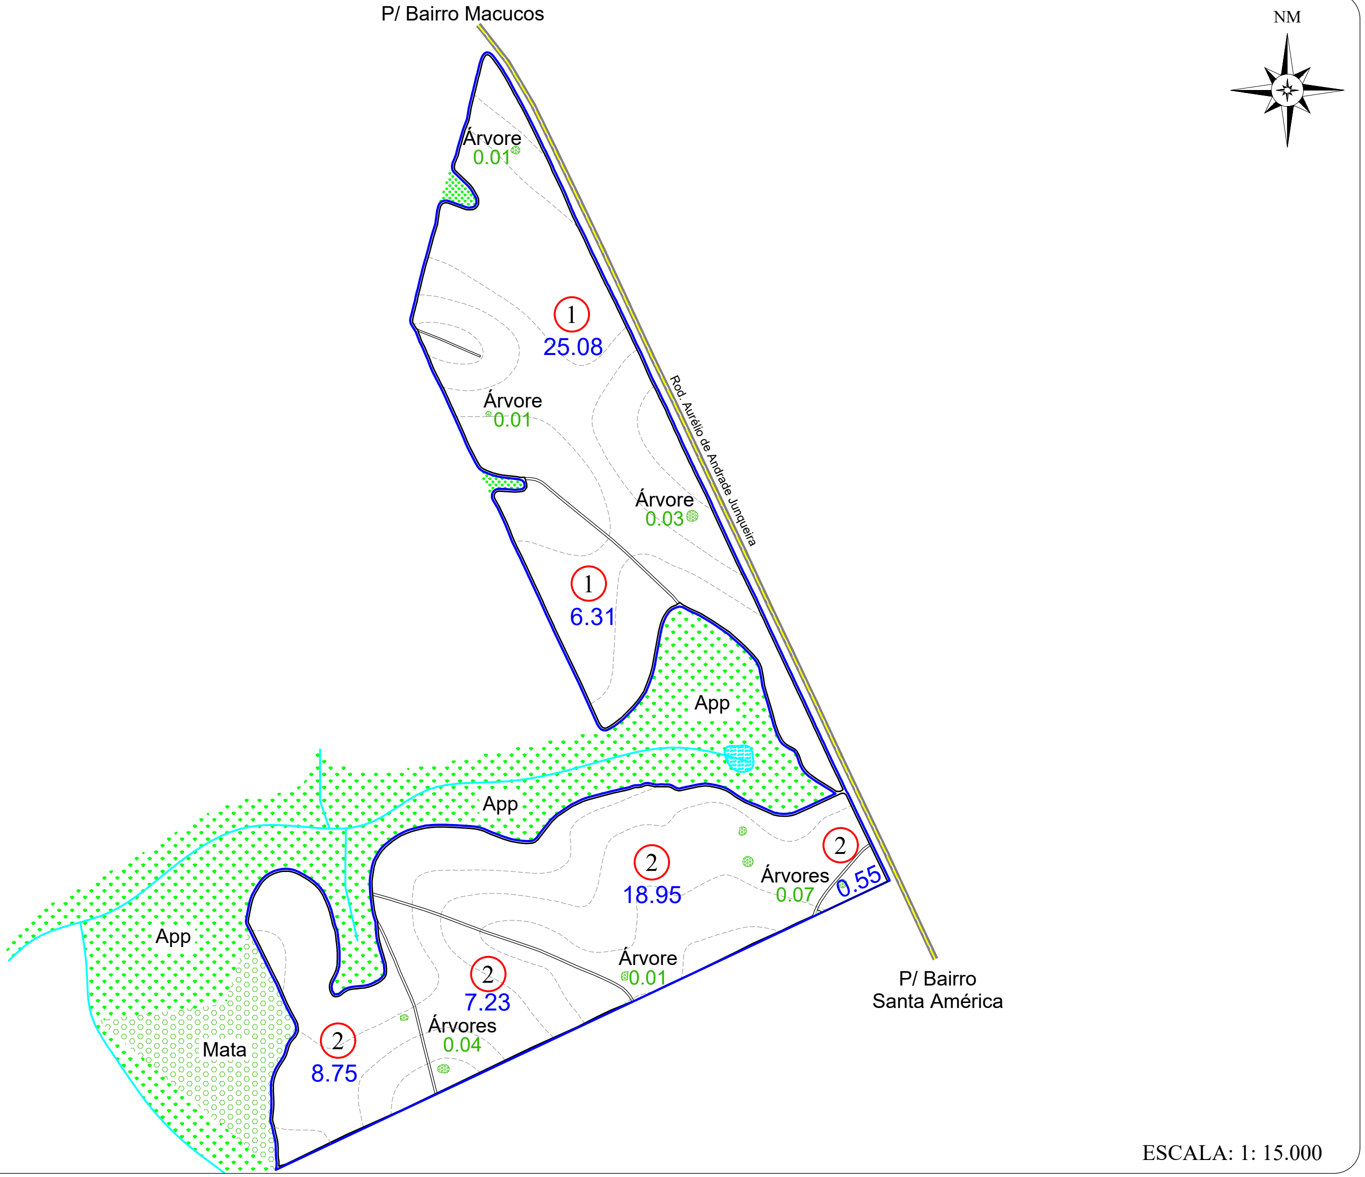

ESCALA: 1: 15.000

CROQUI DE ACESSO

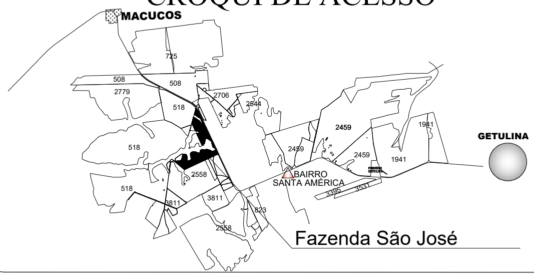

SÍTIO SÃO JOSÉ

PROPRIETÁRIO: WALDEMIR APARICIO CAPUTO
COMPRADOR: CLEALCO S/A
MUNICÍPIO: GETULINA - SP

DISTÂNCIAS (km):

UNID. I -	Asfalto:	81.00	Terra.:	1.00
UNID.I I -	Asfalto:	24.50	Terra.:	1.00
UNID. III -	Asfalto:	62.00	Terra.:	1.00

COORDENADAS: E(X): 595235.18 N(Y): 7590519.56
LAT: -21°47'11.4147" LONG: -50°4'43.5588"

CLEALCO - AÇÚCAR E ALCOOL S/A - DEPARTAMENTO DE TOPOGRAFIA

UNIDADE:
I

PARTE:
A/A

FUNDO AGRÍCOLA:
307321

M:\01-Mapa de safra\Mapas Atualizados\Terceiro\307321 - Sìtio São José (Waldemir Aparicio Caputo)\307321 - Sìtio São José (Waldemir Aparicio Caputo).dwg

Fernanda Bezerra 18/10/22