ZONA DV	Nº TAL.	DATA PL.	ÁREA (ha)	VARIEDADE
999 4.36%	1	05/2022	45.87	RB 975242
	2		41.01	
	3		26.57	
	4		20.49	
	5	06/2023	42.38	
TOTAL PLANTIO			176.32	--------


ÁREAS	(ha)	(%)
PLANTIO	176.32	96.38
CARREADORES	5.80	3.17
OUTROS	0.00	0.00
SUB TOTAL AGRICULTÁVEL	182.12	99.56
AP.P.	0.00	0.00
ÁRVORES	0.81	0.44
OUTROS	0.00	0.00
SUB TOTAL NÃO AGRICULT.	0.81	0.44
ÁREA TOTAL	182.93	100.00

C. NÍVEL: 19618.30 m/l 4.51 ha 2.47 %


LEGENDA

- FAZENDA
- TALHÃO
- CURVA DE NÍVEL
- CARREADOR
- CONFRONTANTE
- REDE ELÉTRICA
- TRAJETO VAZIO
- TRAJETO CARREGADO

PLANTIO MANUAL - ESPAÇAMENTO: 1.50 X 1.50
TIRO MÉDIO ESTIMADO: 526.20m

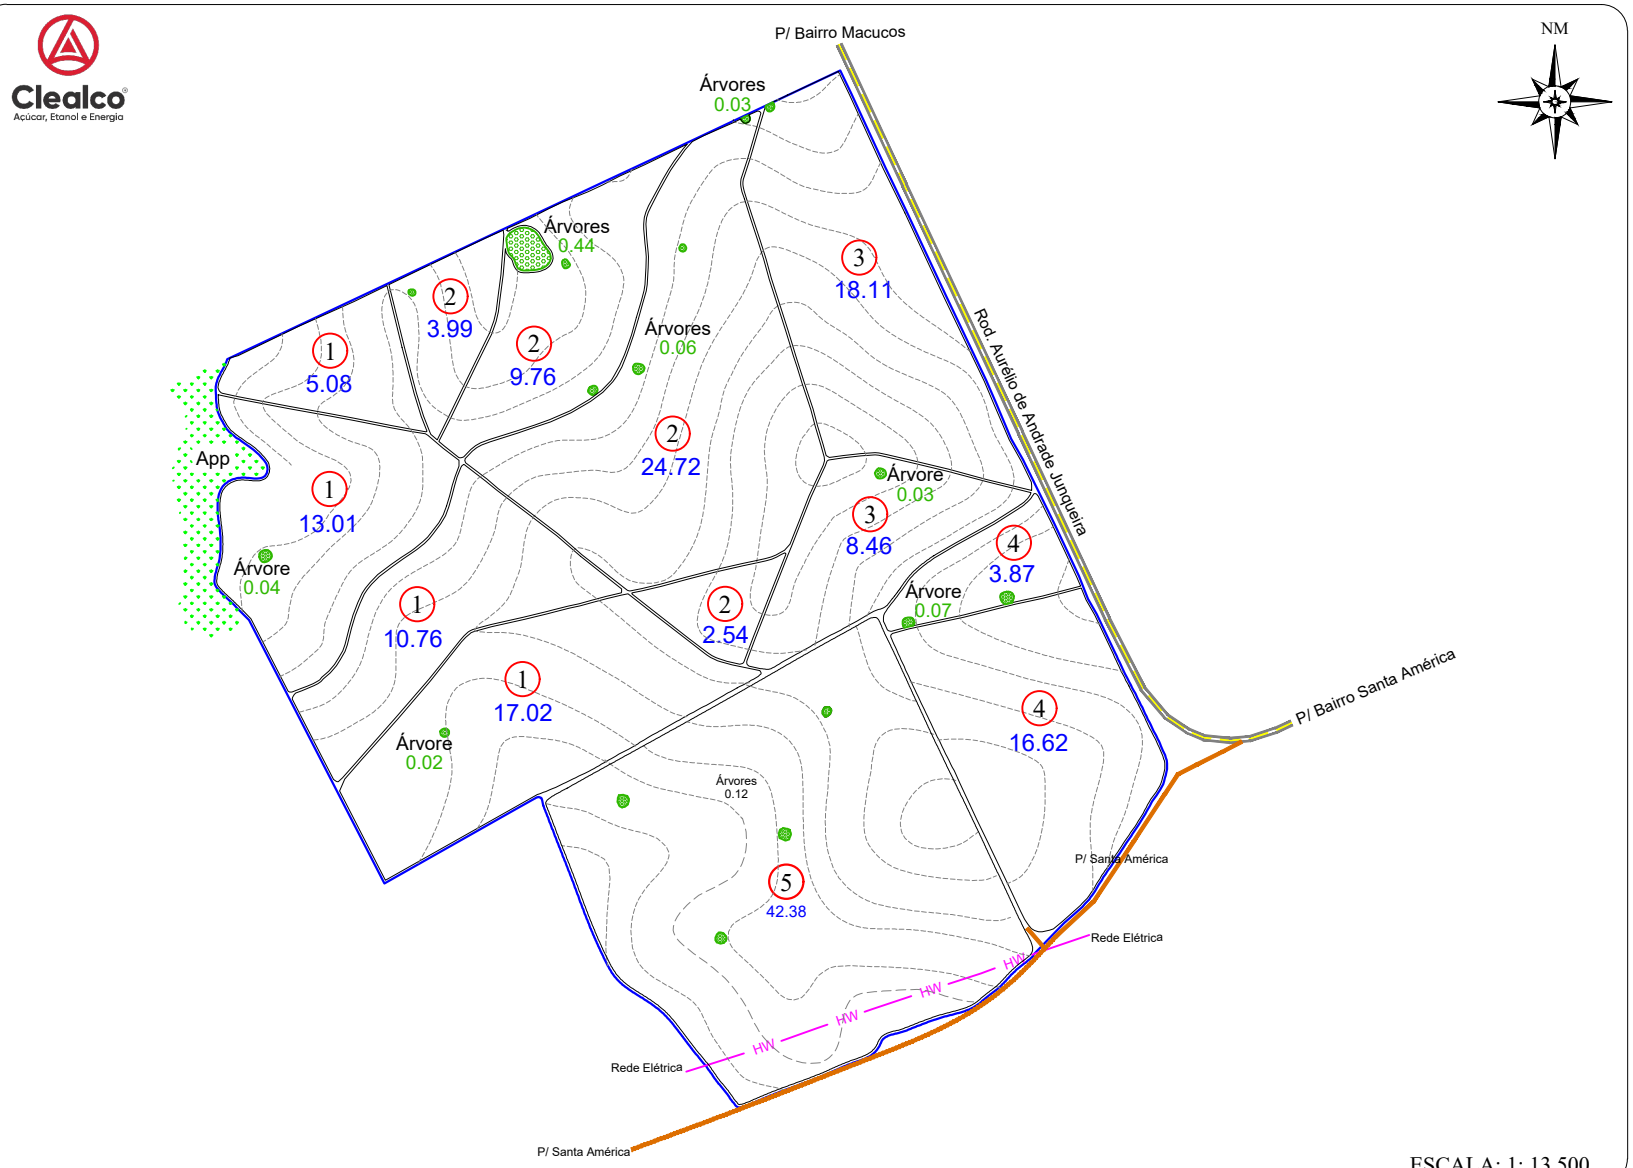

CROQUI DE ACESSO

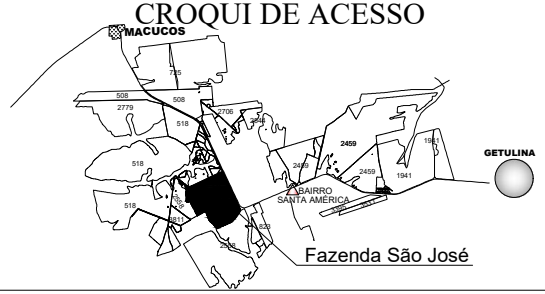

FAZENDA SÃO JOSÉ

PROPRIETÁRIO: WALDEMIR APARICIO CAPUTO
COMPRADOR: CLEALCO S/A
MUNICÍPIO: GETULINA - SP

DISTÂNCIAS (km):

UNID. I -	Asfalto:	80.00	Terra.:	2.50
UNID.I I -	Asfalto:	22.00	Terra.:	2.50
UNID. III -	Asfalto:	72.00	Terra.:	2.50

COORDENADAS: E(X): 595361.96 N(Y): 7589293.04
LAT: -21°47'51.2780" LONG: -50°4'38.8890"

CLEALCO - AÇÚCAR E ALCOOL S/A - DEPARTAMENTO DE TOPOGRAFIA

UNIDADE: II
PARTE: A/A
FUNDO AGRÍCOLA: 307323

Bruno Gamboa 17/07/24