ZONA D.V.	Nº TAL.	DATA PL.	ÁREA (ha)	VAR.
999 3.45 %	1	05/2022	9.19	RB 966928
	2		16.91	
	3		33.00	
	4		23.84	
	5		16.71	
	6		21.35	
	7		29.10	
	8		13.11	
	9		17.58	
TOTAL PLANTIO			180.79	--------


ÁREAS	(ha)	(%)
PLANTIO	180.79	95.92
CARREADORES	7.06	3.74
OUTROS	0.00	0.00
SUB TOTAL AGRICULTÁVEL	187.85	99.66
AP.P.	0.00	0.00
ÁRVORES	0.48	0.26
OUTROS	0.16	0.08
SUB TOTAL NÃO AGRICULT.	0.64	0.34
ÁREA TOTAL	188.49	100.00

C. NÍVEL: 11473.52 m/l 2.64 ha 1.40 %


LEGENDA

- FAZENDA
- TALHÃO
- CURVA DE NÍVEL
- CARREADOR
- CONFRONTANTE
- REDE ELÉTRICA
- TRAJETO VAZIO
- TRAJETO CARREGADO

PLANTIO MANUAL - ESPAÇAMENTO: 1.50 X 1.50
TIRO MÉDIO ESTIMADO: 000.00m

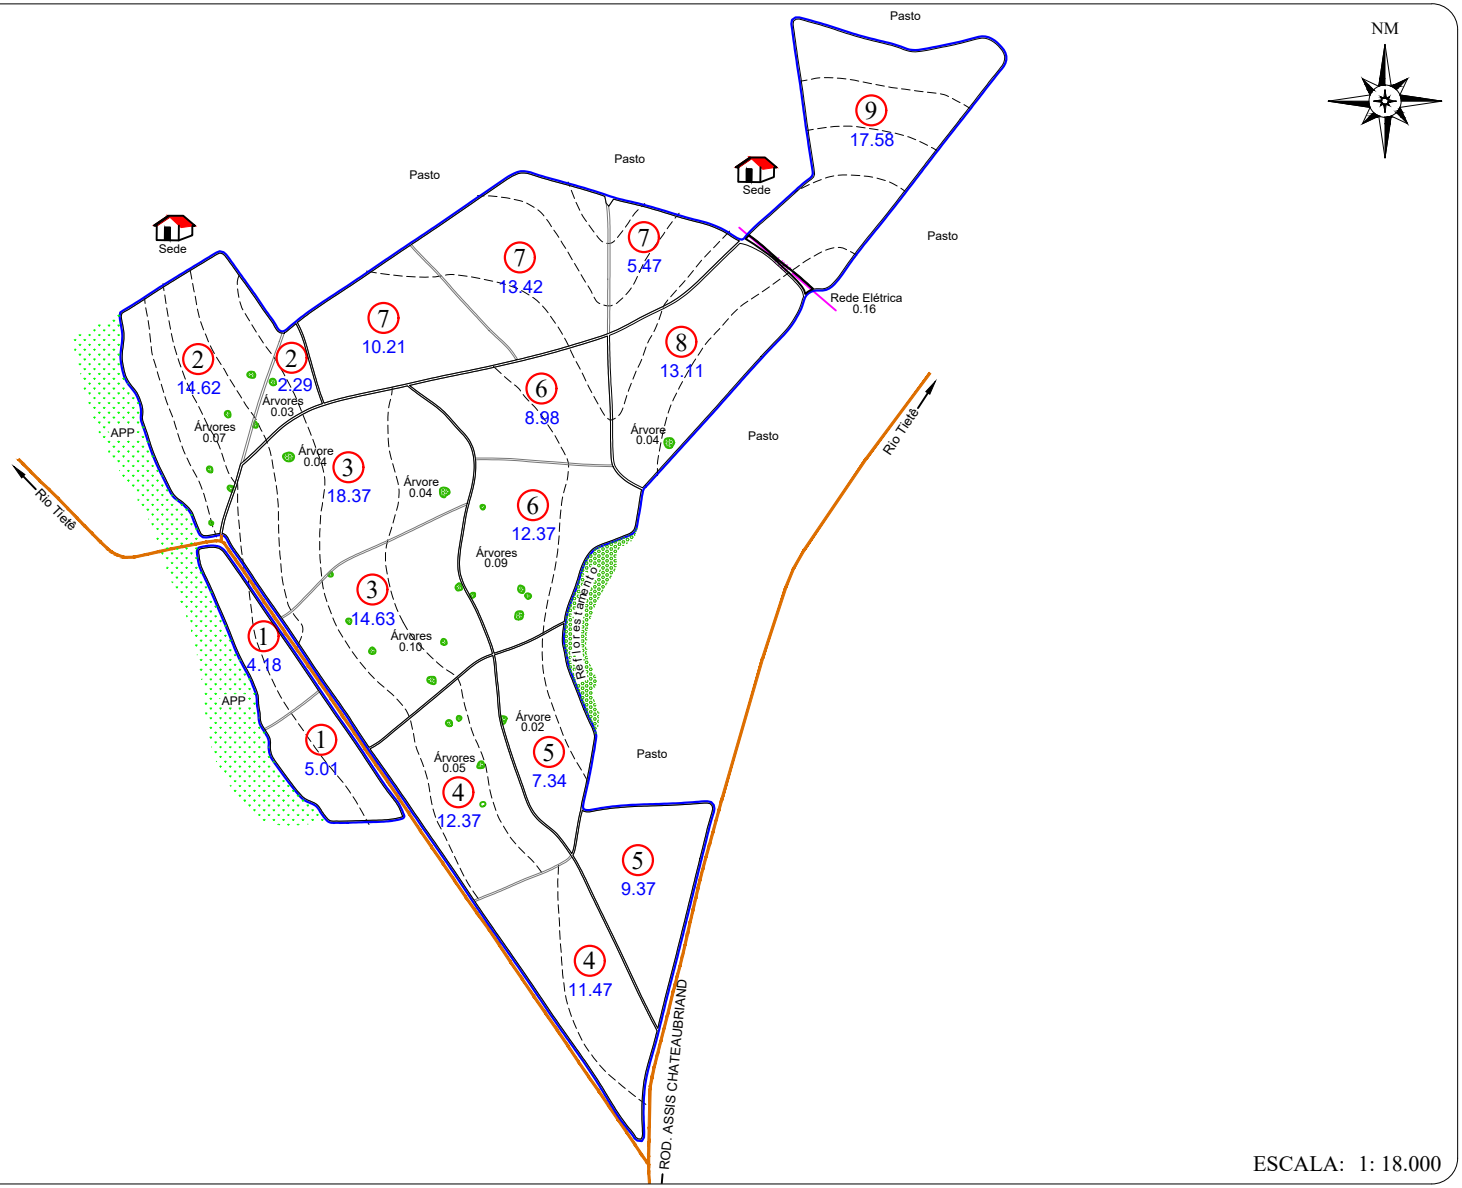

CROQUI DE ACESSO

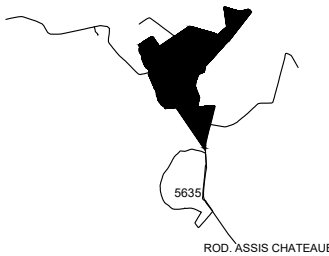

FAZENDA SÃO JOSÉ DA BELA VISTA

PROPRIETÁRIO: LEANDRO INOCÊNCIO TORREZAN
COMPRADOR: CLEALCO S/A
MUNICÍPIO: PENÁPOLIS

DISTÂNCIAS (km):

UNID. I - Asfalto:	47.00	Terra.:	6.00
UNID.I I - Asfalto:	74.00	Terra.:	6.00
UNID. III -Asfalto:	13.00	Terra.:	6.00

COORDENADAS: E(X): 596088.27 N(Y): 7646539.63
LAT: -21°16'49.3642" LONG: -50°4'25.4300"

CLEALCO - AÇÚCAR E ALCOOL S/A - DEPARTAMENTO DE TOPOGRAFIA

UNIDADE: I
PARTE: A/A
FUNDO AGRÍCOLA: 307326

M:\01-Mapa de safra\Mapas Atualizados\Terceiro\307326 - Fazenda São João da bela vista (Leandro Inocencio Torrezan)\307326 - Fazenda São João da bela vista (Leandro Inocencio Torrezan).dwg

Peterson Santos 10/01/23