| ZONA D.V. | Nº TAL. | DATA PL. | ÁREA (ha) | VAR. |
|---|---|---|---|---|
| 999 | 1 | 06/2022 | 10.43 | RB975242 |
| 2.68 % | 2 | | 6.33 | |
| | | | | |
| | | | | |
| TOTAL PLANTIO | | | 16.76 | -------- |

| ÁREAS | (ha) | (%) |
|---|---|---|
| PLANTIO | 16.76 | 90.19 |
| CARREADORES | 1.77 | 9.54 |
| OUTROS | 0.00 | 0.00 |
| SUB TOTAL AGRICULTÁVEL | 18.53 | 99.73 |
| AP.P. | 0.00 | 0.00 |
| ÁRVORES | 0.02 | 0.11 |
| OUTROS | 0.03 | 0.16 |
| SUB TOTAL NÃO AGRICULT. | 0.05 | 0.27 |
| ÁREA TOTAL | 18.58 | 100.00 |

| | | | |
|---|---|---|---|
| C. NÍVEL: | 643.73 m/l | 0.15 ha | 0.80 % |

## LEGENDA

| | |
|---|---|
| ▬ FAZENDA | ▬ CONFRONTANTE |
| ▬ TALHÃO | ▬ REDE ELÉTRICA |
| ▬ CURVA DE NÍVEL | —▷ TRAJETO VAZIO |
| — CARREADOR | —► TRAJETO CARREGADO |

PLANTIO MANUAL - ESPAÇAMENTO: 1.50 X 1.50

Clealco®
Açúcar, Etanol e Energia

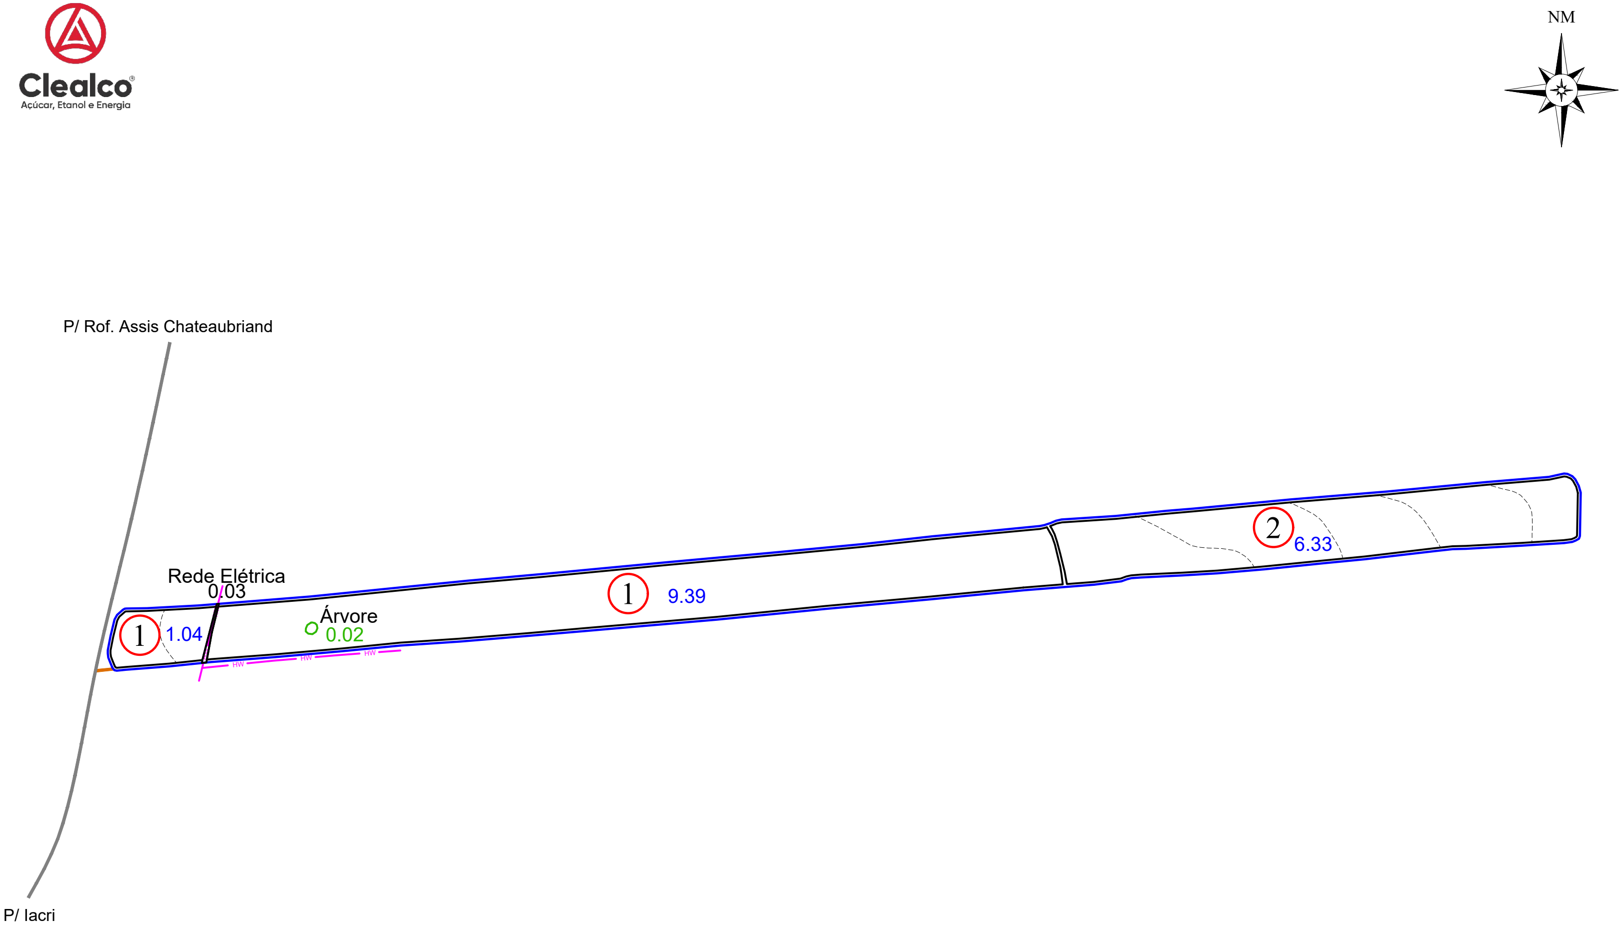

ESCALA: 1: 11.000

## CROQUI DE ACESSO

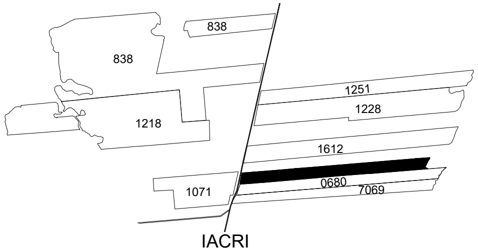

# SÍTIO SÃO CAETANO

| | | | | | | |
|---|---|---|---|---|---|---|
| PROPRIETÁRIO: | VINICIUS STEFANELLI | DISTÂNCIAS (km): | | | | |
| | | UNID. I - | Asfalto: | 42.00 | Terra.: | 1.00 |
| COMPRADOR: | CLEALCO S/A | UNID.I I - | Asfalto: | 76.50 | Terra.: | 1.00 |
| MUNICÍPIO: | IACRI - SP | UNID. III - | Asfalto: | 0.00 | Terra.: | 0.00 |

| | | | | |
|---|---|---|---|---|
| COORDENADAS: | E(X): | 542094.50 | N(Y): | 7596188.09 |
| | LAT: | -21°44'14.4856" | LONG: | -50°35'34.5760" |

CLEALCO - AÇÚCAR E ALCOOL S/A - DEPARTAMENTO DE TOPOGRAFIA

UNIDADE:
I

PARTE:
A/A

FUNDO AGRÍCOLA:
307328

M:\01-Mapa de safra\Mapas Atualizados\Terceiro\307328 - Sito Sao Caetano (Vinicius Stefanelli)\307328 - Sito Sao Caetano (Vinicius Stefanelli).dwg

Peterson Santos 27/12/22