ZONA D.V.	Nº TAL.	DATA PL.	ÁREA (ha)	VAR.
999 4.48 %	1	06/2022	23.09	RB867515
TOTAL PLANTIO			23.09	--------

ÁREAS	(ha)	(%)
PLANTIO	23.09	95.81
CARREADORES	1.00	4.15
OUTROS	0.00	0.00
SUB TOTAL AGRICULTÁVEL	24.09	99.96
AP.P.	0.00	0.00
ÁRVORES	0.01	0.04
OUTROS	0.00	0.00
SUB TOTAL NÃO AGRICULT.	0.01	0.04
ÁREA TOTAL	24.10	100.00

C. NÍVEL:	3597.90 m/l	0.83 ha	3.43 %

LEGENDA

▬	FAZENDA	▬	CONFRONTANTE
▬	TALHÃO	🟩	REDE ELÉTRICA
▬	CURVA DE NÍVEL	⇨	TRAJETO VAZIO
—	CARREADOR	→	TRAJETO CARREGADO

PLANTIO MANUAL - ESPAÇAMENTO: 1.50 X 1.50
TIRO MÉDIO ESTIMADO: 000.00m

Clealco
Açúcar, Etanol e Energia

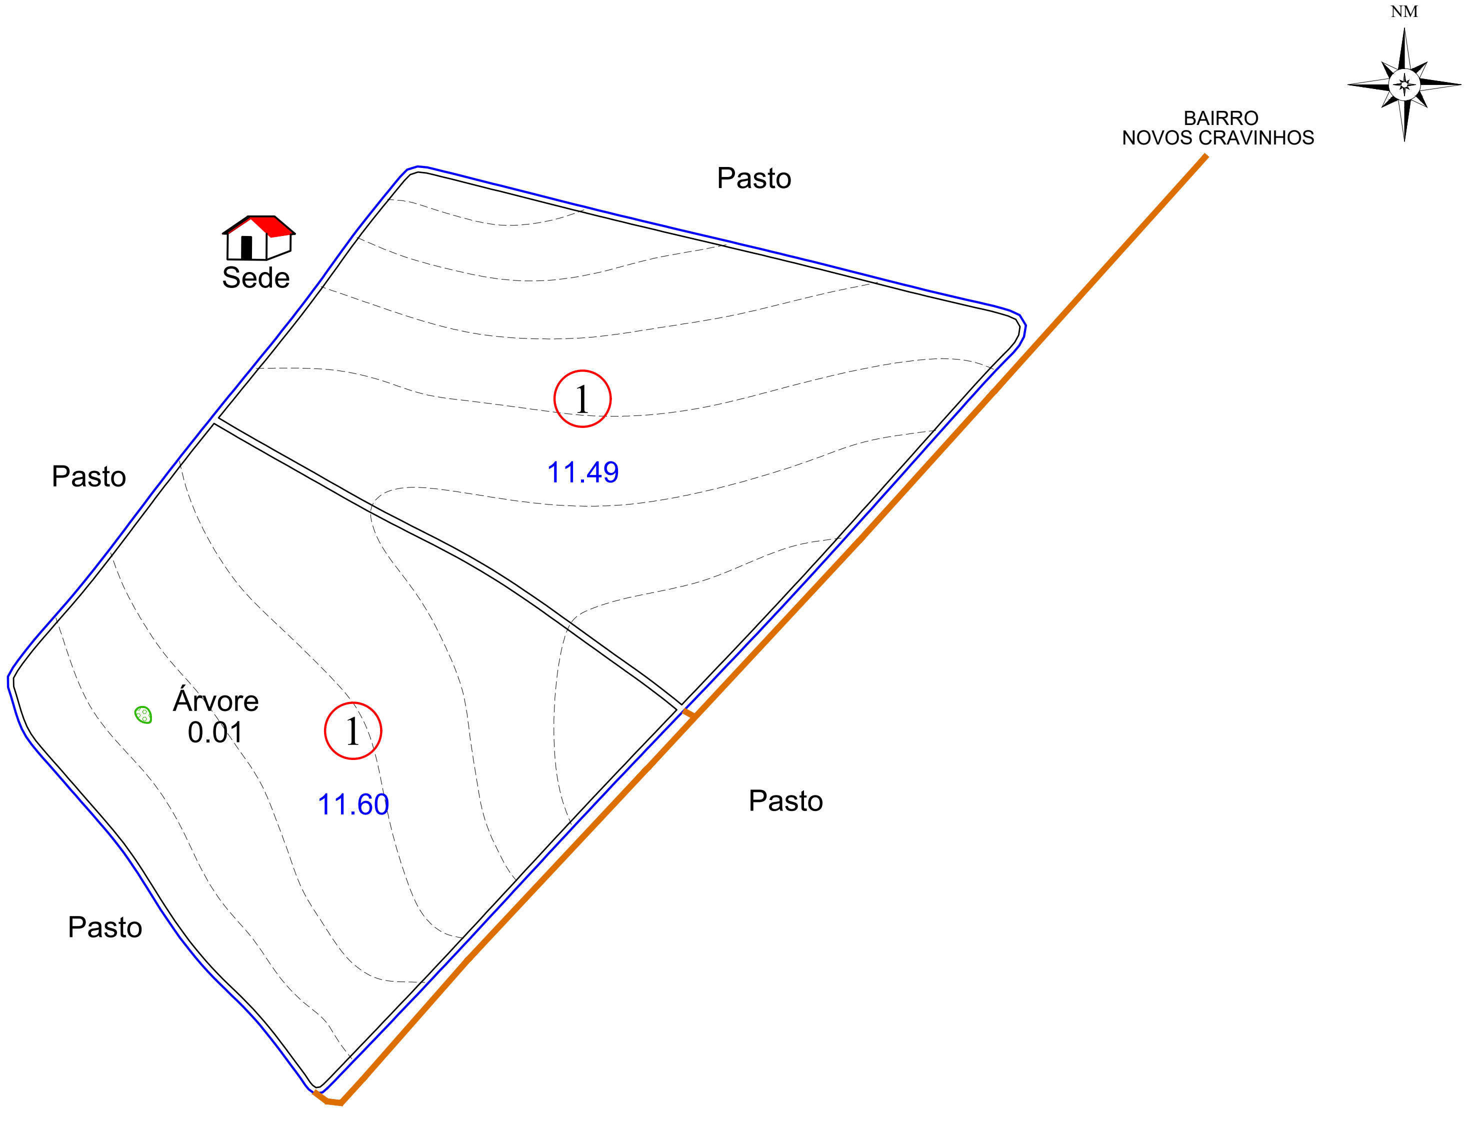
NM
BAIRRO
NOVOS CRAVINHOS
Pasto
Sede
Pasto
1
11.49
Árvore
0.01
1
11.60
Pasto
Pasto

ESCALA: 1: 5.500

CROQUI DE ACESSO

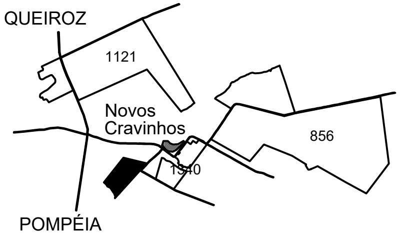
QUEIROZ
1121
Novos
Cravinhos
856
1340
POMPÉIA

SÍTIO SÃO PEDRO

PROPRIETÁRIO:	JORGE LUIZ GILBERTO
COMPRADOR:	CLEALCO S/A
MUNICÍPIO:	POMPÉIA

DISTÂNCIAS (km):

UNID. I -	Asfalto:	84.50	Terra.:	2.50
UNID.I I -	Asfalto:	24.50	Terra.:	2.50
UNID. III -	Asfalto:	78.00	Terra.:	2.50

COORDENADAS:		
	E(X): 590835.6325	N(Y): 7567933.956
	LAT: 21º 59' 26"	LONG: 50º 07' 12"

CLEALCO - AÇÚCAR E ALCOOL S/A - DEPARTAMENTO DE TOPOGRAFIA

UNIDADE:
II

PARTE:
A/A

FUNDO AGRÍCOLA:
307333

M:\01-Mapa de safra\Mapas Atualizados\Terceiro\307333 - Sítio São Pedro (Jorge Luis Gilberto)\307333 - Sítio São Pedro (Jorge Luis Gilberto).dwg

Peterson Santos 27/12/22