ZONA DV	Nº TAL.	DATA PL.	ÁREA (ha)	VARIEDADE
999 5.04%	1	05/2022	22.96	RB 975242
TOTAL PLANTIO			22.96	--------

ÁREAS	(ha)	(%)
PLANTIO	22.96	91.34
CARREADORES	1.75	6.95
OUTROS	0.00	0.00
SUB TOTAL AGRICULTÁVEL	24.71	98.29
AP.P.	0.34	1.35
ÁRVORES	0.03	0.12
OUTROS	0.06	0.24
SUB TOTAL NÃO AGRICULT.	0.43	1.71
ÁREA TOTAL	25.14	100.00

C. NÍVEL: 0.00 m/l 0.00 ha 0.00 %

LEGENDA

FAZENDA	CONFRONTANTE
TALHÃO	REDE ELÉTRICA
CURVA DE NÍVEL	TRAJETO VAZIO
CARREADOR	TRAJETO CARREGADO

PLANTIO MANUAL - ESPAÇAMENTO: 1.50 X 1.50
TIRO MÉDIO ESTIMADO: 313.13 m

Clealco®
Açúcar, Etanol e Energia

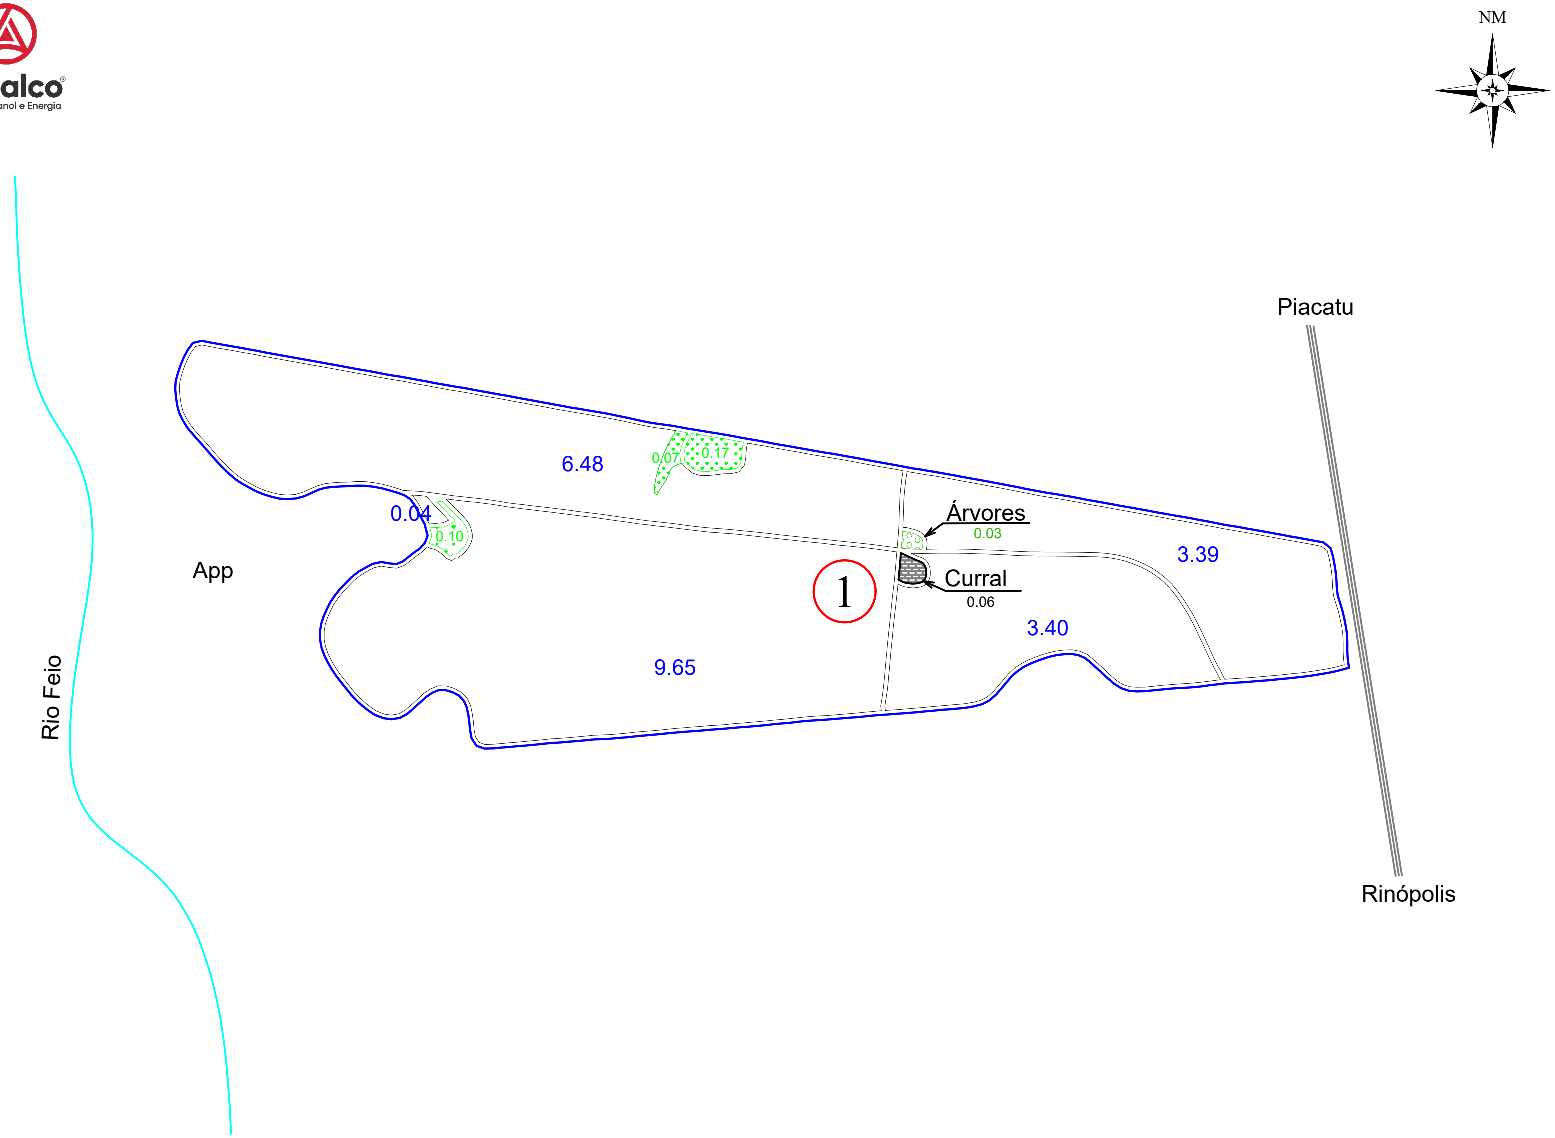

ESCALA: 1: 8.000

CROQUI DE ACESSO

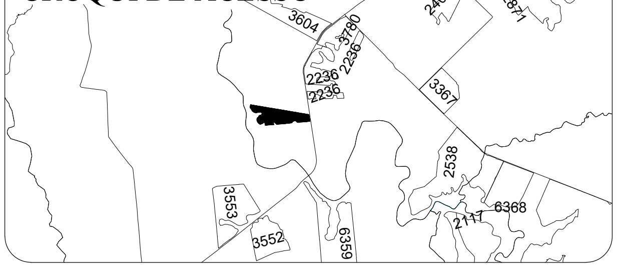

SÍTIO SÃO LUIZ

PROPRIETÁRIO: RAFAEL BRIGATTI
ARRENDATÁRIO: CLEALCO S/A
MUNICÍPIO: PIACATU

DISTÂNCIAS (km):

UNID. I -	Asfalto:	26.00	Terra.:	4.00
UNID.I I -	Asfalto:	62.00	Terra.:	1.50
UNID. III -	Asfalto:	61.00	Terra.:	4.00

COORDENADAS: E(X): 537695.8990 N(Y): 7607699.0054
LAT: 21°38'00,18063" LONG: 50° 38' 08,64740"

CLEALCO - AÇÚCAR E ALCOOL S/A - DEPARTAMENTO DE TOPOGRAFIA

UNIDADE:
I
PARTE:
A/A
FUNDO AGRÍCOLA:
307337

M:\01-Mapa de safra\Mapas Atualizados\Terceiro\307337 - Sitio São Luiz I (Rafael Brigatti)\307337 - Sitio São Luiz I (Rafael Brigatti).dwg

Peterson Santos 21/07/2022