ZONA DV	Nº TAL.	DATA PL.	ÁREA (ha)	VARIEDADE
999	1	06/2022	5.49	RB975242
6.33%	2		32.28	
TOTAL PLANTIO			37.77	--------

ÁREAS	(ha)	(%)
PLANTIO	37.77	96.20
CARREADORES	1.49	3.80
OUTROS	0.00	0.00
SUB TOTAL AGRICULTÁVEL	39.26	100.00
AP.P.	0.00	0.00
ÁRVORES	0.00	0.00
OUTROS	0.00	0.00
SUB TOTAL NÃO AGRICULT.	0.00	0.00
ÁREA TOTAL	39.26	100.00

C. NÍVEL:	3925.01 m/l	0.90 ha	2.30 %

LEGENDA

FAZENDA	CONFRONTANTE
TALHÃO	REDE ELÉTRICA
CURVA DE NÍVEL	TRAJETO VAZIO
CARREADOR	TRAJETO CARREGADO

PLANTIO MANUAL - ESPAÇAMENTO: 1.50 X 1.50
TIRO MÉDIO ESTIMADO: 418,56 m

CLEALCO
AÇÚCAR E ÁLCOOL S.A.

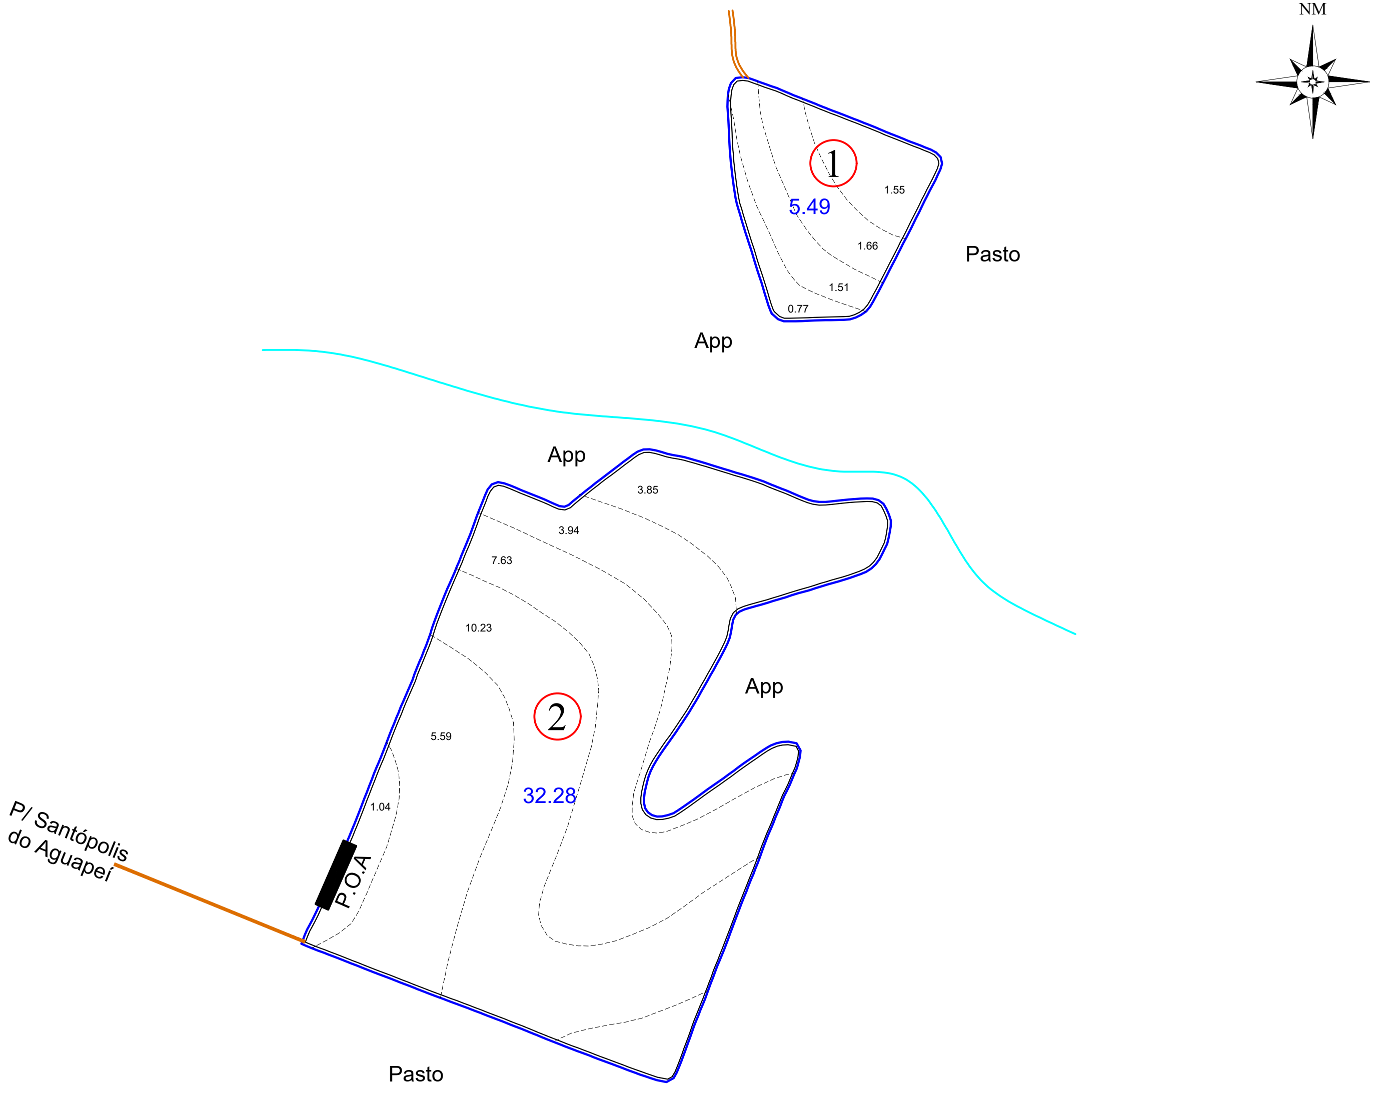
NM
1
5.49
1.55
1.66
1.51
0.77
Pasto
App
App
3.85
3.94
7.63
10.23
2
5.59
32.28
1.04
P.O.A
App
P/ Santópolis do Aguapei
Pasto

ESCALA: 1: 10.000

CROQUI DE ACESSO

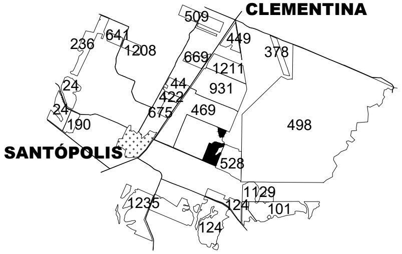
CLEMENTINA
509
236
641
1208
449
378
669
1211
44
422
931
24
24
675
469
190
498
SANTÓPOLIS
528
1129
1235
124
101
124

SÍTIO CERES

PROPRIETÁRIO: DOUGLAS IMAR MENANI
COMPRADOR: CLEALCO S/A
MUNICÍPIO: SANTOPOLIS DO AGUAPEI

DISTÂNCIAS (km):

	Asfalto:		Terra.:	
UNID. I -	Asfalto:	11.00	Terra.:	1.50
UNID.I I -	Asfalto:	48.00	Terra.:	1.50
UNID. III -	Asfalto:	67.00	Terra.:	1.50

COORDENADAS: E(X): 553987 N(Y): 7607384
LAT: 21° 38' 09,18450" LONG: 50° 28' 41,88854"

CLEALCO - AÇÚCAR E ALCOOL S/A - DEPARTAMENTO DE TOPOGRAFIA

UNIDADE:
I

PARTE:
A/A

FUNDO AGRÍCOLA:
307351

M:\01-Mapa de safra\Mapas Atualizados\Terceiro\307351 - Sítio Ceres (Douglas Omar Manani)\307351 - Sítio Ceres (Douglas Omar Manani).dwg

Peterson Santos 26/07/2022