
Clealco
Açúcar, Etanol e Energia

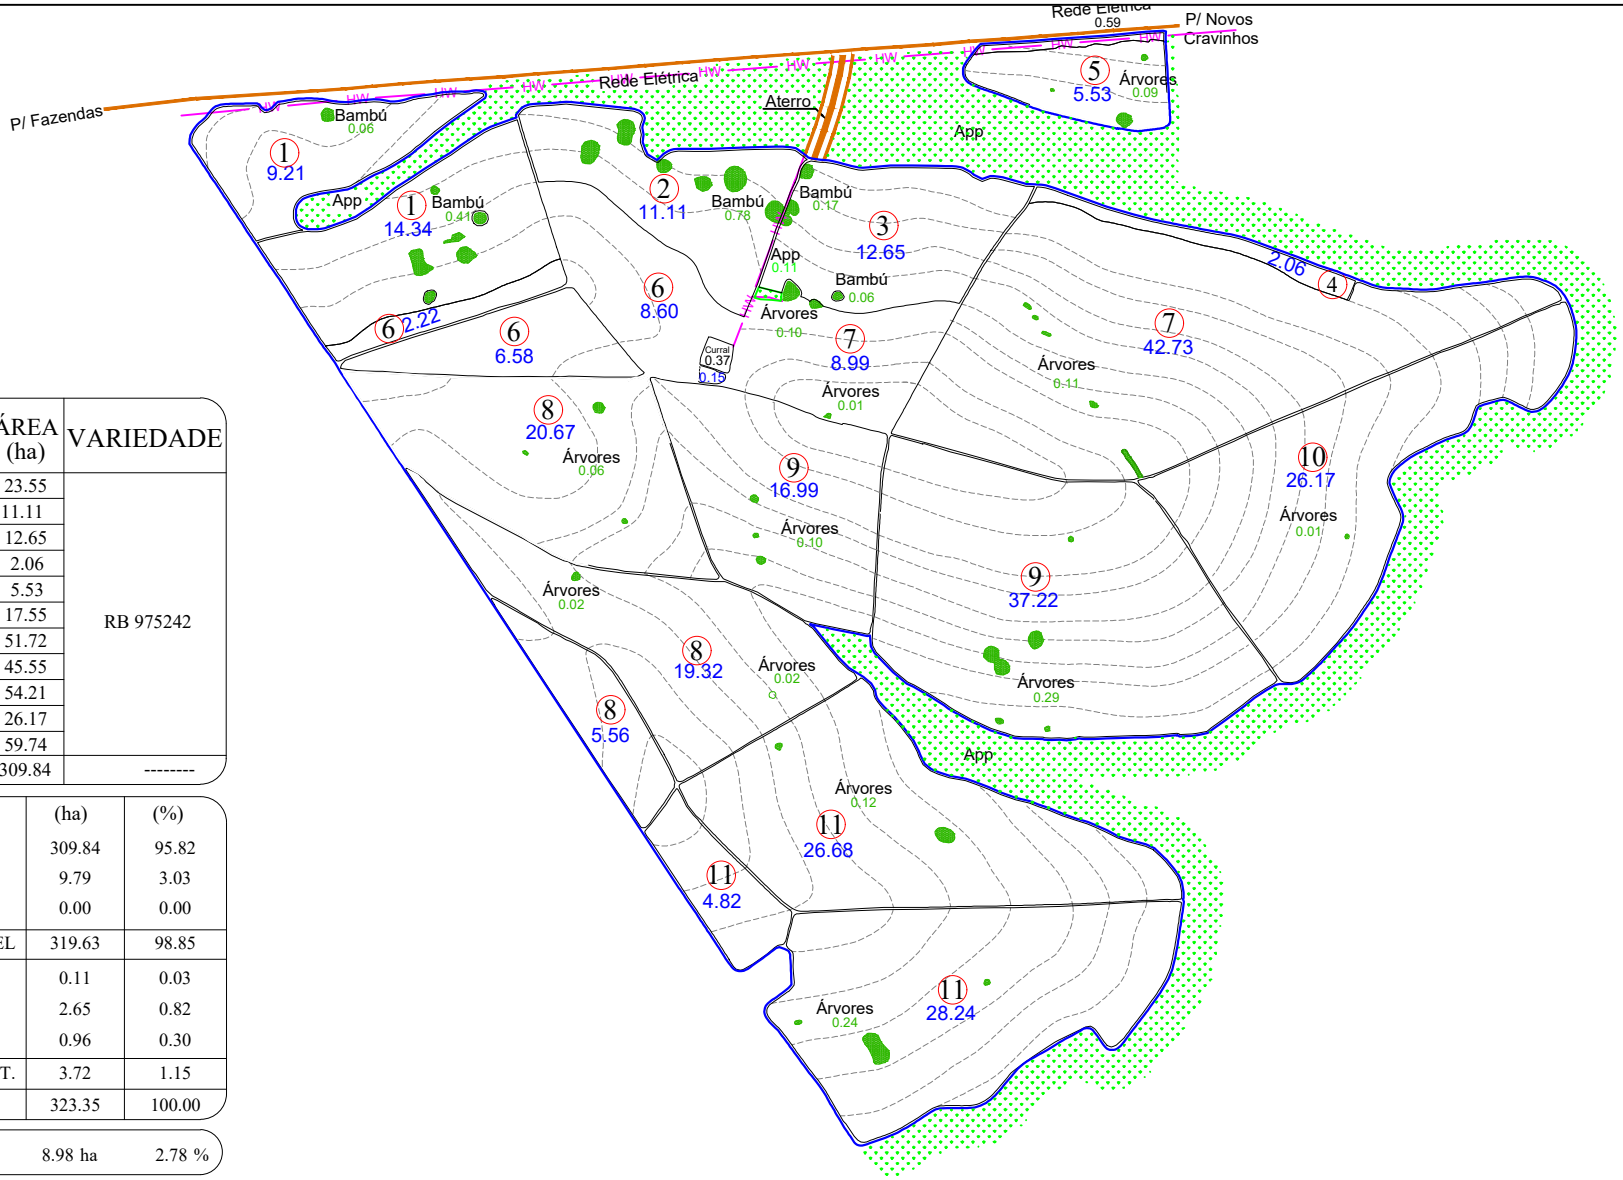

ZONA	Nº TAL.	DATA PL.	ÁREA (ha)	VARIEDADE
999	1	07/2022	23.55	RB 975242
	2		11.11	
	3		12.65	
	4		2.06	
	5	06/2023	5.53	
	6		17.55	
	7		51.72	
	8		45.55	
	9		54.21	
	10		26.17	
	11		59.74	
TOTAL PLANTIO			309.84	--------

ÁREAS	(ha)	(%)
PLANTIO	309.84	95.82
CARREADORES	9.79	3.03
OUTROS	0.00	0.00
SUB TOTAL AGRICULTÁVEL	319.63	98.85
AP.P.	0.11	0.03
ÁRVORES	2.65	0.82
OUTROS	0.96	0.30
SUB TOTAL NÃO AGRICULT.	3.72	1.15
ÁREA TOTAL	323.35	100.00

C. NÍVEL: 39032.41 m/l 8.98 ha 2.78 %


ESCALA: 1: 16.500

LEGENDA

- FAZENDA
- TALHÃO
- REDE ELÉTRICA
- TERRAÇO BASE LARGA
- TERRAÇO EMBUTIDO

ESPAÇAMENTO: 1.50 x 1.50
TIRO MÉDIO ESTIMADO: 000.00 m
D.V: 0.00 %

CROQUI DE ACESSO

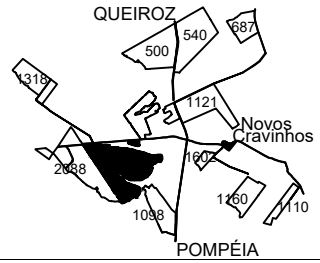

FAZENDA IPIRANGA

PROPRIETÁRIO: WANDERLEY ZANCHETTIN
COMPRADOR: CLEALCO S/A
MUNICÍPIO: POMPÉIA

DISTÂNCIAS (km):
UNID. I - Asfalto: 84.00 Terra.: 4.00
UNID.I I - Asfalto: 24.00 Terra.: 4.00
UNID. III -Asfalto: 80.00 Terra.: 4.00

COORDENADAS: E(X): 587839.89 N(Y): 7568515.82
LAT: -21°59'8.3845" LONG: -50°8'56.8260"
CLEALCO - AÇÚCAR E ALCOOL S/A - DEPARTAMENTO DE GEOTECNOLOGIA

LEVANTAMENTO VIA:
SATÉLITE
GPS / VANT
GOOGLE

UNIDADE: II
PARTE: A/A
FUNDO AGRÍCOLA: 307377

M:\01-Mapa de safra\Mapas Atualizados\Terceiro\307377 - Fazenda Ipiranga (Wanderley Zanchettin)\307377 - Fazenda Ipiranga (Wanderley Zanchettin).dwg

Fabiano Castro 24/07/25