
Clealco
Açúcar, Etanol e Energia

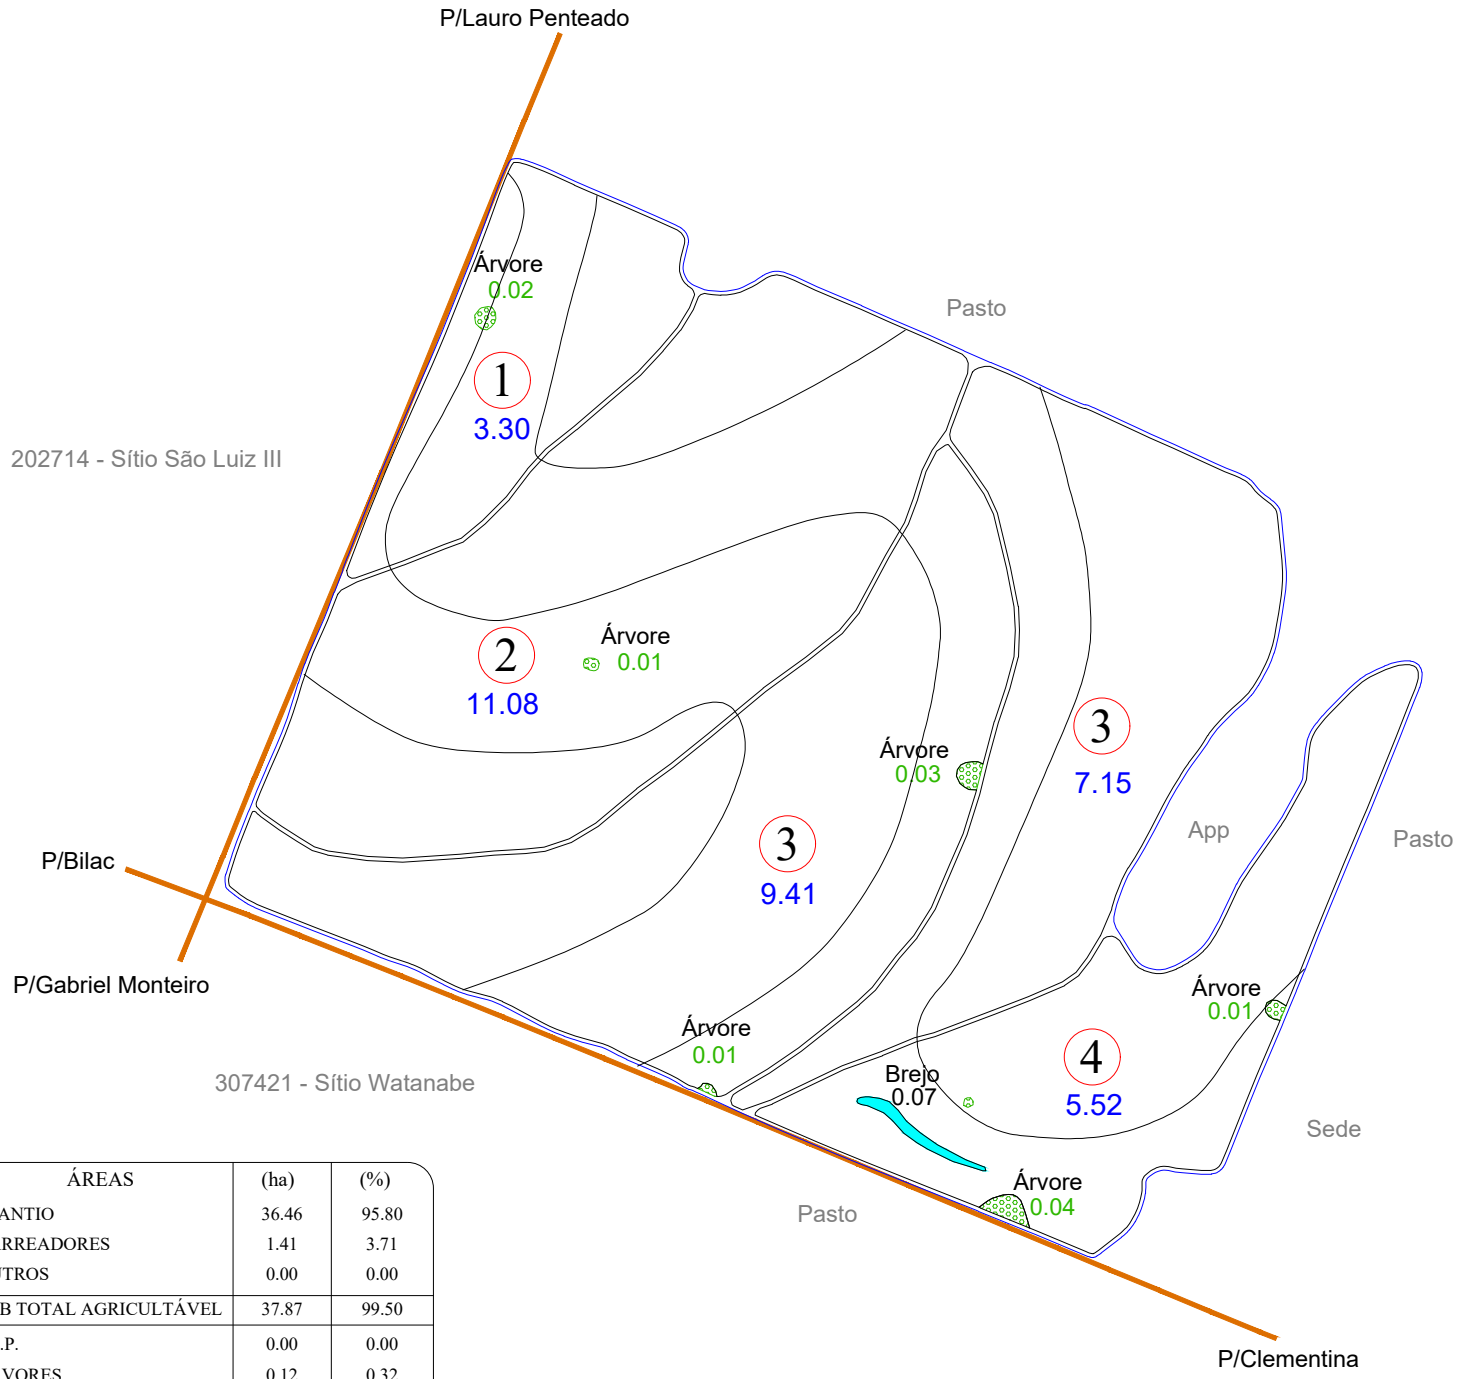

ÁREAS	(ha)	(%)
PLANTIO	36.46	95.80
CARREADORES	1.41	3.71
OUTROS	0.00	0.00
SUB TOTAL AGRICULTÁVEL	37.87	99.50
AP.P.	0.00	0.00
ÁRVORES	0.12	0.32
OUTROS	0.07	0.18
SUB TOTAL NÃO AGRICULT.	0.19	0.50
ÁREA TOTAL	38.06	100.00

C. NÍVEL: 3149.41 m/l 0.72 ha 1.90 %

LEGENDA


- FAZENDA
- TALHÃO
- REDE ELÉTRICA
- VAZIO
- TERRAÇO BASE LARGA
- TERRAÇO EMBUTIDO
- (P.O.A) PATIO DE OPERAÇÃO
- CARREGADO

ESPAÇAMENTO: 1.50 x 1.50
TIRO MÉDIO ESTIMADO: 214.35 m
D.V: 5.46%

ZONA	Nº TAL.	DATA PL.	ÁREA (ha)	VAR.
999	1	04/2023	3.30	CTC 04
	2		11.08	
	3		16.56	
	4		5.52	
TOTAL PLANTIO			36.46	--------

ESCALA: 1: 5.500

CROQUI DE ACESSO

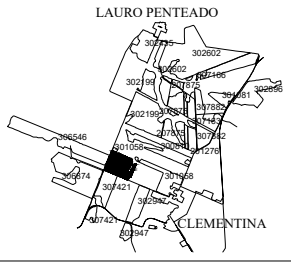

SÍTIO NATALIA

PROPRIETÁRIO: WALDEMIR V. POLLEGATO
COMPRADOR: CLEALCO
MUNICÍPIO: CLEMENTINA - SP

DISTÂNCIAS (km):
UNID. I - Asfalto: 4.00 Terra.: 3.00
UNID.I I - Asfalto: 51.00 Terra.: 4.70

COORDENADAS: E(X): 555291.90 N(Y): 7617193.12
LAT: -21°32'50.0023" LONG: -50°27'57.6653"

CLEALCO - AÇÚCAR E ALCOOL S/A - DEPARTAMENTO DE GEOTECNOLOGIA

LEVANTAMENTO VIA:
- SATÉLITE
- GPS / VANT
- GOOGLE

UNIDADE: I
PARTE: A/A
FUNDO AGRÍCOLA: 307386

M:\01-Mapa de safra\Mapas Atualizados\Terceiro\307386 - Sítio Natalia (Waldemir Vasques Polegato)\307386 - Sítio Natalia (Waldemir Vasques Polegato).dwg

Bruno Gamboa 31/08/26