ZONA DV	Nº TAL.	DATA PL.	ÁREA (ha)	VARIEDADE
999 3.62%	5	06/2022	6.83	CTC 04 RB 975242 RB 975201
	6		22.95	
	7		46.15	
	8		16.83	
	9		27.45	
TOTAL PLANTIO			120.21	--------

ÁREAS	(ha)	(%)
PLANTIO	120.21	96.47
CARREADORES	4.39	3.52
OUTROS	0.00	0.00
SUB TOTAL AGRICULTÁVEL	124.60	99.99
AP.P.	0.00	0.00
ÁRVORES	0.01	0.01
OUTROS	0.00	0.00
SUB TOTAL NÃO AGRICULT.	0.01	0.01
ÁREA TOTAL	124.61	100.00


C. NÍVEL: 0.00 m/l 0.00 ha 0.00 %

LEGENDA

- FAZENDA
- TALHÃO
- CURVA DE NÍVEL
- CARREADOR
- CONFRONTANTE
- REDE ELÉTRICA
- TRAJETO VAZIO
- TRAJETO CARREGADO


PLANTIO MANUAL - ESPAÇAMENTO: 1.50 X 1.50
TIRO MÉDIO ESTIMADO: 315.97 m

Clealco
Açúcar, Etanol e Energia

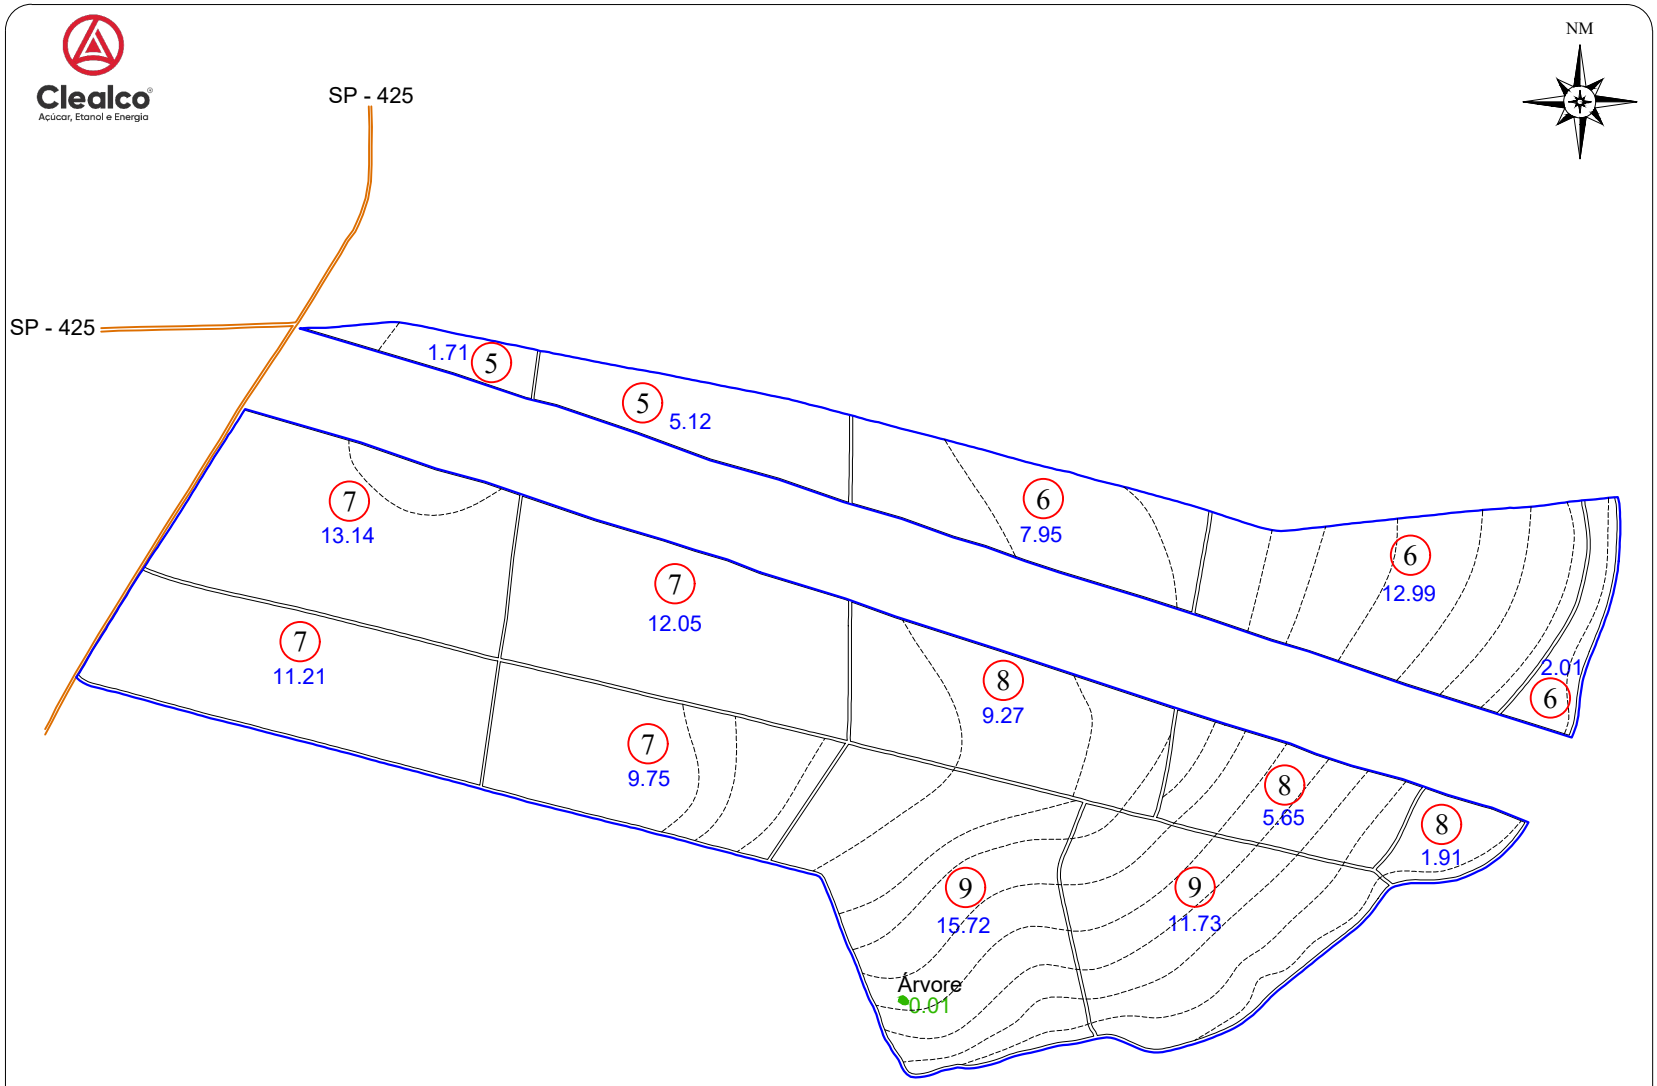

ESCALA: 1: 12.000

CROQUI DE ACESSO

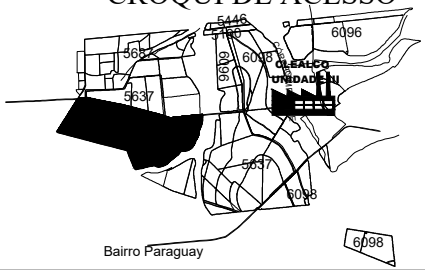

FAZENDA CAMPESTRE

PROPRIETÁRIO: ROSIMARA R. V. DE ANDRADE
COMPRADOR: CLEALCO S/A
MUNICÍPIO: PENÁPOLIS - SP

DISTÂNCIAS (km):
UNID. I - Asfalto: 60.70 Terra.: 2.50
UNID.I I - Asfalto: 49.50 Terra.: 2.50
UNID. III -Asfalto: 00.00 Terra.: 2.50

COORDENADAS: E(X): 588683.81 N(Y): 7624281.97
LAT: -21°28'54.6140" LONG: -50°8'38.1583"

CLEALCO - AÇÚCAR E ALCOOL S/A - DEPARTAMENTO DE TOPOGRAFIA

UNIDADE: I
PARTE: B/D
FUNDO AGRÍCOLA: 307388