ZONA DV	Nº TAL.	DATA PL.	ÁREA (ha)	VARIEDADE
999 3.41%	10	05/2022	31.53	RB 975201
TOTAL PLANTIO			31.53	--------

ÁREAS	(ha)	(%)
PLANTIO	31.53	98.15
CARREADORES	0.60	1.85
OUTROS	0.00	0.00
SUB TOTAL AGRICULTÁVEL	32.13	100.00
AP.P.	0.00	0.00
ÁRVORES	0.00	0.00
OUTROS	0.00	0.00
SUB TOTAL NÃO AGRICULT.	0.00	0.00
ÁREA TOTAL	32.13	100.00

C. NÍVEL: 4198.28 m/l 0.97 ha 3.01 %

LEGENDA

▬ FAZENDA	▬ CONFRONTANTE
▬ TALHÃO	-·- REDE ELÉTRICA
▪▪▪▪ CURVA DE NÍVEL	—▷ TRAJETO VAZIO
— CARREADOR	—► TRAJETO CARREGADO

PLANTIO MANUAL - ESPAÇAMENTO: 1.50 X 1.50
TIRO MÉDIO ESTIMADO: 315.97 m

Clealco
Açúcar, Etanol e Energia

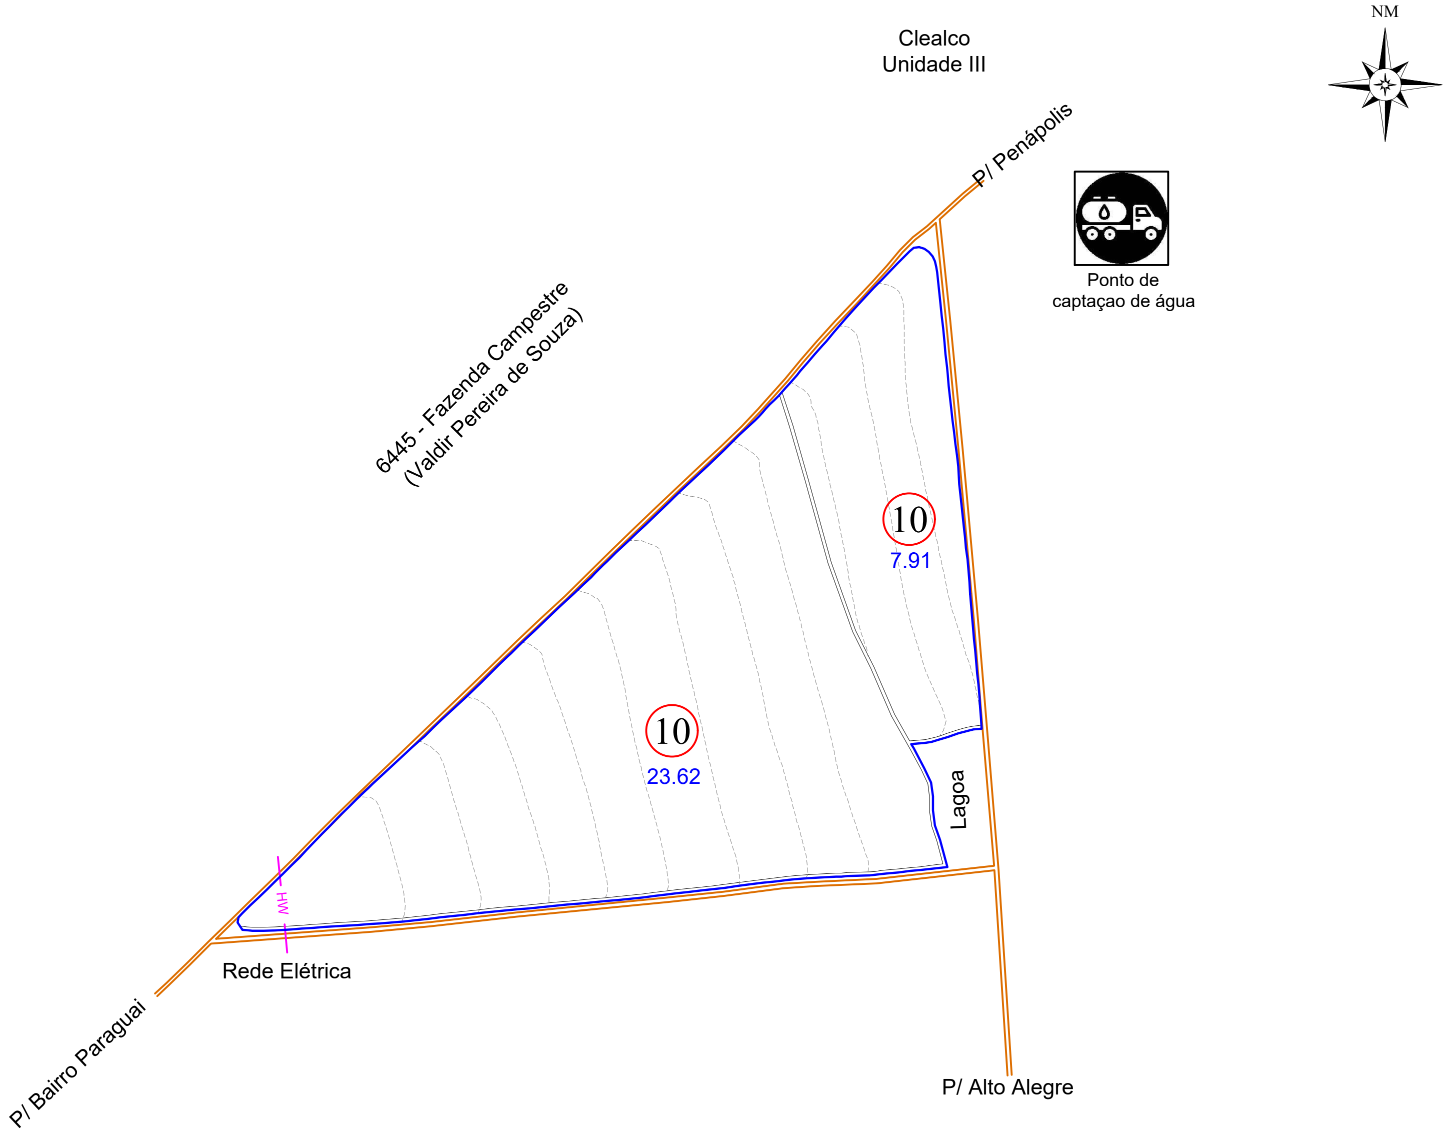

ESCALA: 1: 9.000

CROQUI DE ACESSO

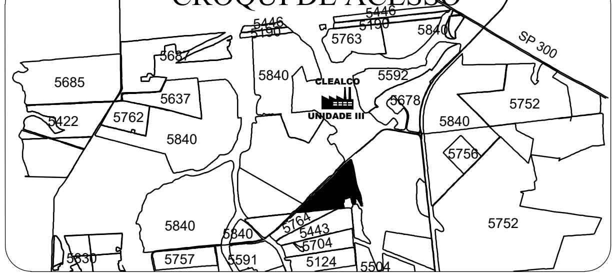

FAZENDA CAMPESTRE

PROPRIETÁRIO: ROSIMARA R. V. DE ANDRADE
COMPRADOR: CLEALCO S/A
MUNICÍPIO: PENÁPOLIS - SP

DISTÂNCIAS (km):

	Asfalto:		Terra.:	
UNID. I -	Asfalto:	60.70	Terra.:	2.50
UNID.I I -	Asfalto:	49.50	Terra.:	2.50
UNID. III -	Asfalto:	00.00	Terra.:	2.50

COORDENADAS: E(X): 591011.19 N(Y): 7623196.00
LAT: -21°29'29.5130" LONG: -50°7'17.0748"

CLEALCO - AÇÚCAR E ALCOOL S/A - DEPARTAMENTO DE TOPOGRAFIA

UNIDADE:
I

PARTE:
C/D

FUNDO AGRÍCOLA:
307388

M:\01-Mapa de safra\Mapas Atualizados\Terceiro\307388 - Fazenda Campestre (Rosimara R. Villanova de Andrade)\307388 C - Fazenda Campestre (Rosimara Rodrigues Villanova de Andrade).dwg

Fernanda Bezerra 25/10/22