ZONA DV	Nº TAL.	DATA PL.	ÁREA (ha)	VARIEDADE
999 3.81%	12	2026	96.37	REFORMA
TOTAL PLANTIO			96.37	--------

ÁREAS	(ha)	(%)
PLANTIO	96.37	95.85
CARREADORES	4.17	4.15
OUTROS	-	-
SUB TOTAL AGRICULTÁVEL	100.54	100.00
AP.P.	-	-
MATA	-	-
OUTROS	-	-
SUB TOTAL NÃO AGRICULT.	--------	--------
ÁREA TOTAL	100.54	100.00

C. NÍVEL:

LEGENDA

▬ FAZENDA	▬ CONFRONTANTE
▬ TALHÃO	▬ REDE ELÉTRICA
▪▪▪▪ CURVA DE NÍVEL	⇾ TRAJETO VAZIO
— CARREADOR	→ TRAJETO CARREGADO

PLANTIO MANUAL - ESPAÇAMENTO: 1.50 X 1.50
TIRO MÉDIO ESTIMADO: 315.97 m

Clealco
Açúcar, Etanol e Energia

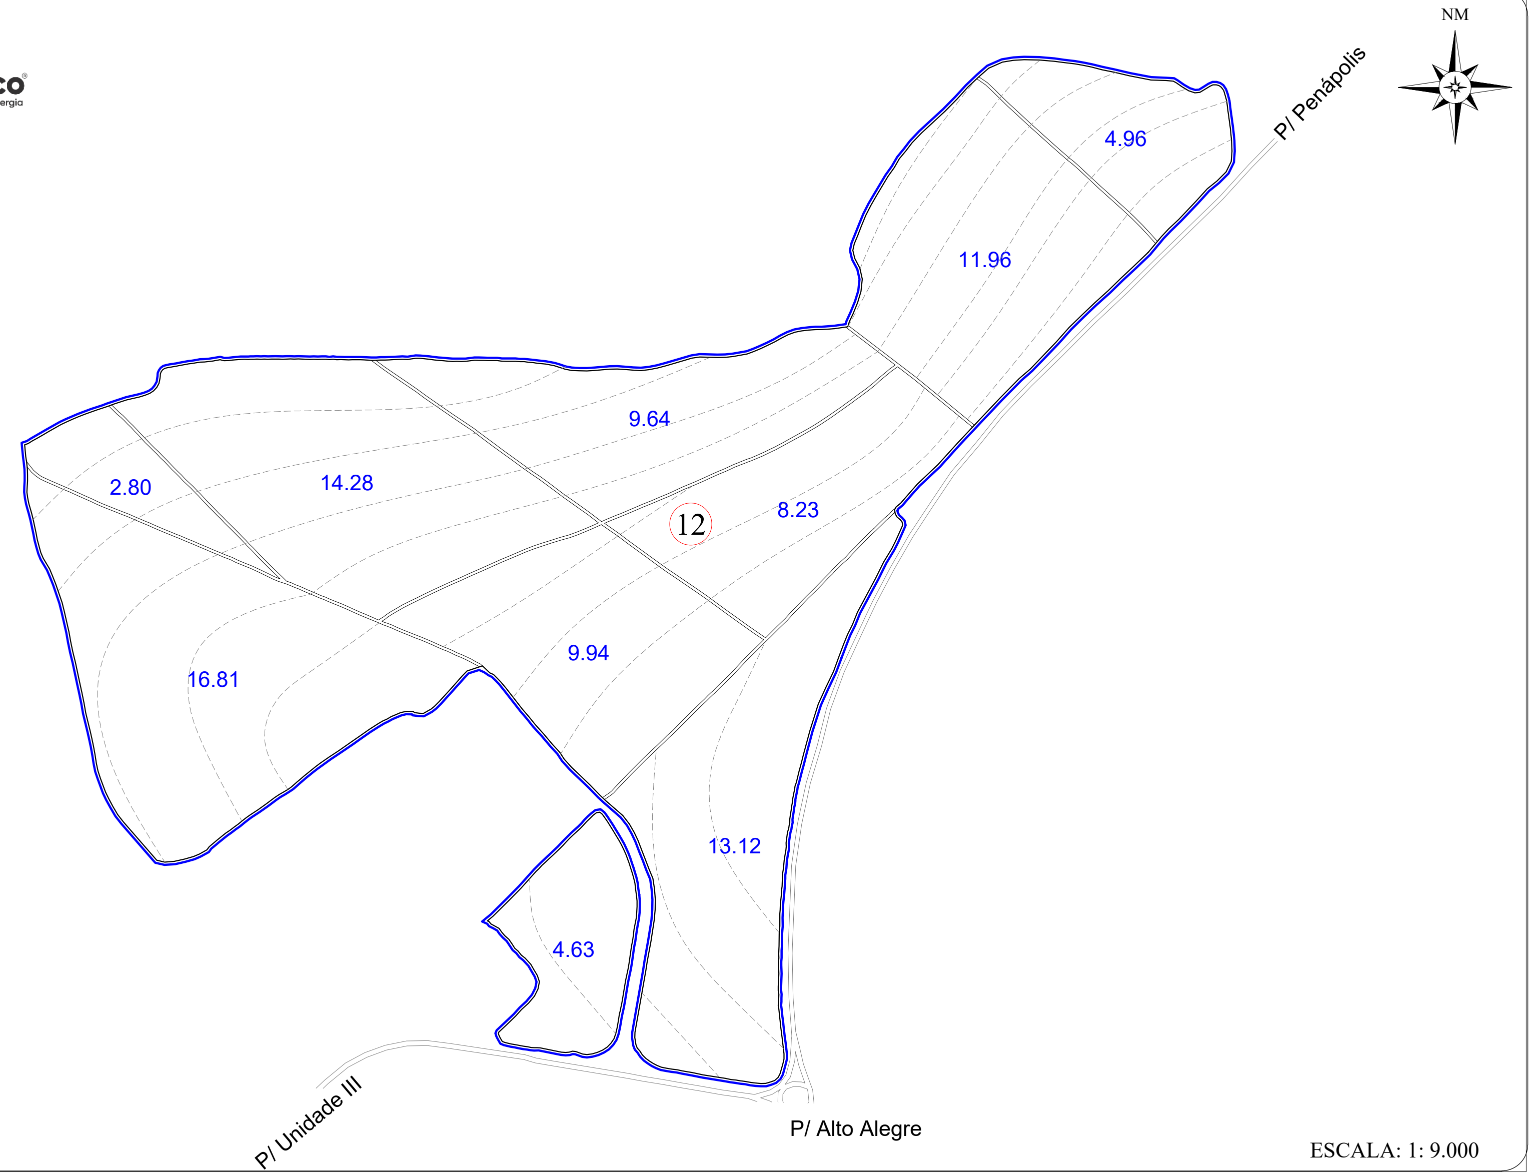

ESCALA: 1: 9.000

CROQUI DE ACESSO

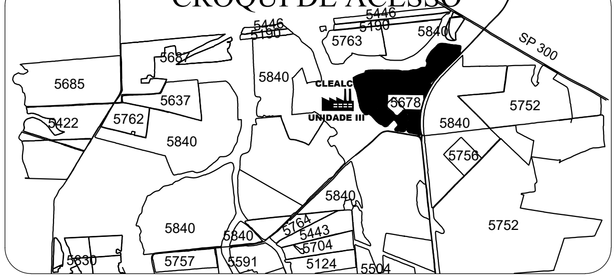

FAZENDA CAMPESTRE

PROPRIETÁRIO: ROSIMARA R. V. DE ANDRADE
COMPRADOR: CLEALCO S/A
MUNICÍPIO: PENÁPOLIS - SP

DISTÂNCIAS (km):

UNID. I -	Asfalto:	45.00	Terra.:	1.00
UNID.I I -	Asfalto:	55.00	Terra.:	1.00
UNID. III -	Asfalto:	00.00	Terra.:	5.50

COORDENADAS: E(X): 588593 N(Y): 7624835
LAT: 21°28'36,64393" LONG: 50°08'41,41872"

CLEALCO - AÇÚCAR E ALCOOL S/A - DEPARTAMENTO DE TOPOGRAFIA

UNIDADE:
I

PARTE:
D/D

FUNDO AGRÍCOLA:
307388

M:\01-Mapa de safra\Mapas Atualizados\Terceiro\307388 - Fazenda Campestre (Rosimara R. Villanova de Andrade)\307388 D - Fazenda Campestre (Rosimara Rodrigues Villanova de Andrade).dwg

Rafael 25/10/22