ZONA D.V.	Nº TAL.	DATA PL.	ÁREA (ha)	VARIEDADE
999 5.22%	1	04/2022	0.44	RB975242
	2		0.30	
	3		0.16	
	4		13.29	
	5		18.45	
	6		7.51	
	7		12.20	
	8		5.05	
TOTAL PLANTIO			57.40	--------


ÁREAS	(ha)	(%)
PLANTIO	57.40	92.44
CARREADORES	4.13	6.66
OUTROS	0.00	0.00
SUB TOTAL AGRICULTÁVEL	61.53	99.10
AP.P.	0.00	0.00
ÁRVORES	0.45	0.72
OUTROS	0.11	0.18
SUB TOTAL NÃO AGRICULT.	0.56	0.90
ÁREA TOTAL	62.09	100.00

C. NÍVEL: 9819.53 m/l 2.26 ha 3.64 %

LEGENDA


- FAZENDA
- TALHÃO
- CURVA DE NÍVEL
- CARREADOR
- CONFRONTANTE
- REDE ELÉTRICA
- TRAJETO VAZIO
- TRAJETO CARREGADO

PLANTIO MANUAL - ESPAÇAMENTO: 1.50 X 1.50
TIRO MÉDIO ESTIMADO: 000.00m

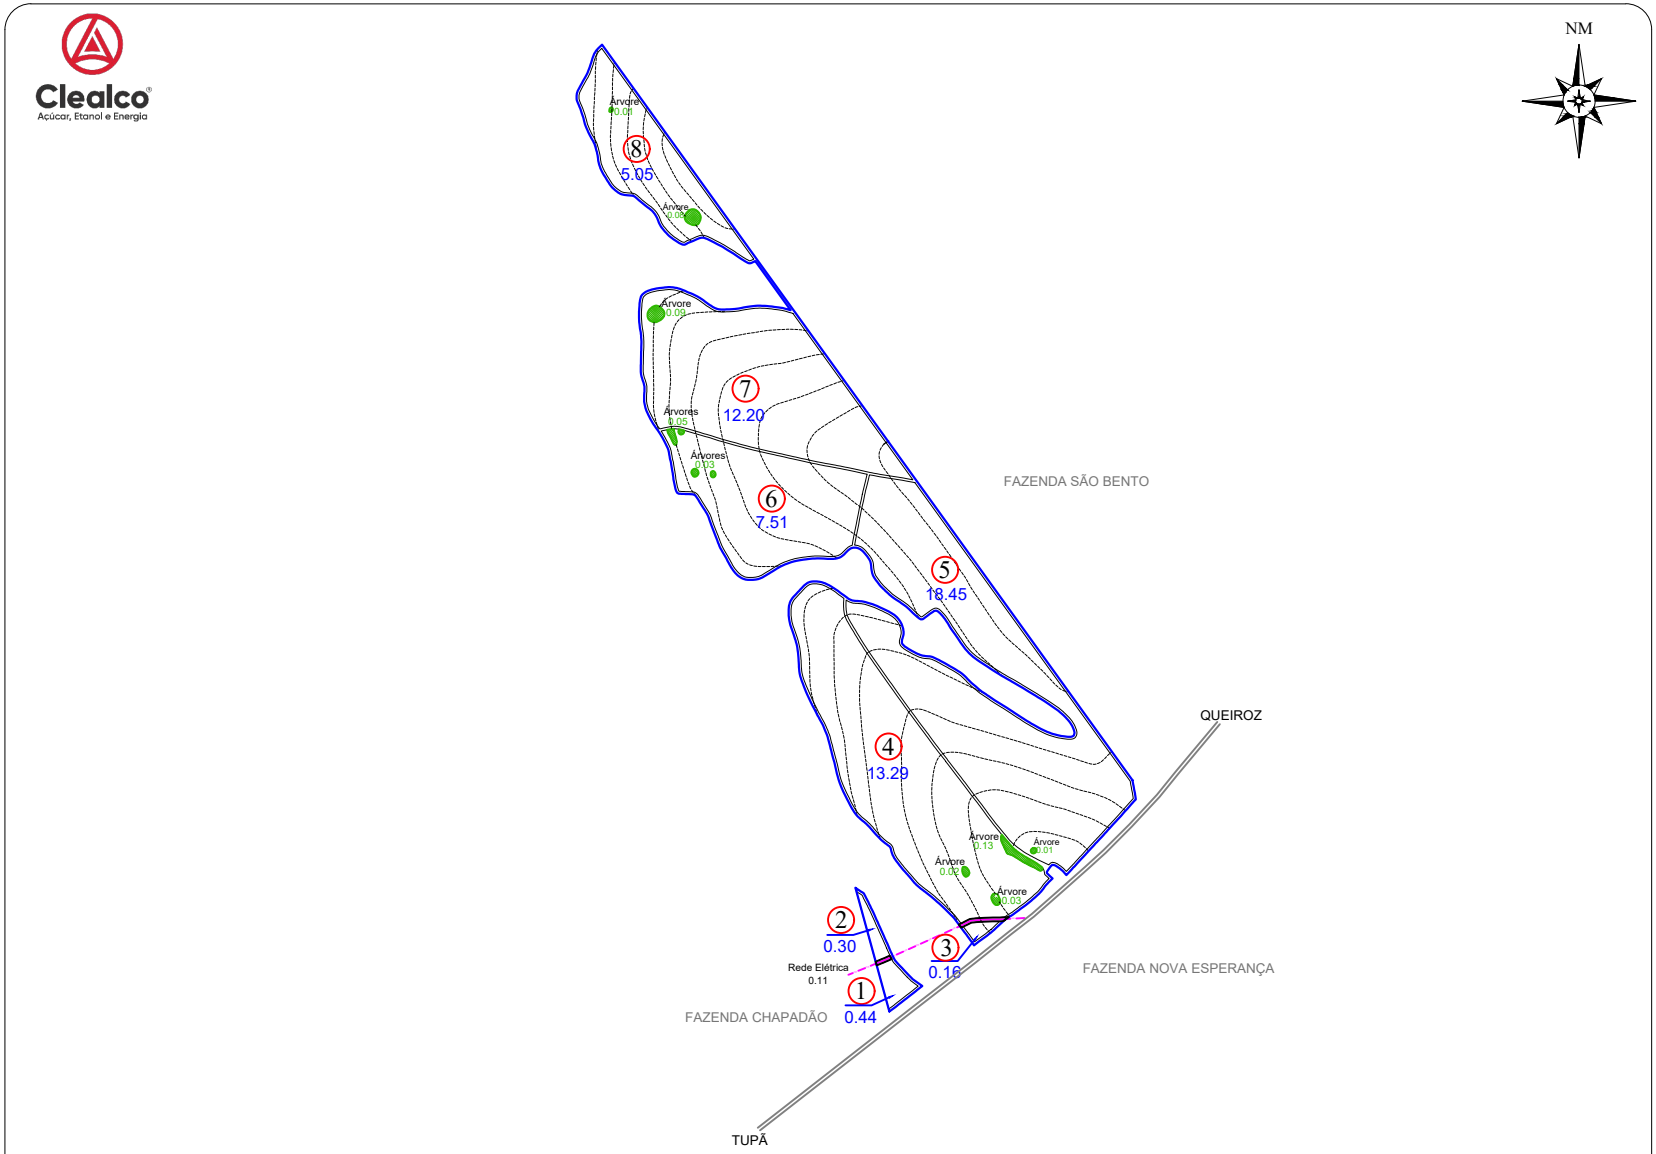

ESCALA: 1: 16.000

CROQUI DE ACESSO

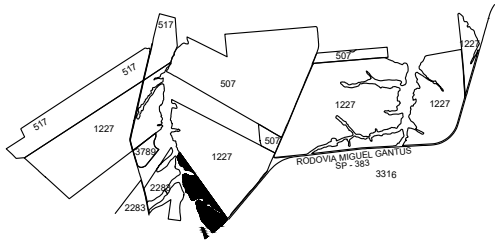

SÍTIO AEROPORTO

PROPRIETÁRIO: FELIPE DE FIGUEIREDO FERRAZ
COMPRADOR: CLEALCO S/A
MUNICÍPIO: QUEIROZ - SP

DISTÂNCIAS (km):
UNID. I - Asfalto: 35.00 Terra.: 24.40
UNID.I I - Asfalto: 15.50 Terra.: 1.50
UNID. III -Asfalto: 52.00 Terra.: 1.50

COORDENADAS: E(X): 570642.67 N(Y): 7582014.74
LAT: -21°51'52.1724" LONG: -50°18'58.5925"

CLEALCO - AÇÚCAR E ALCOOL S/A - DEPARTAMENTO DE TOPOGRAFIA

UNIDADE: II
PARTE: A/A
FUNDO AGRÍCOLA: 307392

M:\01-Mapa de safra\Mapas Atualizados\Terceiro\307392 - Sítio Aeroporto (Felipe Ferraz)\307392 - Sítio Aeroporto (Felipe Ferraz).dwg

Peterson Santos 10/04/23