ZONA D.V.	Nº TAL.	DATA PL.	ÁREA (ha)	VARIEDADE
999 4.62%	1	05/2023	12.31	RB 92579
	2		7.88	
	3		12.87	
TOTAL PLANTIO			33.06	--------


ÁREAS	(ha)	(%)
PLANTIO	33.06	95.37
CARREADORES	1.56	4.51
OUTROS	0.00	0.00
SUB TOTAL AGRICULTÁVEL	34.62	99.88
AP.P.	0.00	0.00
ÁRVORES	0.04	0.12
OUTROS	0.00	0.00
SUB TOTAL NÃO AGRICULT.	0.04	0.12
ÁREA TOTAL	34.66	100.00

C. NÍVEL: 4824.84 m/l 1.11 ha 3.20 %


LEGENDA

- FAZENDA
- TALHÃO
- CURVA DE NÍVEL
- CARREADOR
- CONFRONTANTE
- REDE ELÉTRICA
- TRAJETO VAZIO
- TRAJETO CARREGADO

PLANTIO MANUAL - ESPAÇAMENTO: 1.50 X 1.50

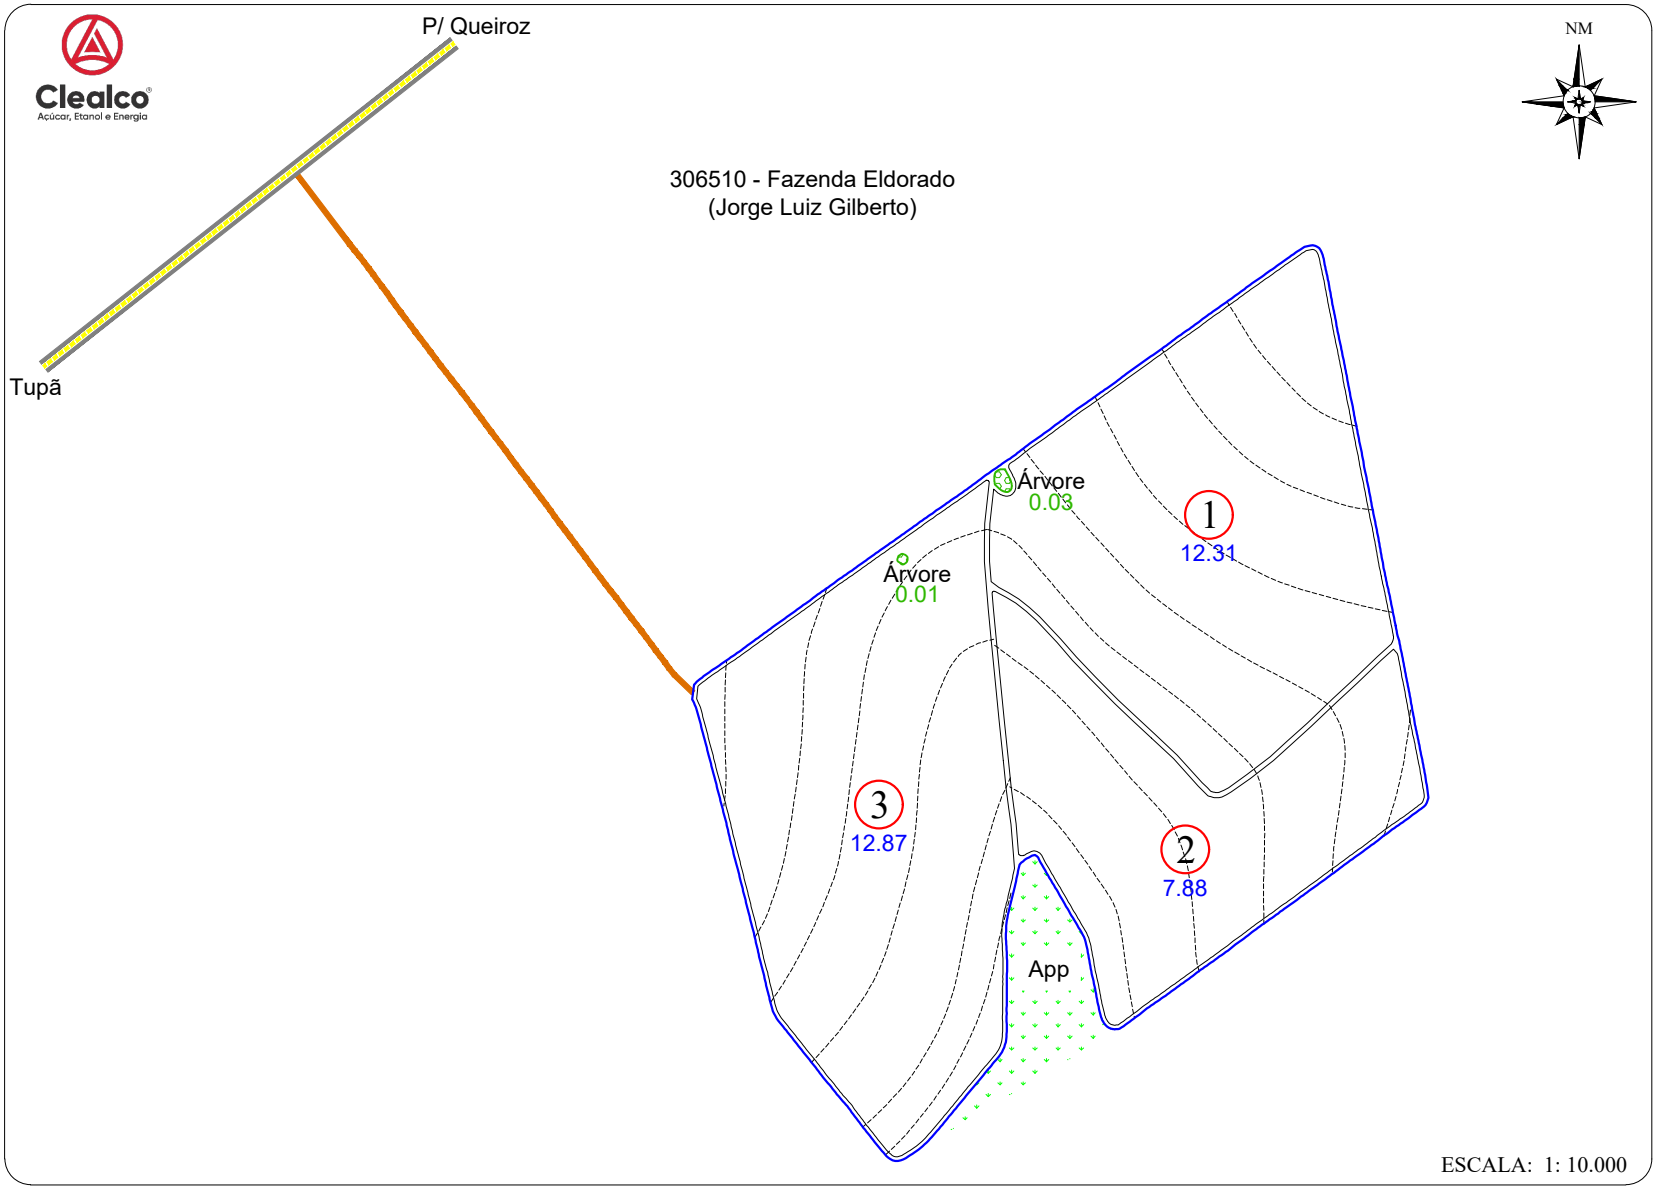

CROQUI DE ACESSO

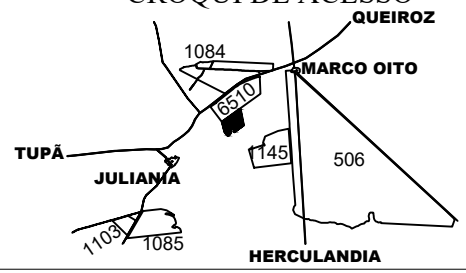

SÍTIO BELA LILIAN

PROPRIETÁRIO: FELIPE FERRAZ
COMPRADOR: CLEALCO S/A
MUNICÍPIO: HERCULÂNDIA

DISTÂNCIAS (km):
UNID. I - Asfalto: 32.50 Terra.: 23.50
UNID.I I - Asfalto: 16.70 Terra.: 2.10
UNID. III -Asfalto: 71.00 Terra.: 2.10

COORDENADAS: E(X): 567158.49 N(Y): 7579264.78
LAT: -21°53'22.1002" LONG: -50°20'59.5807"

CLEALCO - AÇÚCAR E ALCOOL S/A - DEPARTAMENTO DE TOPOGRAFIA

UNIDADE: II
PARTE: A/A
FUNDO AGRÍCOLA: 307393