ZONA D.V.	Nº TAL.	DATA PL.	ÁREA (ha)	VAR.
1	1	07/2023	15.94	RB 975242
6.59 %	2		2.03	
TOTAL PLANTIO			17.97	--------


ÁREAS	(ha)	(%)
PLANTIO	17.97	96.42
CARREADORES	0.67	3.58
OUTROS	0.00	0.00
SUB TOTAL AGRICULTÁVEL	18.64	100.00
AP.P.	0.00	0.00
ÁRVORES	0.00	0.00
OUTROS	0.00	0.00
SUB TOTAL NÃO AGRICULT.	0.00	0.00
ÁREA TOTAL	18.64	100.00

C. NÍVEL: 304.02 m/l 0.07 ha 0.38 %

LEGENDA


- FAZENDA
- TALHÃO
- CURVA DE NÍVEL
- CARREADOR
- CONFRONTANTE
- REDE ELÉTRICA
- TRAJETO VAZIO
- TRAJETO CARREGADO

PLANTIO MANUAL - ESPAÇAMENTO: 1.50 X 1.50
TIRO MÉDIO ESTIMADO: 257.27m

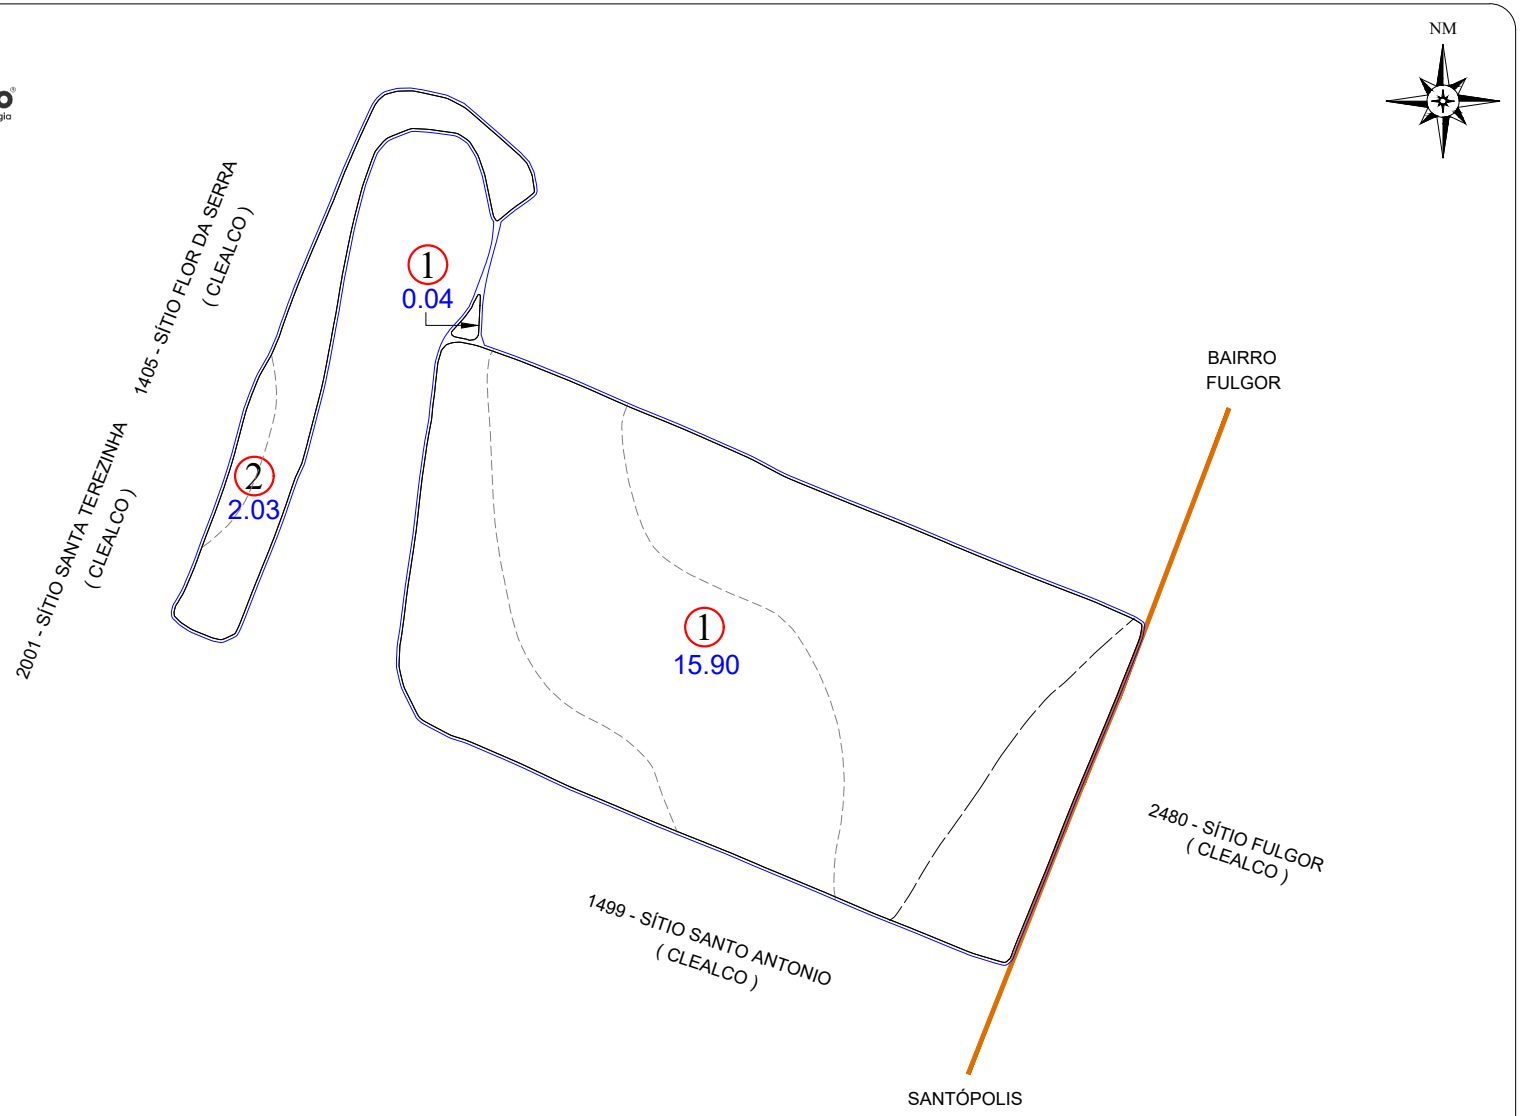

ESCALA: 1: 6.000

CROQUI DE ACESSO

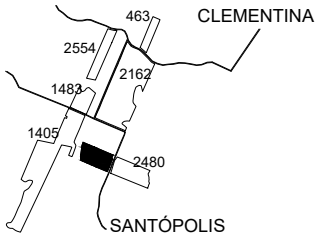

SÍTIO PERSERVERANÇAV

PROPRIETÁRIO: JAIR RODRIGUES VIEIRA
ARRENDATÁRIO: CLEALCO
MUNICÍPIO: CLEMENTINA

DISTÂNCIAS (km):
UNID. I - Asfalto: 11.50 Terra.: 5.30
UNID.I I - Asfalto: 51.00 Terra.: 5.30
UNID. III -Asfalto: 63.10 Terra.: 5.30

COORDENADAS: E(X): 550629.11 N(Y): 7610862.83
LAT: -21°36'16.3917" LONG: -50°30'39.0809"

CLEALCO - AÇÚCAR E ALCOOL S/A - DEPARTAMENTO DE TOPOGRAFIA

UNIDADE: I
PARTE: A/A
FUNDO AGRÍCOLA: 307397

Bruno Gamboa 22/12/23