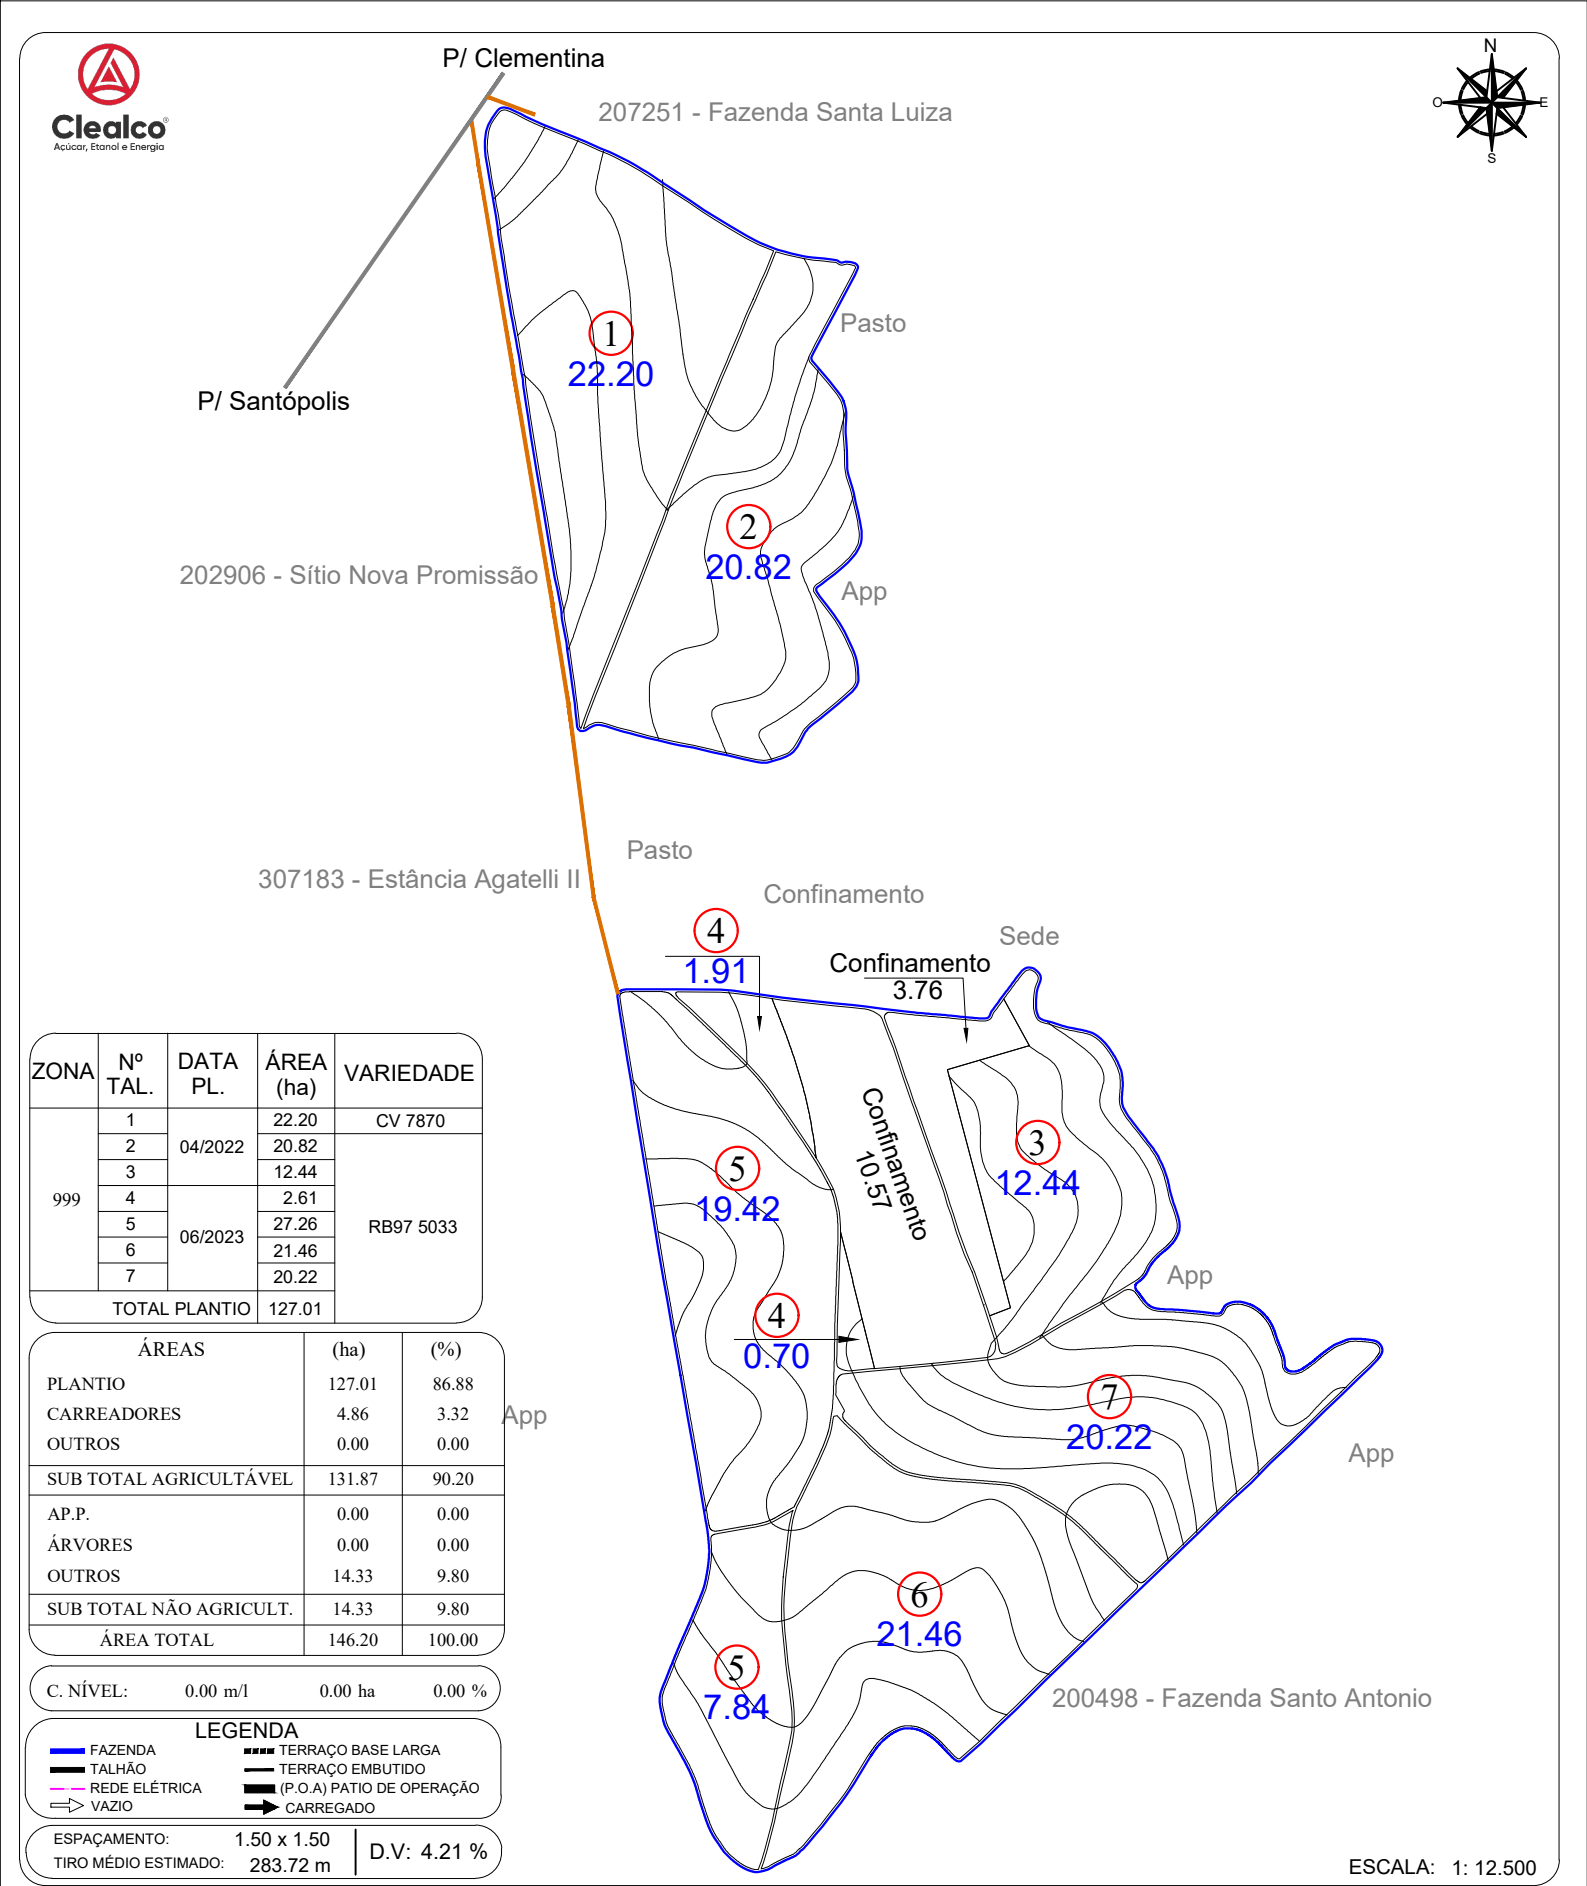


ZONA	Nº TAL.	DATA PL.	ÁREA (ha)	VARIEDADE
999	1	04/2022	22.20	CV 7870
	2		20.82	RB97 5033
	3		12.44	
	4	06/2023	2.61	
	5		27.26	
	6		21.46	
	7		20.22	
TOTAL PLANTIO			127.01	

ÁREAS	(ha)	(%)
PLANTIO	127.01	86.88
CARREADORES	4.86	3.32
OUTROS	0.00	0.00
SUB TOTAL AGRICULTÁVEL	131.87	90.20
AP.P.	0.00	0.00
ÁRVORES	0.00	0.00
OUTROS	14.33	9.80
SUB TOTAL NÃO AGRICULT.	14.33	9.80
ÁREA TOTAL	146.20	100.00

C. NÍVEL: 0.00 m/l 0.00 ha 0.00 %


LEGENDA

- FAZENDA
- TALHÃO
- REDE ELÉTRICA
- VAZIO
- TERRAÇO BASE LARGA
- TERRAÇO EMBUTIDO
- (P.O.A) PATIO DE OPERAÇÃO
- CARREGADO

ESPAÇAMENTO: 1.50 x 1.50
TIRO MÉDIO ESTIMADO: 283.72 m
D.V: 4.21 %

ESCALA: 1: 12.500

CROQUI DE ACESSO

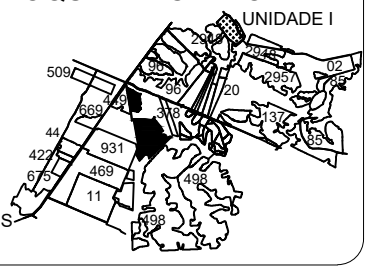

FAZENDA IRACEMA

PROPRIETÁRIO: VILMAR JOSÉ GASTALDI
COMPRADOR: CLEALCO
MUNICÍPIO: SANTÓPOLIS DO AGUAPEÍ - SP

DISTÂNCIAS (km):
UNID. I - Asfalto: 5.60 Terra.: 9.00
UNID.I I - Asfalto: 52.00 Terra.: 9.00

COORDENADAS: E(X): 555975.68 N(Y): 7609244.17
LAT: -21°37'8.4622" LONG: -50°27'32.9333"

CLEALCO - AÇÚCAR E ALCOOL S/A - DEPARTAMENTO DE GEOTECNOLOGIA

LEVANTAMENTO VIA:
- SATÉLITE
- GPS / VANT
- GOOGLE

UNIDADE: I
PARTE: A/B
FUNDO AGRÍCOLA: 307403

M:\01-Mapa de safra\Mapas Atualizados\Terceiro\307403 - Fazenda Iracema (Vilmar Gastaldi)\307403 A - Fazenda Iracema (Vilmar Gastaldi).dwg

Bruno Gamboa 08/05/26