
Clealco
Açúcar, Etanol e Energia

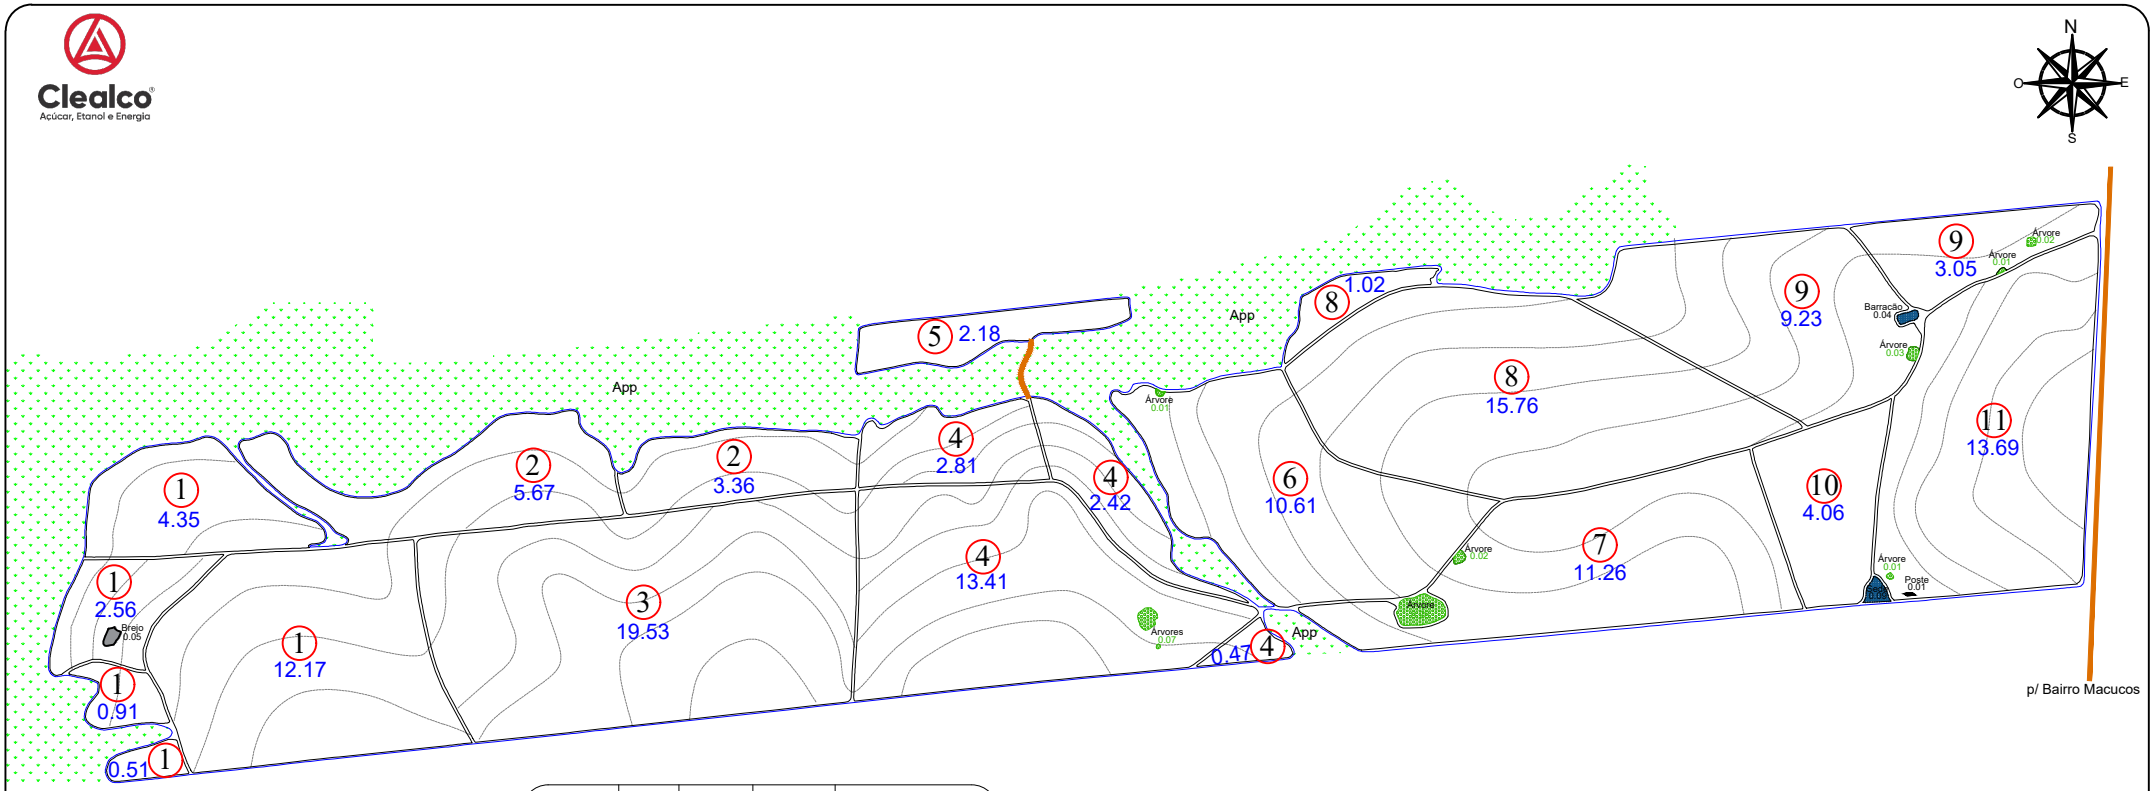

ÁREAS	(ha)	(%)
PLANTIO	139.03	96.00
CARREADORES	5.17	3.57
OUTROS	0.05	0.03
SUB TOTAL AGRICULTÁVEL	144.25	99.61
AP.P.	0.00	0.00
ÁRVORES	0.43	0.30
OUTROS	0.14	0.10
SUB TOTAL NÃO AGRICULT.	0.57	0.39
ÁREA TOTAL	144.82	100.00

C. NÍVEL: 19092.29 m/l 4.39 ha 3.03 %

ZONA	Nº TAL.	DATA PL.	ÁREA (ha)	VARIEDADE
999	1	06/2023	20.5	RB 975242
	2		9.03	
	3		19.53	
	4		19.11	
	5		2.18	
	6		10.61	
	7		11.26	
	8		16.78	
	9		12.28	
	10		4.06	
	11		13.69	
TOTAL PLANTIO			139.03	--------


ESCALA: 1: 11.500

LEGENDA

- FAZENDA
- TALHÃO
- REDE ELÉTRICA
- TERRAÇO BASE LARGA
- TERRAÇO EMBUTIDO

ESPAÇAMENTO: 1.50 x 1.50
TIRO MÉDIO ESTIMADO: 433.11 m
D.V: 5.66 %

CROQUI DE ACESSO

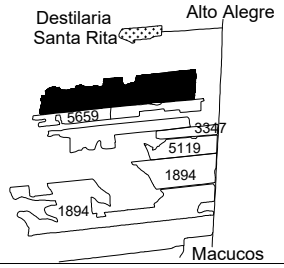

FAZENDA SÃO JOSÉ

PROPRIETÁRIO: WALDERMIR AP. CAPUTO
COMPRADOR: CLEALCO
MUNICÍPIO: ALTO ALEGRE - SP

DISTÂNCIAS (km):
UNID. I - Asfalto: 29.50 Terra.: 13.00
UNID.I I - Asfalto: 40.00 Terra.: 5.50

COORDENADAS: E(X): 583244.96 N(Y): 7607156.77
LAT: -21°38'12.5144" LONG: -50°11'44.0783"
CLEALCO - AÇÚCAR E ALCOOL S/A - DEPARTAMENTO DE GEOTECNOLOGIA

LEVANTAMENTO VIA:
SATÉLITE
GPS / VANT
GOOGLE

UNIDADE: II
PARTE: A/A
FUNDO AGRÍCOLA: 307404

M:\01-Mapa de safra\Mapas Atualizados\Terceiro\307404 - Fazenda São José (Waldemir Aparício Caputo)\307404 - Fazenda São José (Waldemir Aparício Caputo).dwg

Bruno Gamboa 25/07/25