ZONA D.V.	Nº TAL.	DATA PL.	ÁREA (ha)	VAR.
999	1	04/2022	15.95	RB 966928
4.69%	2		3.84	
TOTAL PLANTIO			19.79	--------

ÁREAS	(ha)	(%)
PLANTIO	19.79	83.80
CARREADORES	2.09	8.83
OUTROS	0.00	0.00
SUB TOTAL AGRICULTÁVEL	21.88	92.63
AP.P.	1.44	6.10
ÁRVORES	0.24	1.02
OUTROS	0.06	0.25
SUB TOTAL NÃO AGRICULT.	1.74	7.37
ÁREA TOTAL	23.62	100.00

C. NÍVEL:	1742.63 m/l	0.40 ha	1.70 %

LEGENDA

▬ FAZENDA	▬ CONFRONTANTE
▬ TALHÃO	─■─ REDE ELÉTRICA
▪▪▪▪ CURVA DE NÍVEL	⇨ TRAJETO VAZIO
─ CARREADOR	➞ TRAJETO CARREGADO

PLANTIO MANUAL - ESPAÇAMENTO: 1.50 X 1.50
TIRO MÉDIO ESTIMADO: 000.00m

Clealco
Açúcar, Etanol e Energia

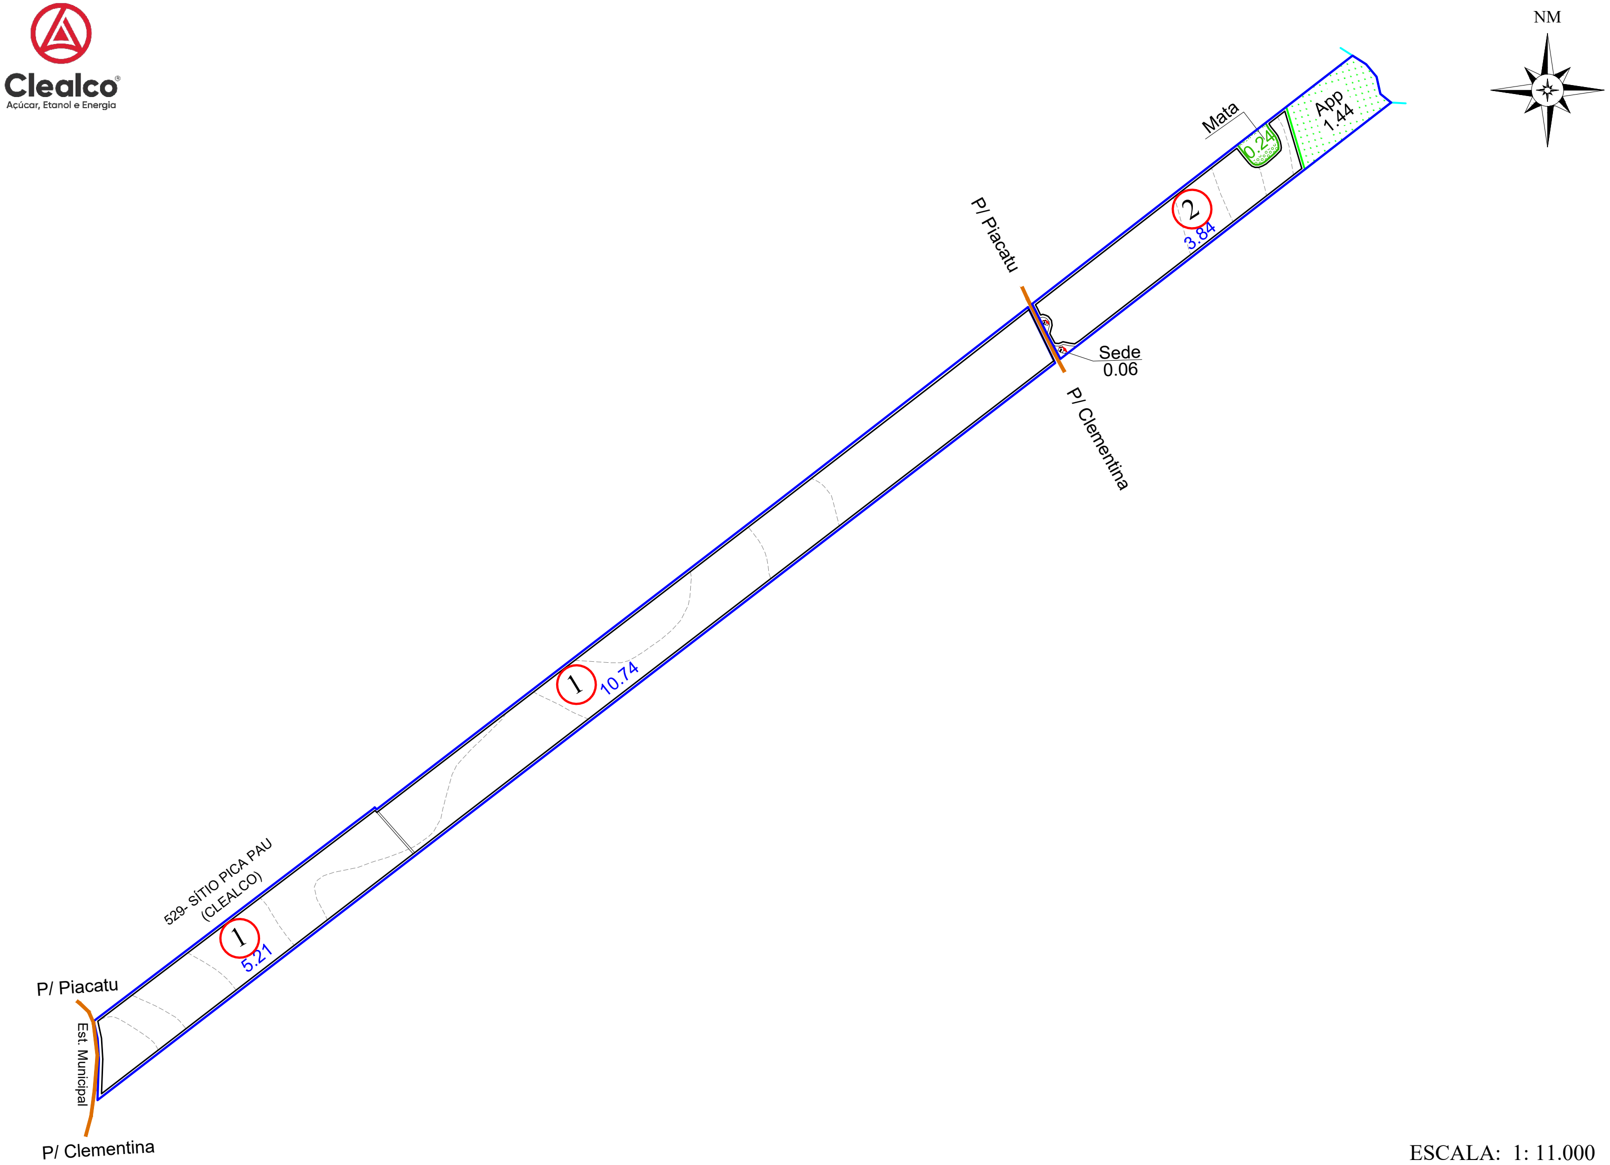

ESCALA: 1: 11.000

CROQUI DE ACESSO

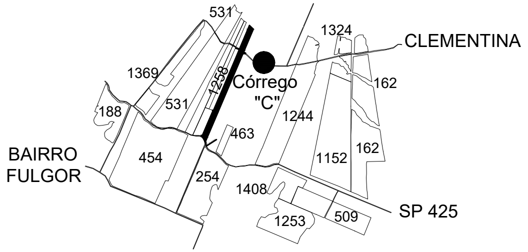

SÍTIO NOSSA SENHORA APARECIDA

PROPRIETÁRIO:	WALDEMIR V. POLLEGATO
COMPRADOR:	CLEALCO S/A
MUNICÍPIO:	CLEMENTINA - SP

DISTÂNCIAS (km):

	Asfalto:		Terra.:
UNID. I -	6.00		4.10
UNID.I I -	55.00		6.50
UNID. III -	51.00		4.10

COORDENADAS:		
E(X): 551838.31	N(Y): 7613632.73
LAT: -21°34'46.1760"	LONG: -50°29'57.3352"

CLEALCO - AÇÚCAR E ALCOOL S/A - DEPARTAMENTO DE TOPOGRAFIA

UNIDADE:
I

PARTE:
A/A

FUNDO AGRÍCOLA:
307405

M:\01-Mapa de safra\Mapas Atualizados\Terceiro\307405 - Sítio Nossa Senhora Aparecida (Waldemir V. Pollegato)\307405 - Sítio Nossa Senhora Aparecida (Waldemir V. Pollegato).dwg

Bruno Gamboa 02/06/23