ZONA D.V.	Nº TAL.	DATA PL.	ÁREA (ha)	VAR.
999 5.08 %	1	05/2022	4.23	RB966928
	2		7.30	
	3		5.81	
	4		15.93	
TOTAL PLANTIO			33.27	--------


ÁREAS	(ha)	(%)
PLANTIO	33.27	96.43
CARREADORES	1.21	3.51
OUTROS	0.00	0.00
SUB TOTAL AGRICULTÁVEL	34.48	99.94
AP.P.	0.00	0.00
ÁRVORES	0.00	0.00
OUTROS	0.02	0.06
SUB TOTAL NÃO AGRICULT.	0.02	0.06
ÁREA TOTAL	34.50	100.00

C. NÍVEL: 2396.54 m/l 0.55 ha 1.60 %


LEGENDA

- FAZENDA
- TALHÃO
- CURVA DE NÍVEL
- CARREADOR
- CONFRONTANTE
- REDE ELÉTRICA
- TRAJETO VAZIO
- TRAJETO CARREGADO

PLANTIO MANUAL - ESPAÇAMENTO: 1.50 X 1.50
TIRO MÉDIO ESTIMADO: 251.03 m

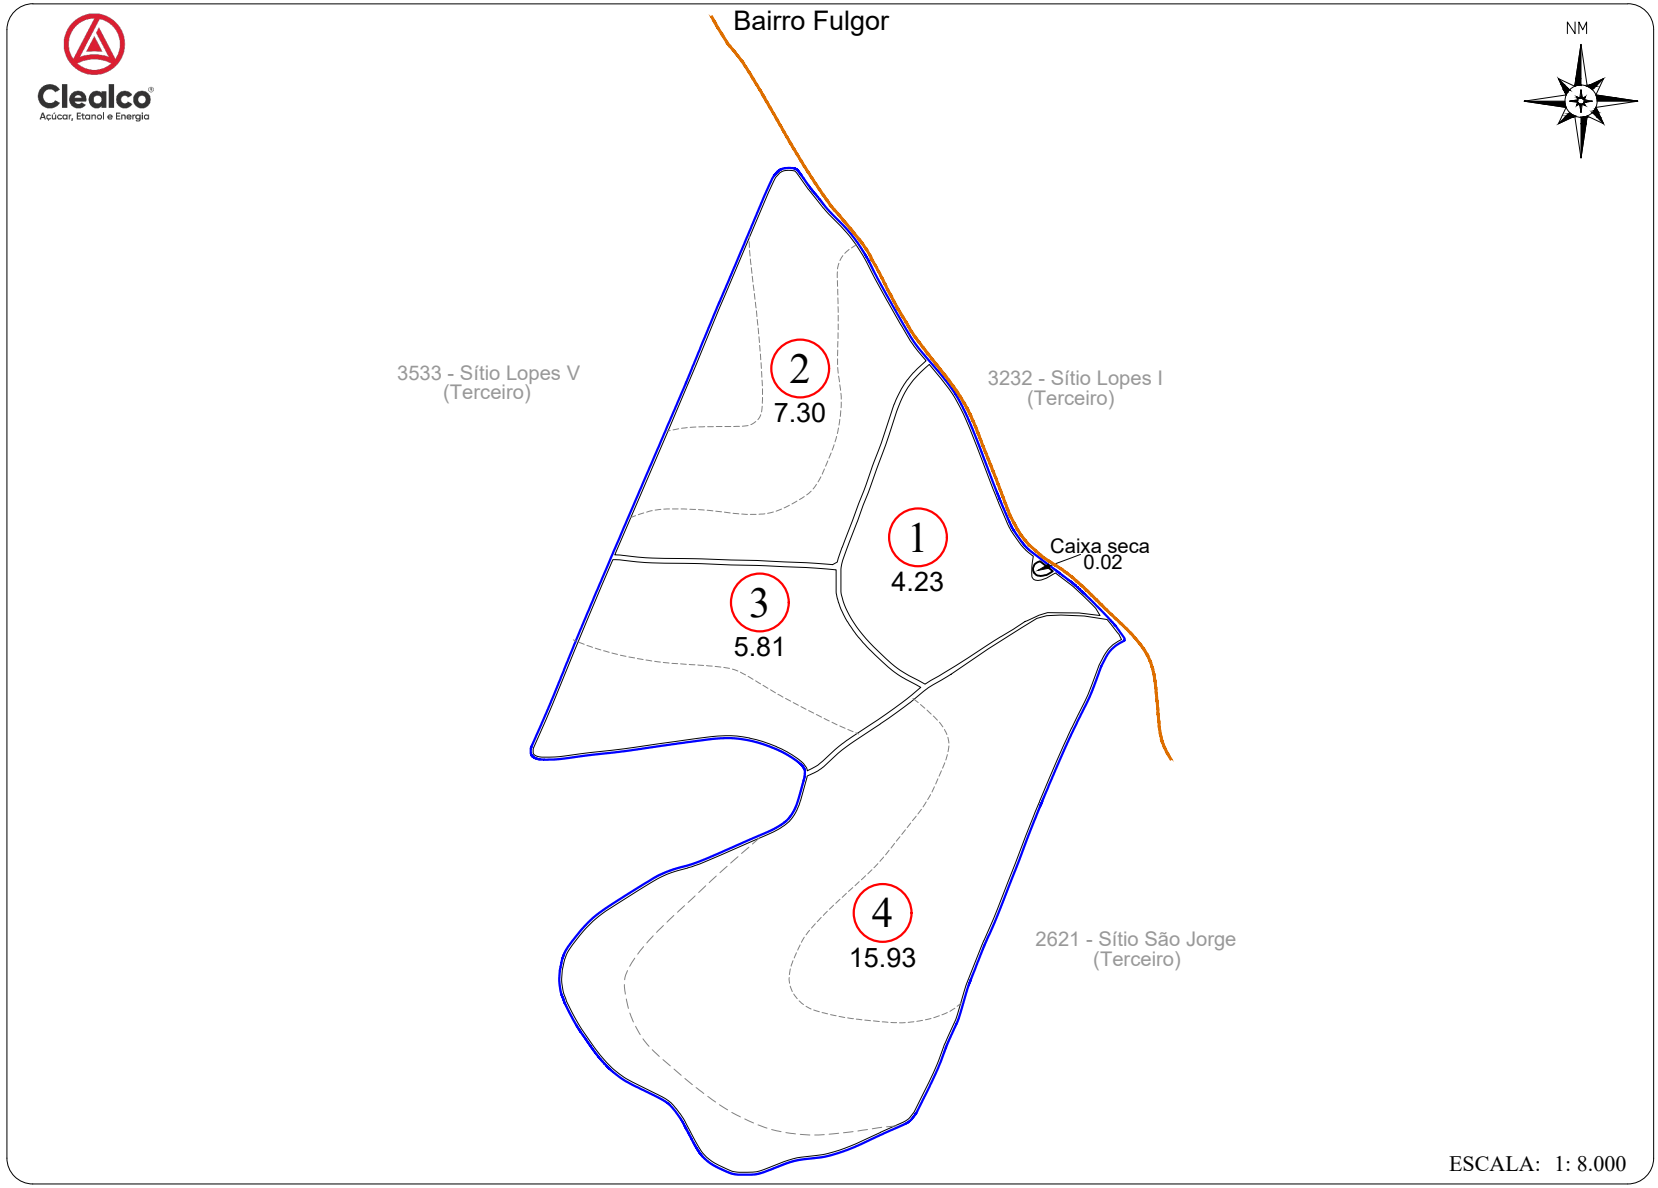

CROQUI DE ACESSO

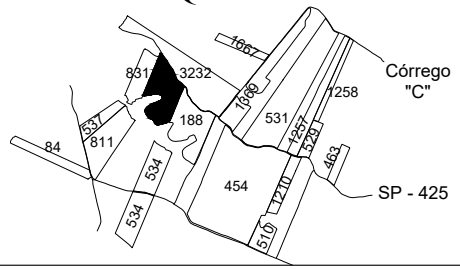

SITIO BABILONIA

PROPRIETÁRIO: RAFAEL ALEXIS LOPES
COMPRADOR: CLEALCO S/A
MUNICÍPIO: CLEMENTINA

DISTÂNCIAS (km):
UNID. I - Asfalto: 6.00 Terra.: 5.50
UNID.I I - Asfalto: 53.00 Terra.: 6.00
UNID. III -Asfalto: 45.00 Terra.: 5.50

COORDENADAS: E(X): 549661.5868 N(Y): 7614234.0218
LAT: 21° 34' 26,84195" LONG: 50° 31' 13,09238"

CLEALCO - AÇÚCAR E ALCOOL S/A - DEPARTAMENTO DE TOPOGRAFIA

UNIDADE: I
PARTE: A/A
FUNDO AGRÍCOLA: 307407